


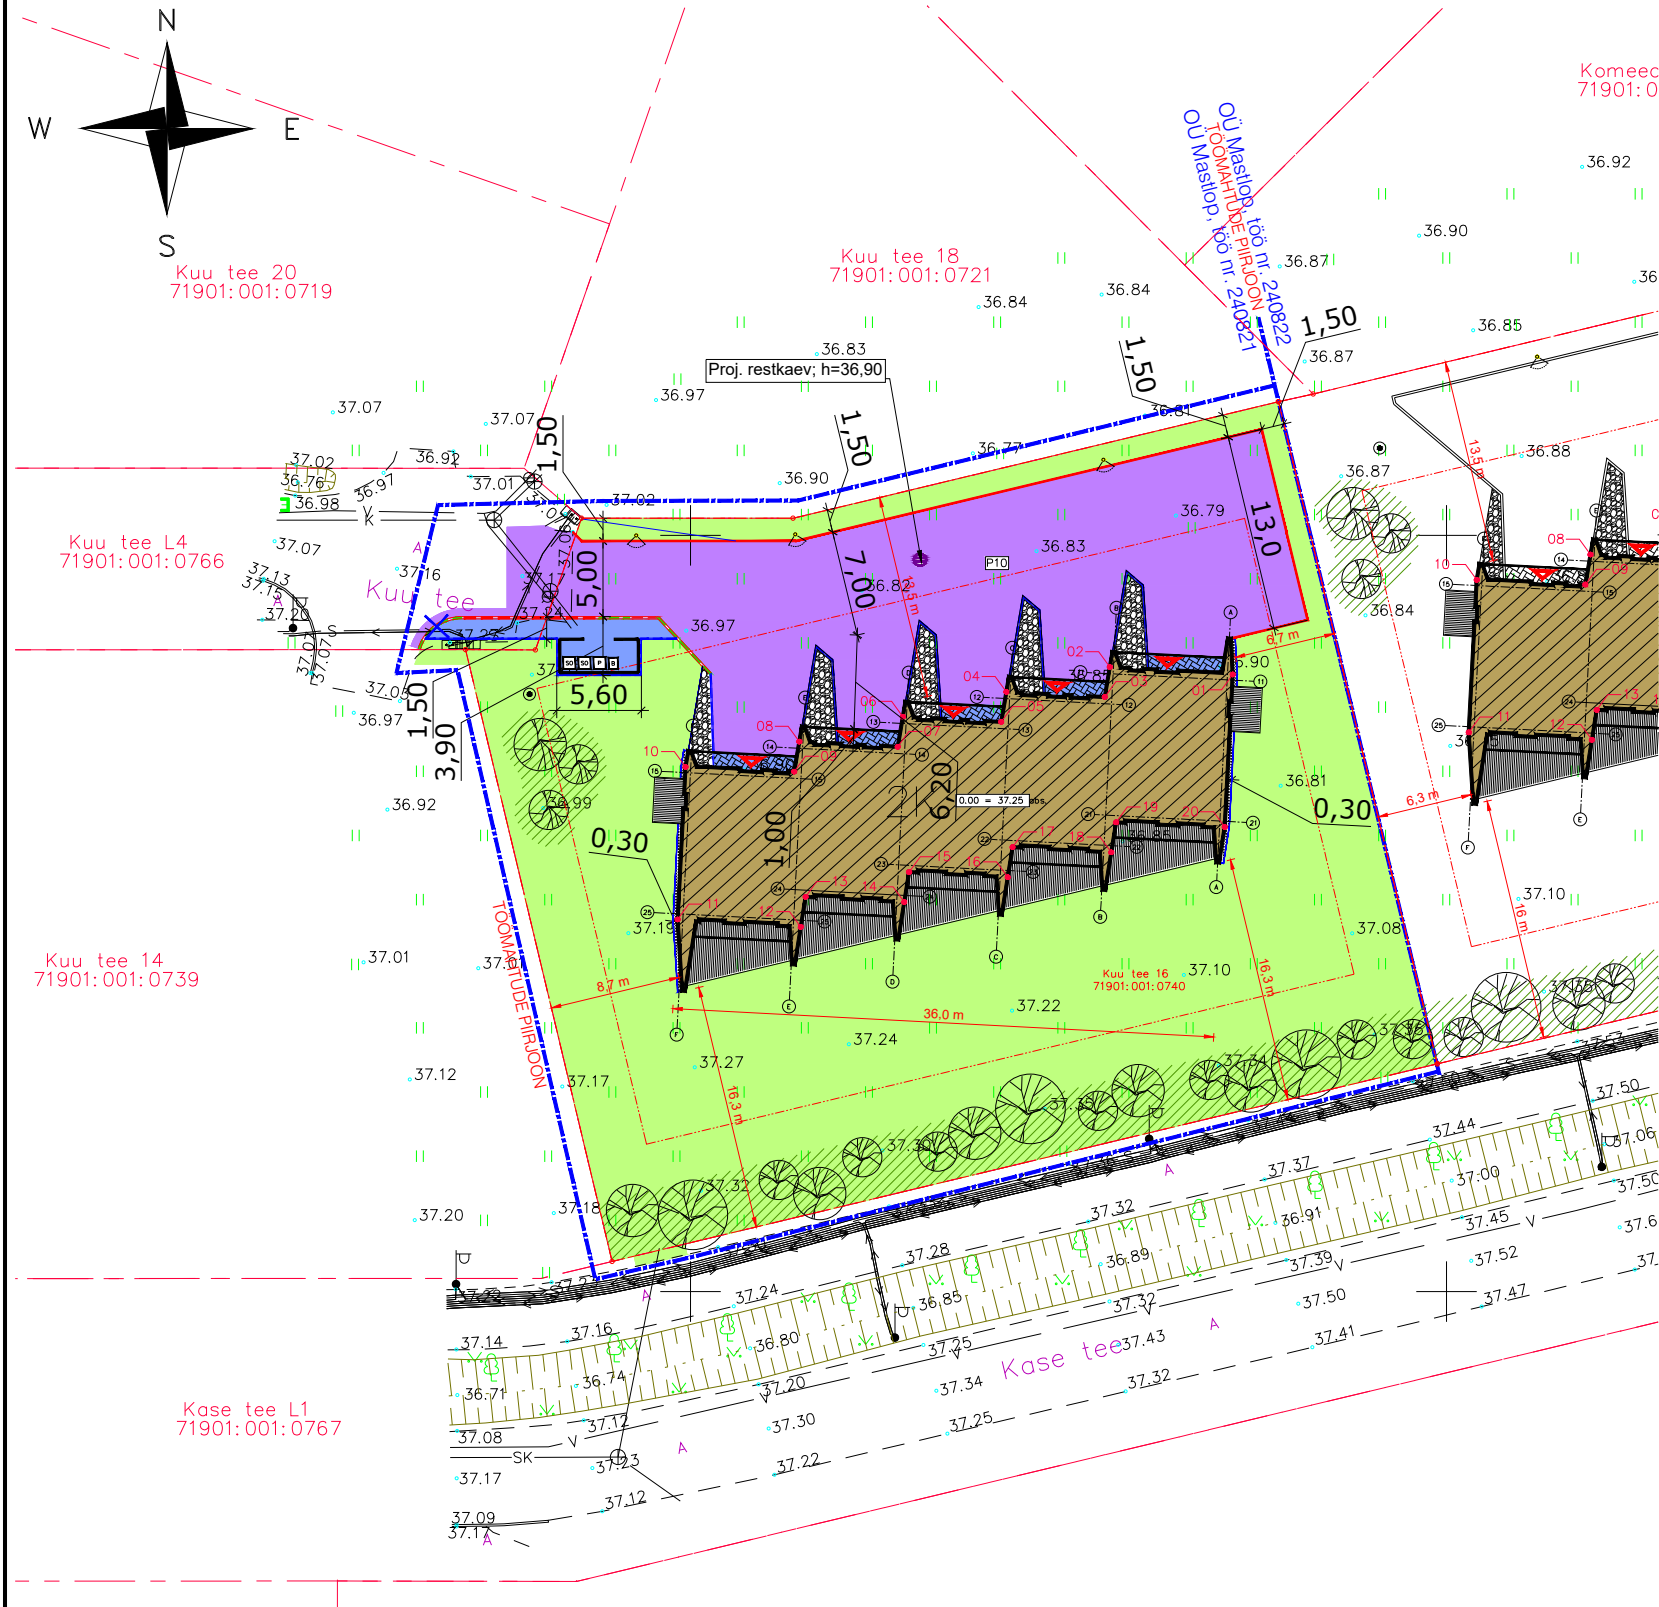

- OÜ Mastlop
TINGMÄRGID**
- OLEMASOLEV KINNISTU PIIR
 - OLEMASOLEV DRENAAZITORUSTIK
 - OLEMASOLEV REDVEEKANALISATSIOONITORUSTIK
 - OLEMASOLEV SADEVEEKANALISATSIOON
 - OLEMASOLEV VEETORUSTIK
 - OLEMASOLEV SIDEKABEL
 - OLEMASOLEV MADALPINGEKABEL
 - OLEMASOLEV NÖLV
 - OLEMASOLEV PUU
 - OLEMASOLEV KAEVUKAAS
 - OLEMASOLEV TV -POST
 - OLEMASOLEV LIKLUSMÄRK
 - OLEMASOLEV EL-KAPP
 - PROJEKTEERTAV SÕDUTEE KATTE SERV
 - PROJEKTEERTAV SÕDUTEE PEENRA SERV
 - PROJEKTEERTAV SÕDUTEE AB KATE/ KATTE TAASTAMINE
 - PROJEKTEERTAV KÕNITEE BETOONKIVIKATE (h=8cm)
 - PROJEKTEERTAV GRANITKIVI SÕLMETEST MULTSALA
 - PROJEKTEERTAV GRANITSÕLMETEST SOKLI ÄÄRE SILLUTIS
 - PROJEKTEERTAV/TAASTATAV MURLIPIND (h=15cm)
 - PROJEKTEERTAV SÕDUTEE ÄÄREKIVI (80x15x20cm, h=5 cm)
 - PROJEKTEERTAV SÕDUTEE ÄÄREKIVI (80x15x20cm, h=10 cm)
 - PROJEKTEERTAV KÕNITEE ÄÄREKIVI (100x8x20cm, h=2 cm)
 - PROJEKTEERTAV PUUDUST PEENRAÄÄRS
 - TÖÖMAHTLUSE PIIRUJOON
 - LIKVIDEERTAV ÄÄREKIVI

- Arhitekt11 OÜ, töö nr. KUU16
TINGMÄRGID
- Proj. hoone 2h
 - Hoonealusala
 - Proj. Murupind
 - Proj. Kõrghajustus
 - Proj. Hoonesse/Arundile
sõltuvus
 - Pt10
 - Proj. Põuamasti osukoht
 - Proj. hoone nurgapunkt
 - Proj. 1.5 m kõrge prüglöödku
lõiged
 - Proj. 1.5 m kõrge prüglöödku
lõiged
 - Postivõrgustik

KUU TEE 16	
PROJ.-HOONE TEHNILISED	
NAITAJAD	2
TOORPÕHUS	19.3
TOORPÕHUSKLAAS	
NETOPIND	607.2 m²
- sh. Eluruumide pind	584.2 m²
- sh. Tehn. pind	13.0 m²
BRUTO PIND	778.6 m²
HOONE MAHT	495.0 m³
HOONEALINE PIND	179.3 m²
KRUNDI PINDALA	2627.0 m²
KRUNDI TASUVUS	15.0 ‰
PARKIMISKOHTE ARV	10

MÄRKUSED:

- 1) Geodeesia koostaja OÜ Radiaan. Teostatud 6.11.2024.a. Töö nr. 2578G24
- 2) Projekteeritud ja olemasolev katend tuleb omavahel kõrguslikult kokku viia
- 3) Kui ol.olevat katendit kahjustatakse suuremas ulatuses kui projektokumentatsioonis kajastatud, tuleb see normidekohaselt taastada.

Mastlop

OÜ Mastlop

Reg.kood 12618952; EEP003122; ELK000079
Peterburi tee 2F, Tallinn 11415
tel. +372 56 24 26 34, e-mail ppoltsam@gmail.com

Projektijuht	Pärt Põltsam
Projekteeris	Pärt Põltsam
Kontrollis	Pärt Põltsam (tunnistuse nr. 163405/163406)
Koostatud / trükitud: 09.05.2025/ 19.05.2025	

Projekti nimetus:	KUU TEE 16 RIDAELAMU TEEDE-EHITUSLIK OSA	Töö nr:	240821
Asukoht:	KUU TEE 16/KUU TEE L4 SAKU ALEVIK, SAKU VALD, HARJU MK	Leht nr:	TL-02
Tellijä:	Saku Arendus OÜ	Stadium:	PÕHIPROJEKT
Joonise nimetus:	ASENDIPLAAN	Mõõtkava:	1:500