


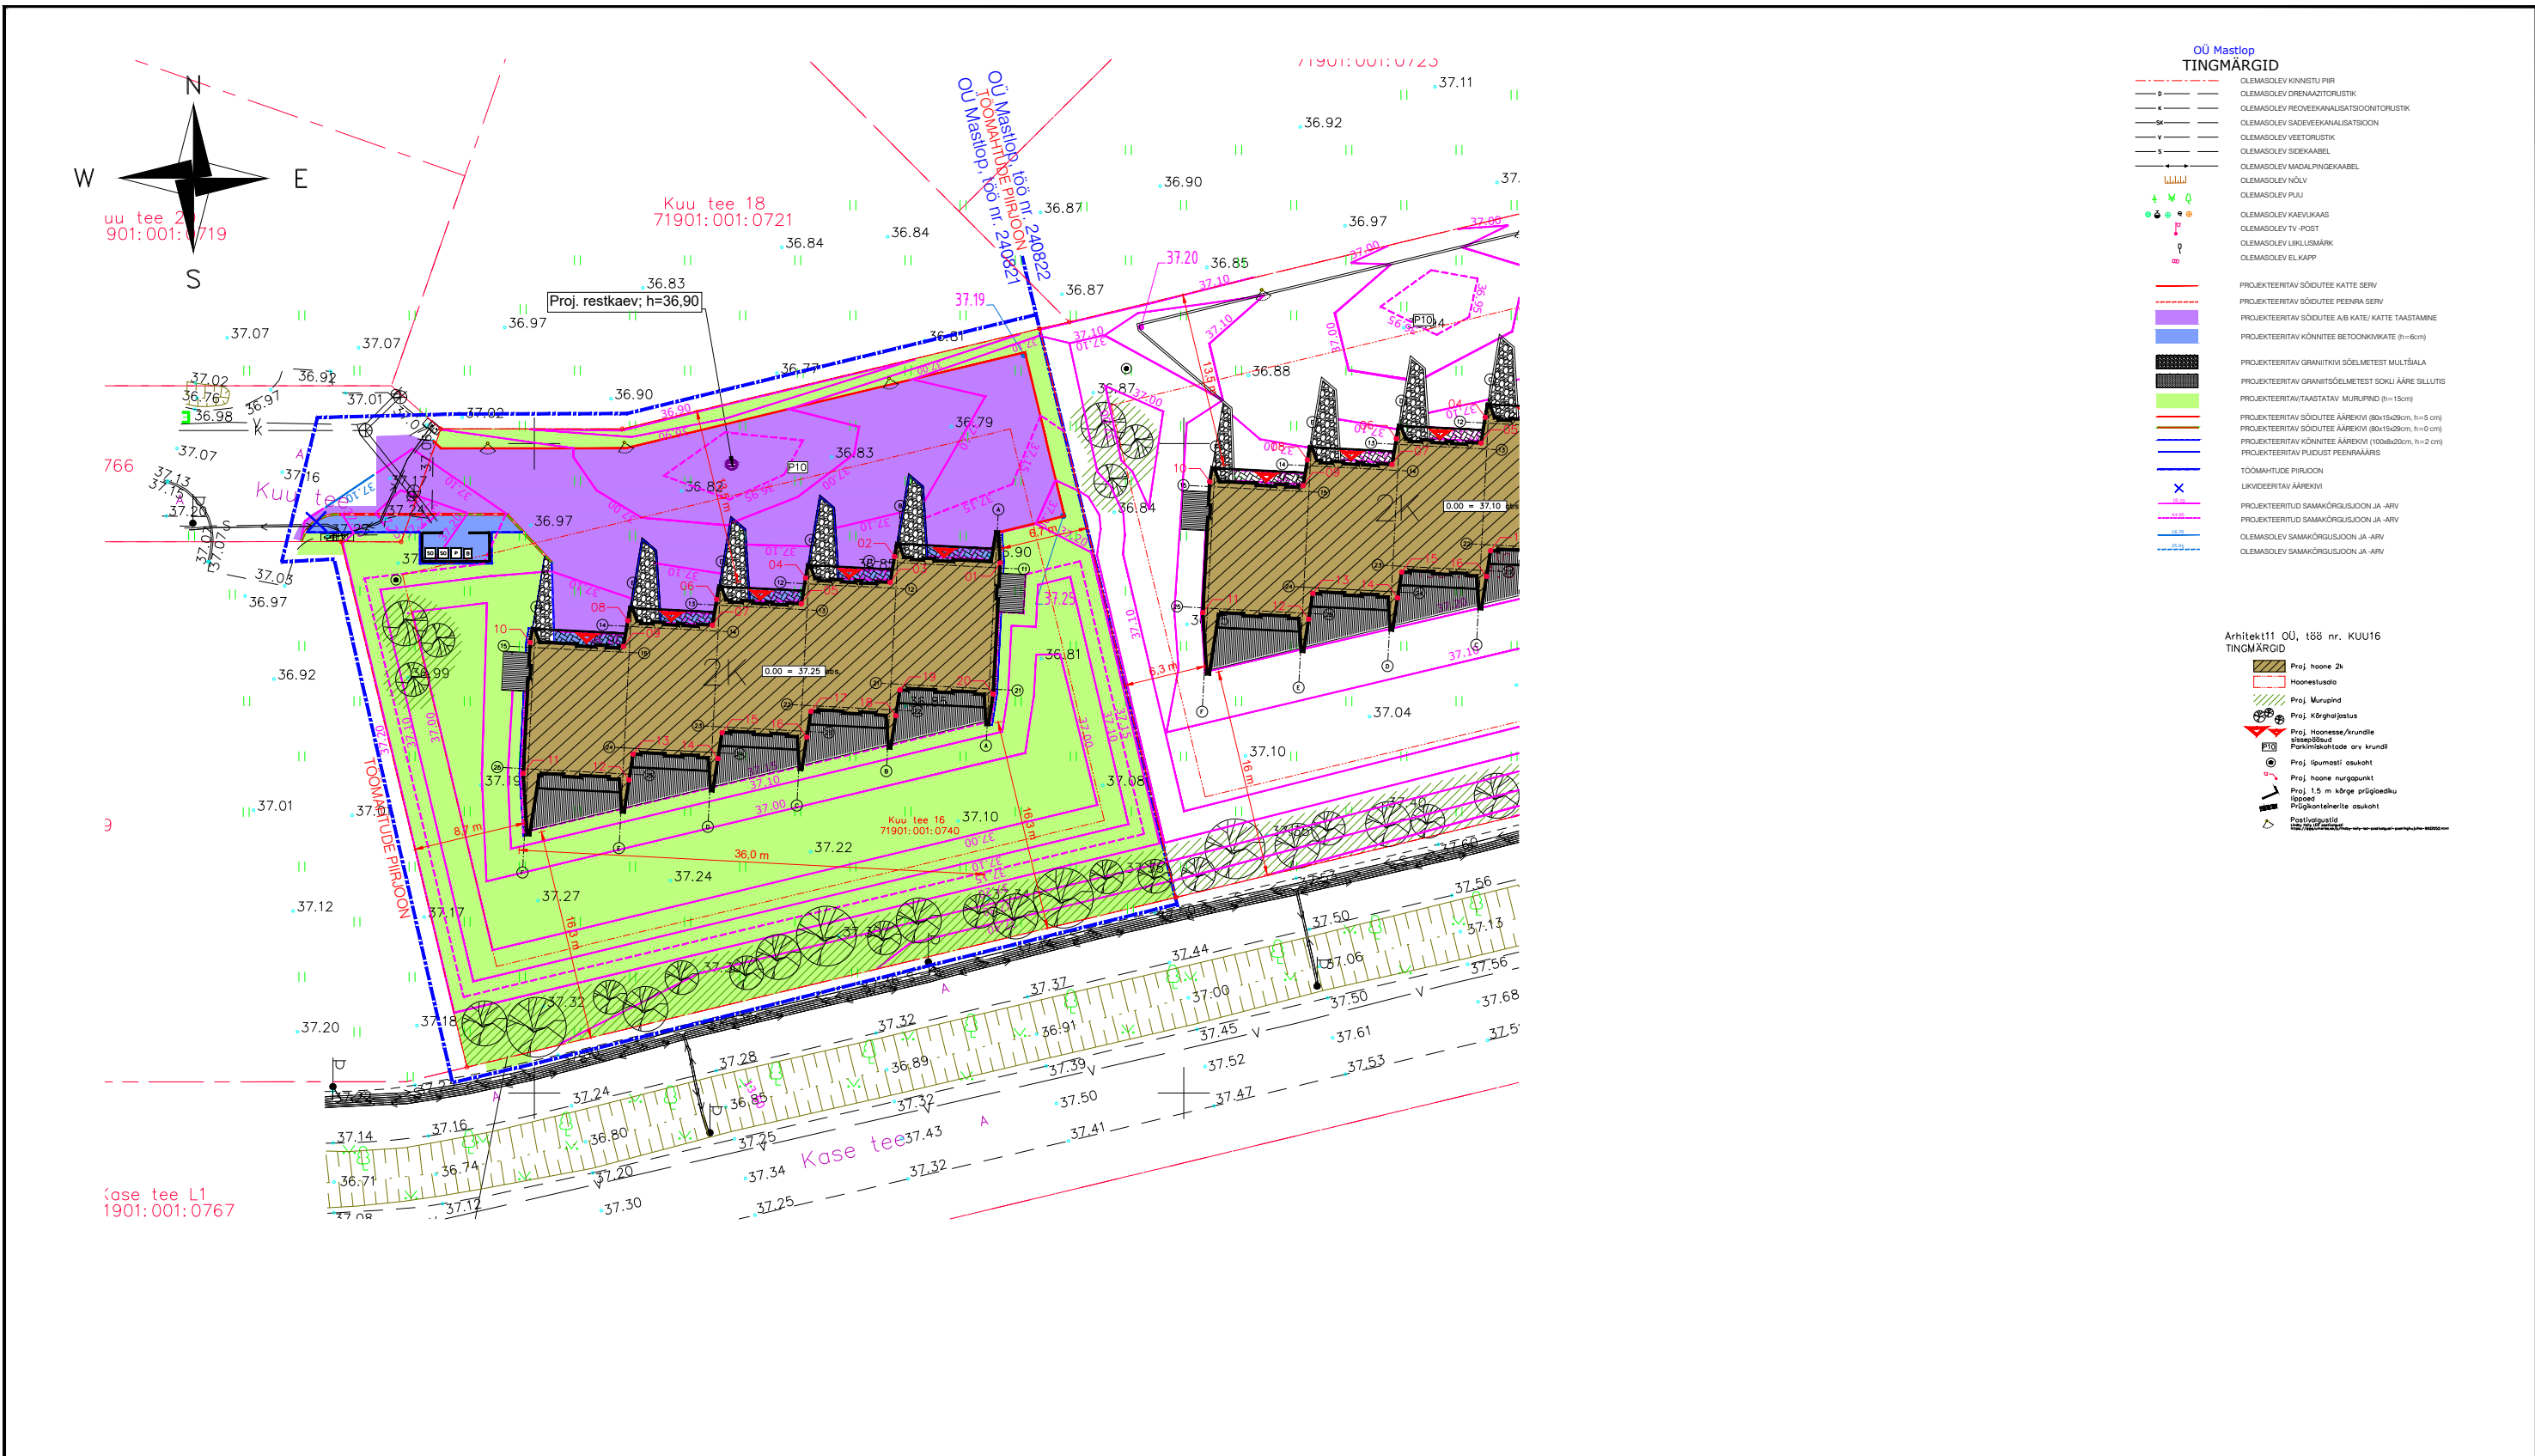

MÄRKUSED:

- 1) Geodeesia koostaja OÜ Radiaan. Teostatud 6.11.2024.a. Töö nr. 2578G24
- 2) Projekteeritud ja olemasolev katend tuleb omavahel kõrguslikult kokku viia
- 3) Kui ol.olevat katendit kahjustatakse suuremas ulatuses kui projektdokumentatsioonis kajastatud, tuleb see normidekohaselt taastada.

Mastlop OÜ Mastlop Reg.kood 12618952; EEP003122; ELK000079 Peterburi tee 2F, Tallinn 11415 tel. +372 56 24 26 34, e-mail ppoltsam@gmail.com		Projekti nimetus:		Töö nr:	
		KUU TEE 16 RIDAELAMU TEEDE-EHITUSLIK OSA		240821	
		Asukoht:		Leht nr:	
		KUU TEE 16/KUU TEE L4 SAKU ALEVIK, SAKU VALD, HARJU MK		TL-03	
		Tellija:		Stadium:	
Projektijuht		Pärt Põltsam		PÕHIPROJEKT	
Projekteeris		Pärt Põltsam		Mõõtkava:	
Kontrollis		Pärt Põltsam (tunnistuse nr. 163405/163406)		1:500	
Koostatud / trükitud:09.05.2025/ 19.05.2025		Joonise nimetus:			
		VERTIKAALPLANEERING			