


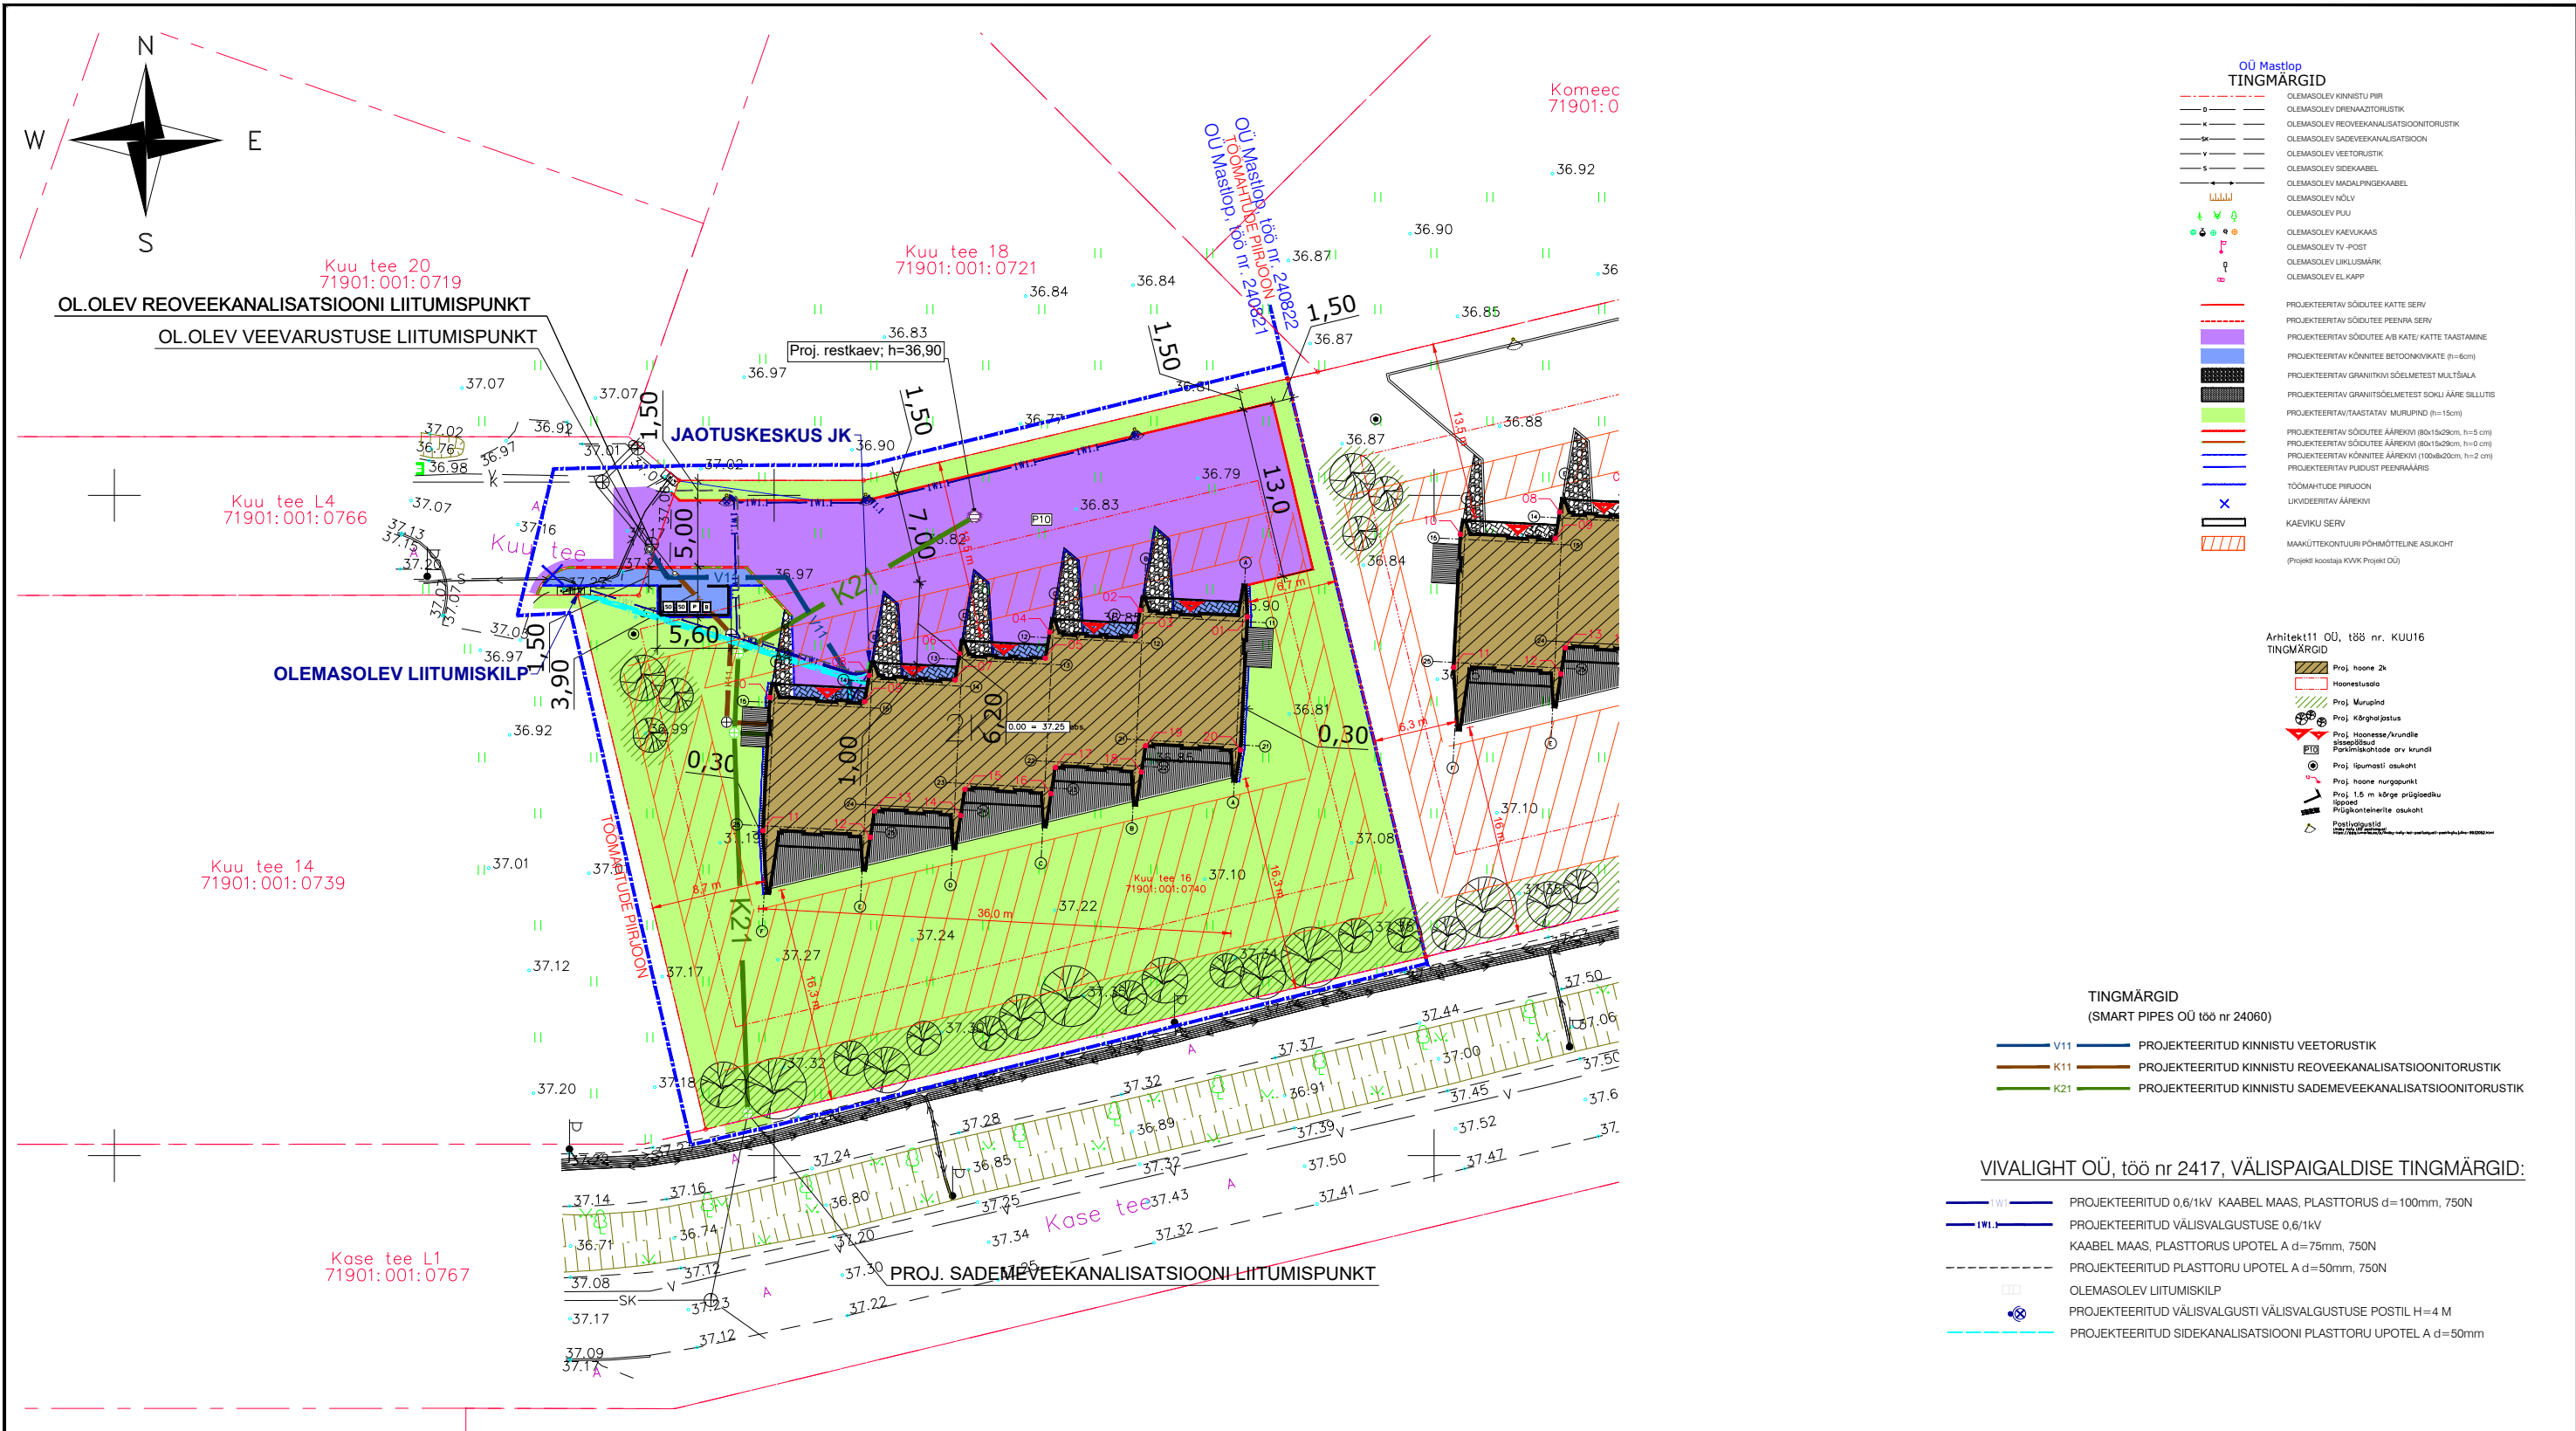

MÄRKUSED:

1) Geodeesia koostaja OÜ Radiaan. Teostatud 6.11.2024.a. Töö nr. 2578G24

2) Projekteeritud ja olemasolev katend tuleb omavahel kõrguslikult kokku viia

3) Kui ol.olevat katendit kahjustatakse suuremas ulatuses kui projektdokumentatsioonis kajastatud, tuleb see normidekohaselt taastada.

Mastlop OÜ Mastlop Reg.kood 12618952; EEP003122; ELK000079 Peterburi tee 2F, Tallinn 11415 tel. +372 56 24 26 34, e-mail ppoltsam@gmail.com		Projekti nimetus:	KUU TEE 16 RIDAELAMU TEEDE-EHITUSLIK OSA	Töö nr:	240821
		Asukoht:	KUU TEE 16/KUU TEE L4 SAKU ALEVIK, SAKU VALD, HARJU MK	Leht nr:	TL-04
				Staadium:	PÕHIPROJEKT
				Mõõtkava:	1:500
		Projektijuht	Pärt Põltsam	Tellija:	Saku Arendus OÜ
Projekteeris	Pärt Põltsam				
Kontrollis	Pärt Põltsam (tunnistuse nr. 163405/163406)	Koostatud / trükitud:09.05.2025/ 19.05.2025			