




Armatuurvarraste painutustabel

Kuju	Positsioon	D(mm)	Materjal	Pikkus (mm)	a	b	c	d	e	u	v	x	y	TD	Kogus [tk]	Pikkus kokku [m]	Mass kokku [kg]
B	84	12	B500B	840	720	150				90°					48	4	3.4
D	86	12	B500B	1105	215	730	215								48	5	5.5
D	87	12	B500B	1075	201	730	201								48	4	4.3
U	85	6	B500B	1165	80	270	270								24	8	9.3
																Kokku:	22.5
																	13.8


Armatuuri mõõdud on antud väliskülgedele
Armatuurvarda kogupikkus ei sisalda pikkuse muutust painutamisel

Armatuurvarraste kokkuvõte



Materjal	Läbimõõt D [mm]	Pikkus kokku [m]	Mass kokku [kg]
B500B	6	9.3	2.1
B500B	12	13.2	11.7
Kokku:			13.8

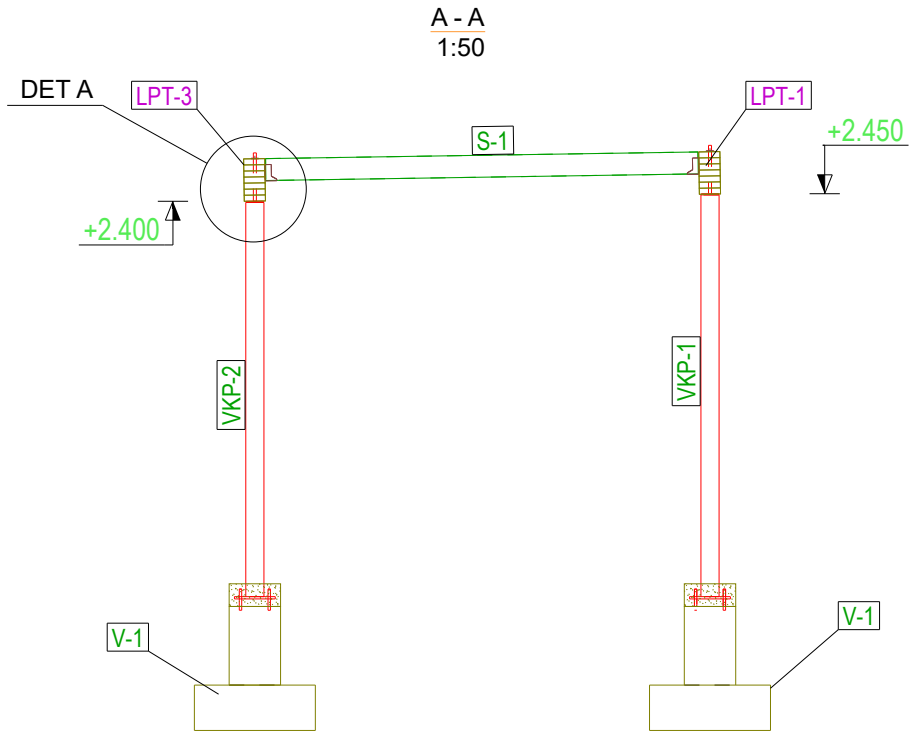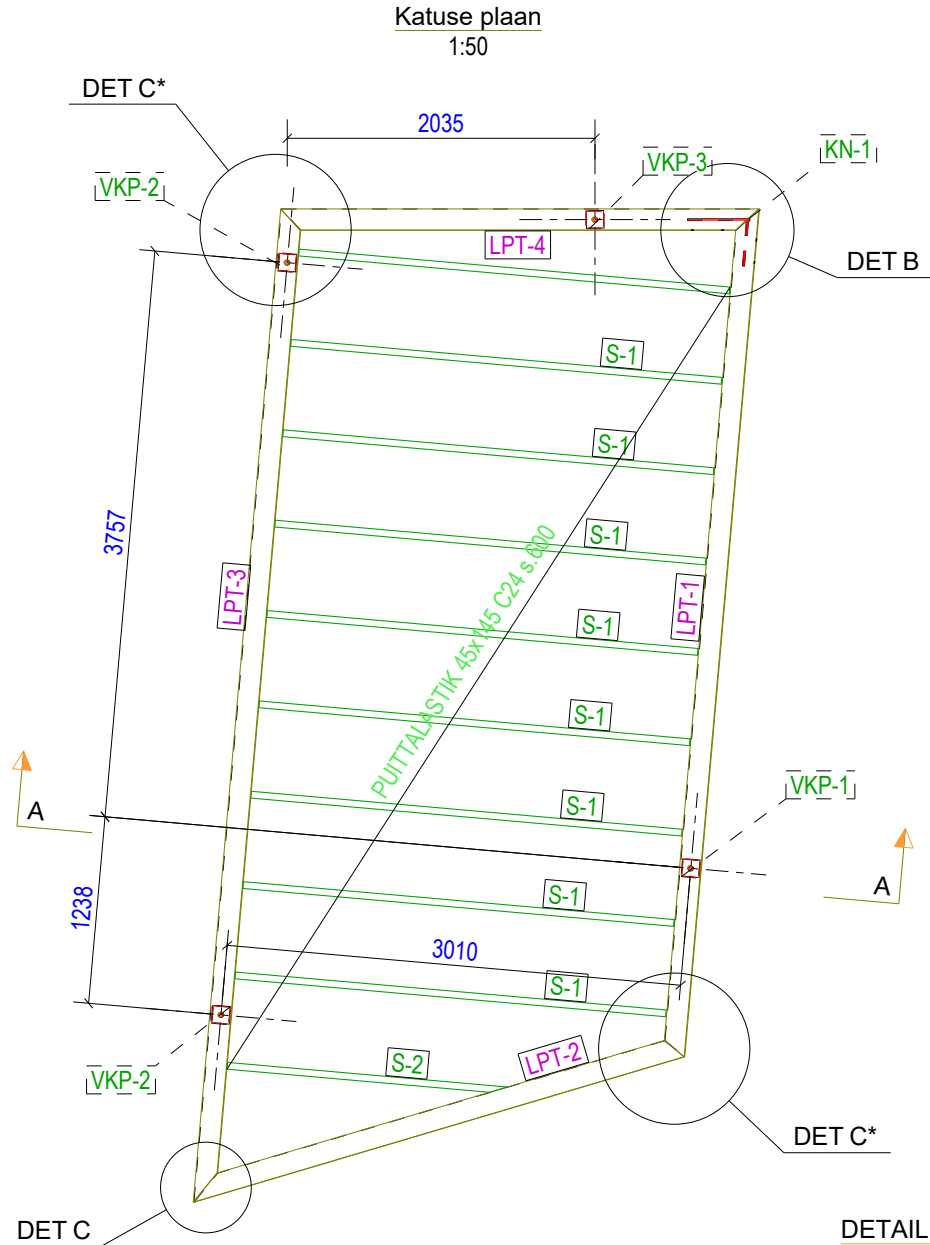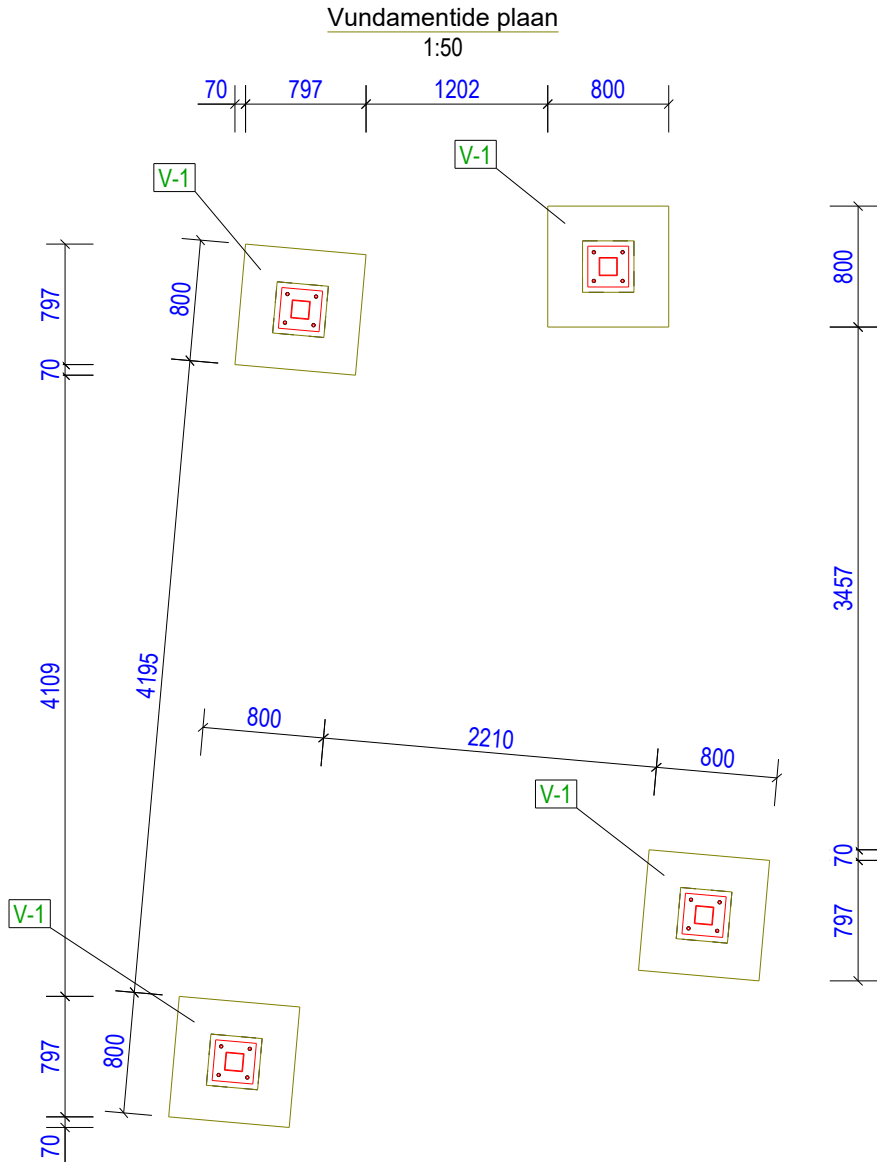

DETAIL B
1:20

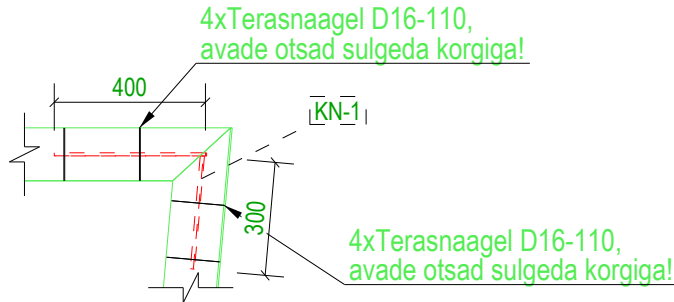

DETAIL C
1:20

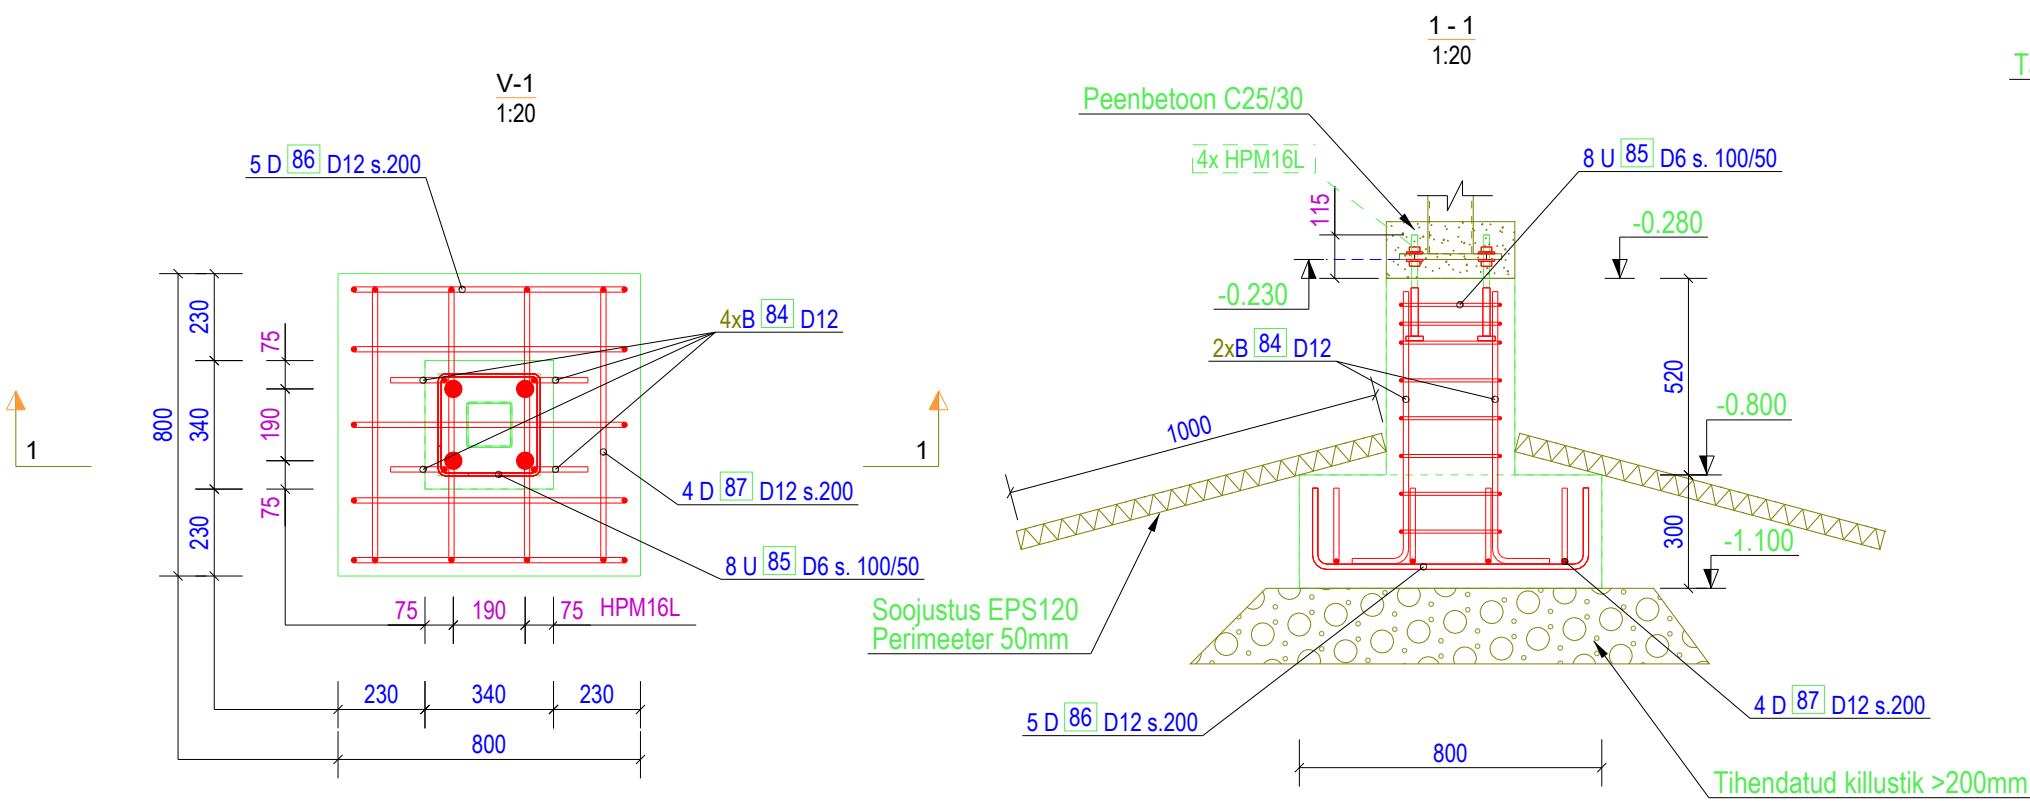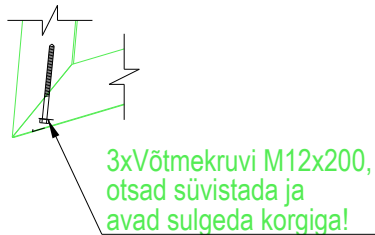

MÄRKUSED:

- VUNDAMEDID VALADA BETOONIST C25/30, ARMATUUR B500B
- VUNDAMENDI R/B-KONSTRUKTSIOONIDE KESKKONNAKLASS XC2, XF1
- ARMATUURI MIN KAITSEKIHT TALLA ALL 40mm+10mm = 50mm (MINIMAALNE + TOLERANTS = NOMINAALNE), MUIDU 25mm+10mm = 35mm
- KONSTRUKTSIOONI VALMISTAMISE TOLERANTSID VASTAVALT BY39 NÕUETELE
- JOONISEL ANTUD ARMATUURI PAINUTUSMÕDUD ON VÄLIMISED
- TÄITEMATERJALI TERA SUURIM LÄBIMÕÖT 16 mm
- KUI VUNDAMENDI ALUMINE PIND ON EBATASANE TULEB ALUMISE PINNA KAITSEKIHTI (EHK TALDMIKU PAKSUSTI) SUURENDADA EBATASASUSE VÕRRA (MIN KAITSEKIHT EBATASASE ALUSE KORRAL 75mm; LUBATUD HÄLVE -10mm; TALDMIKU RISTLÕIKE KASUKÕRGUST EI TOHI VÄHENDADA!)
- KÕRGUSMÄRGID ON ANTUD SUHTELISTE KÕRGUSMÄRKIDENA
- KÕIK KINNITUSVAHENDID KUUMTSINGITUD
- POLDIAUGUD KÕIK ETTE PUURIDA!

OBJEKTI NIMI:	Ridaelamud	KUUPÄEV	16.07.2025
ADDRESS:	Komeedi tn. 1, 2 ja Kuu tee 16, Saku, 75501 Harju mk		
PROJEKT:	O.Paavo	JOONISE SISU:	MÕÕTKAVA 1:20 1:50
KONTROLLIS:		Auto varjualune	
J&O PROJEKT tel.53285342, reg.koode--12615712	PROJ.STAADIUM:	RP	JOON.NR. EK-7-001
	TÖÖ NR.	202410	