



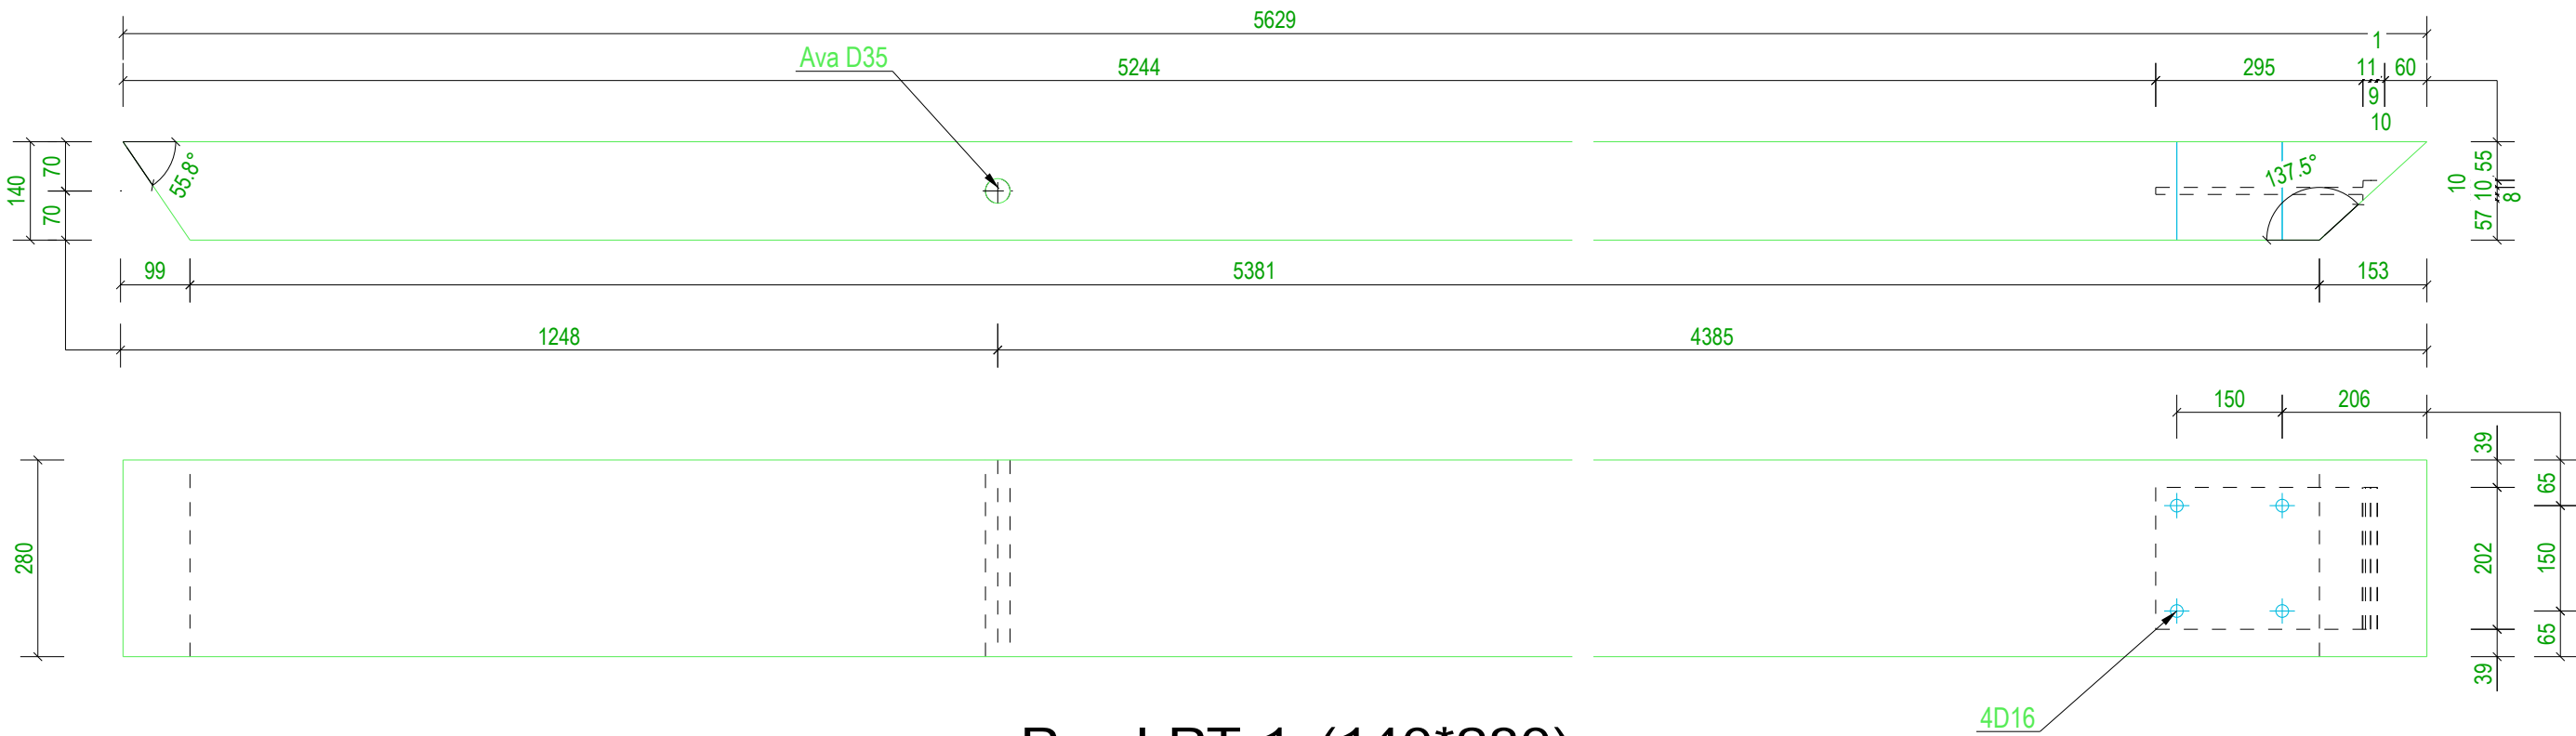


Pos.LPT-1 (140*280)

Arv:1tk

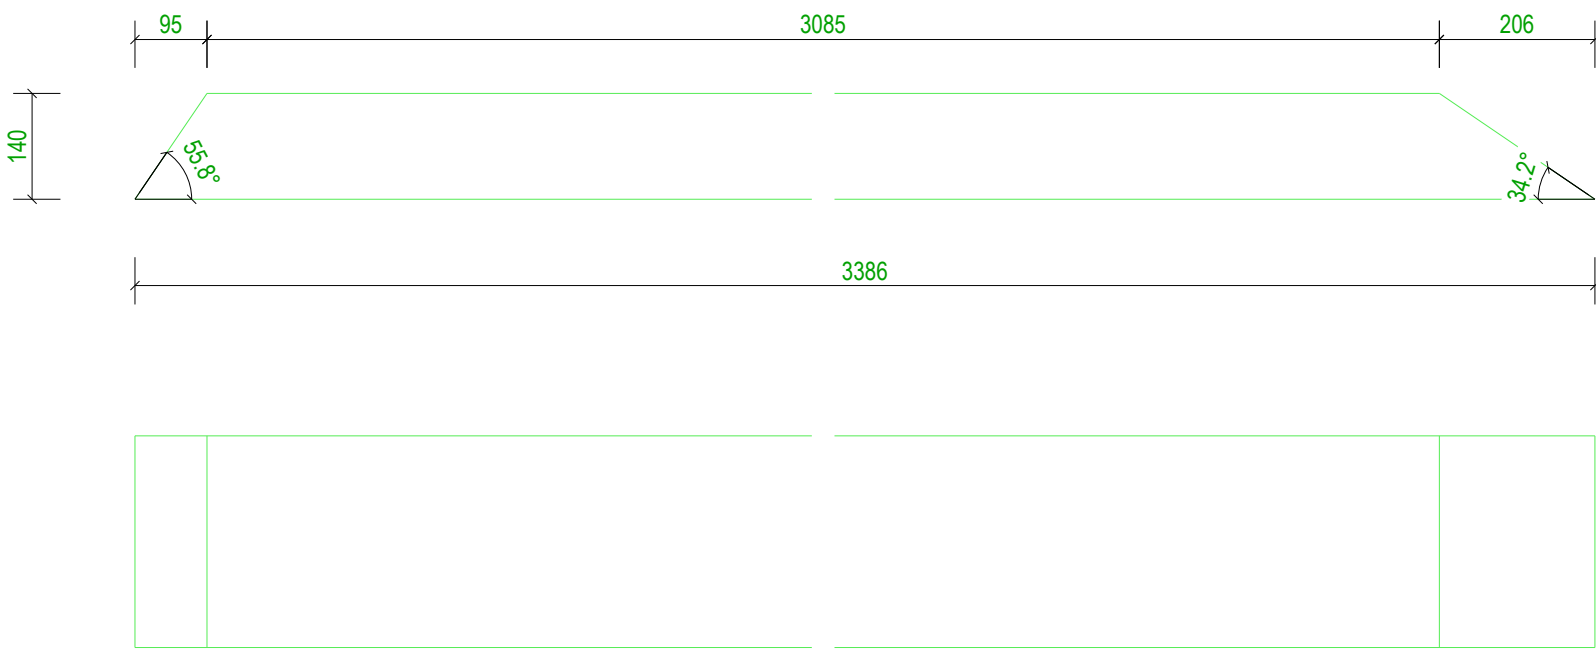


Pos.LPT-2 (140*280)

Arv:1tk

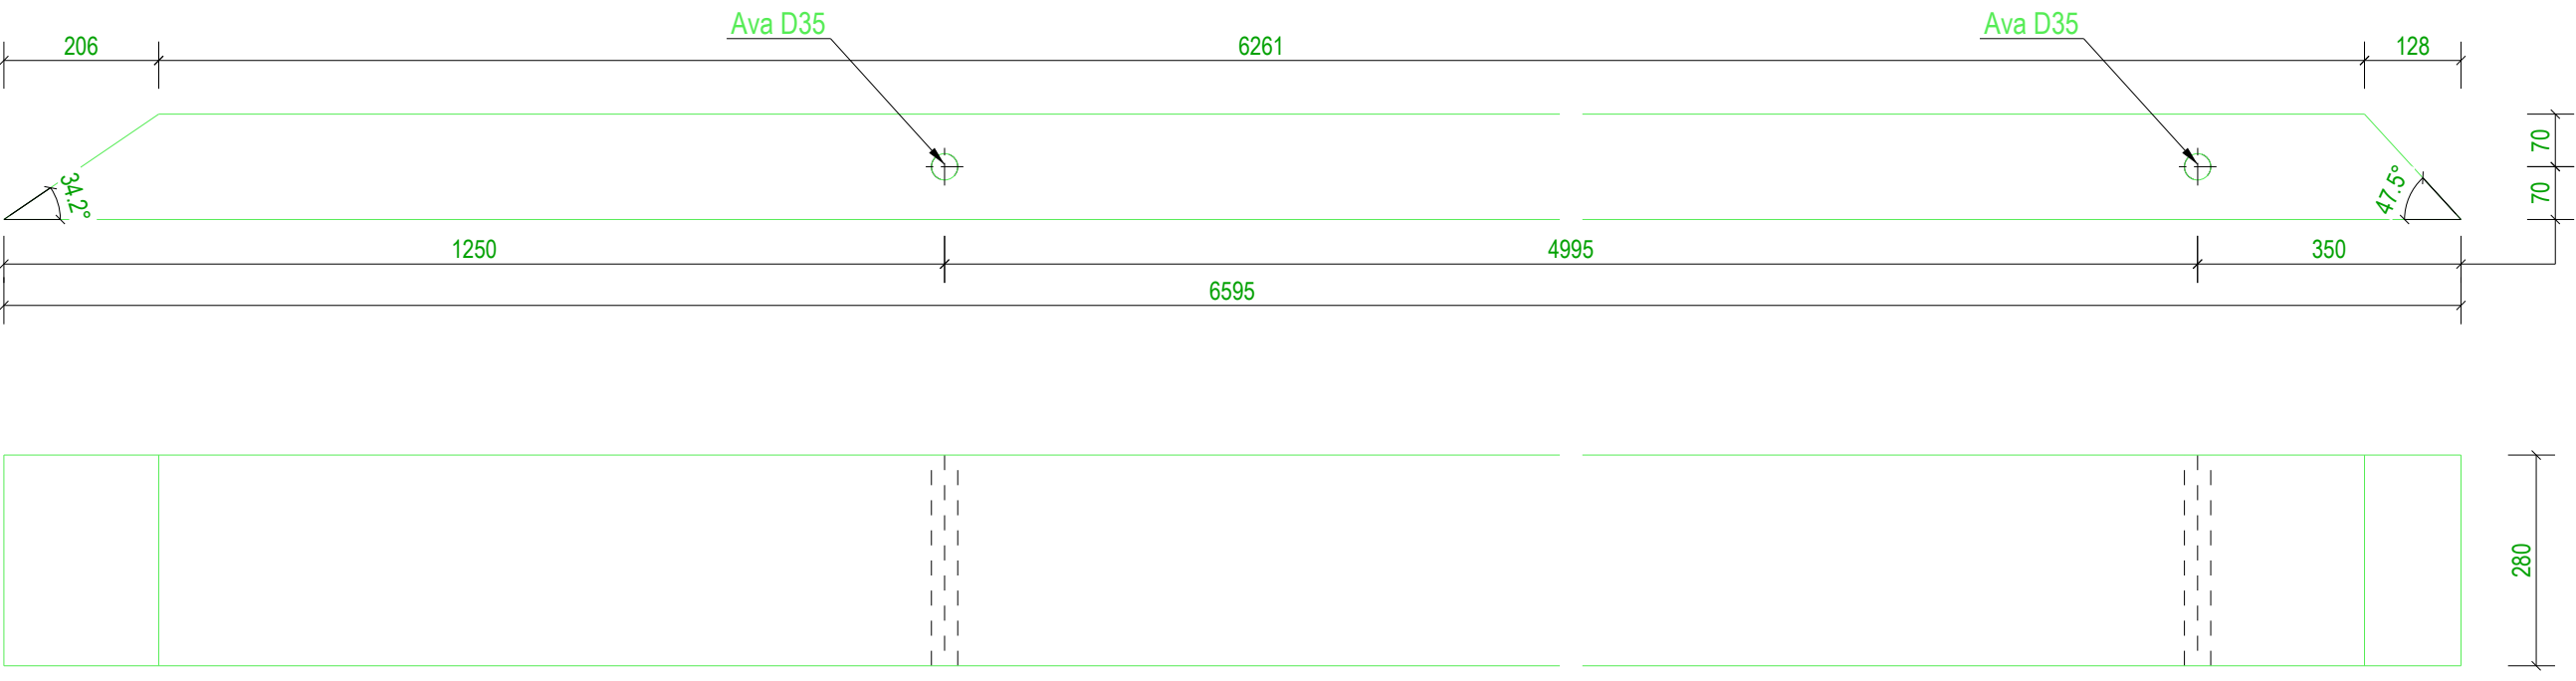

Pos.LPT-3 (140*280)

Arv:1tk

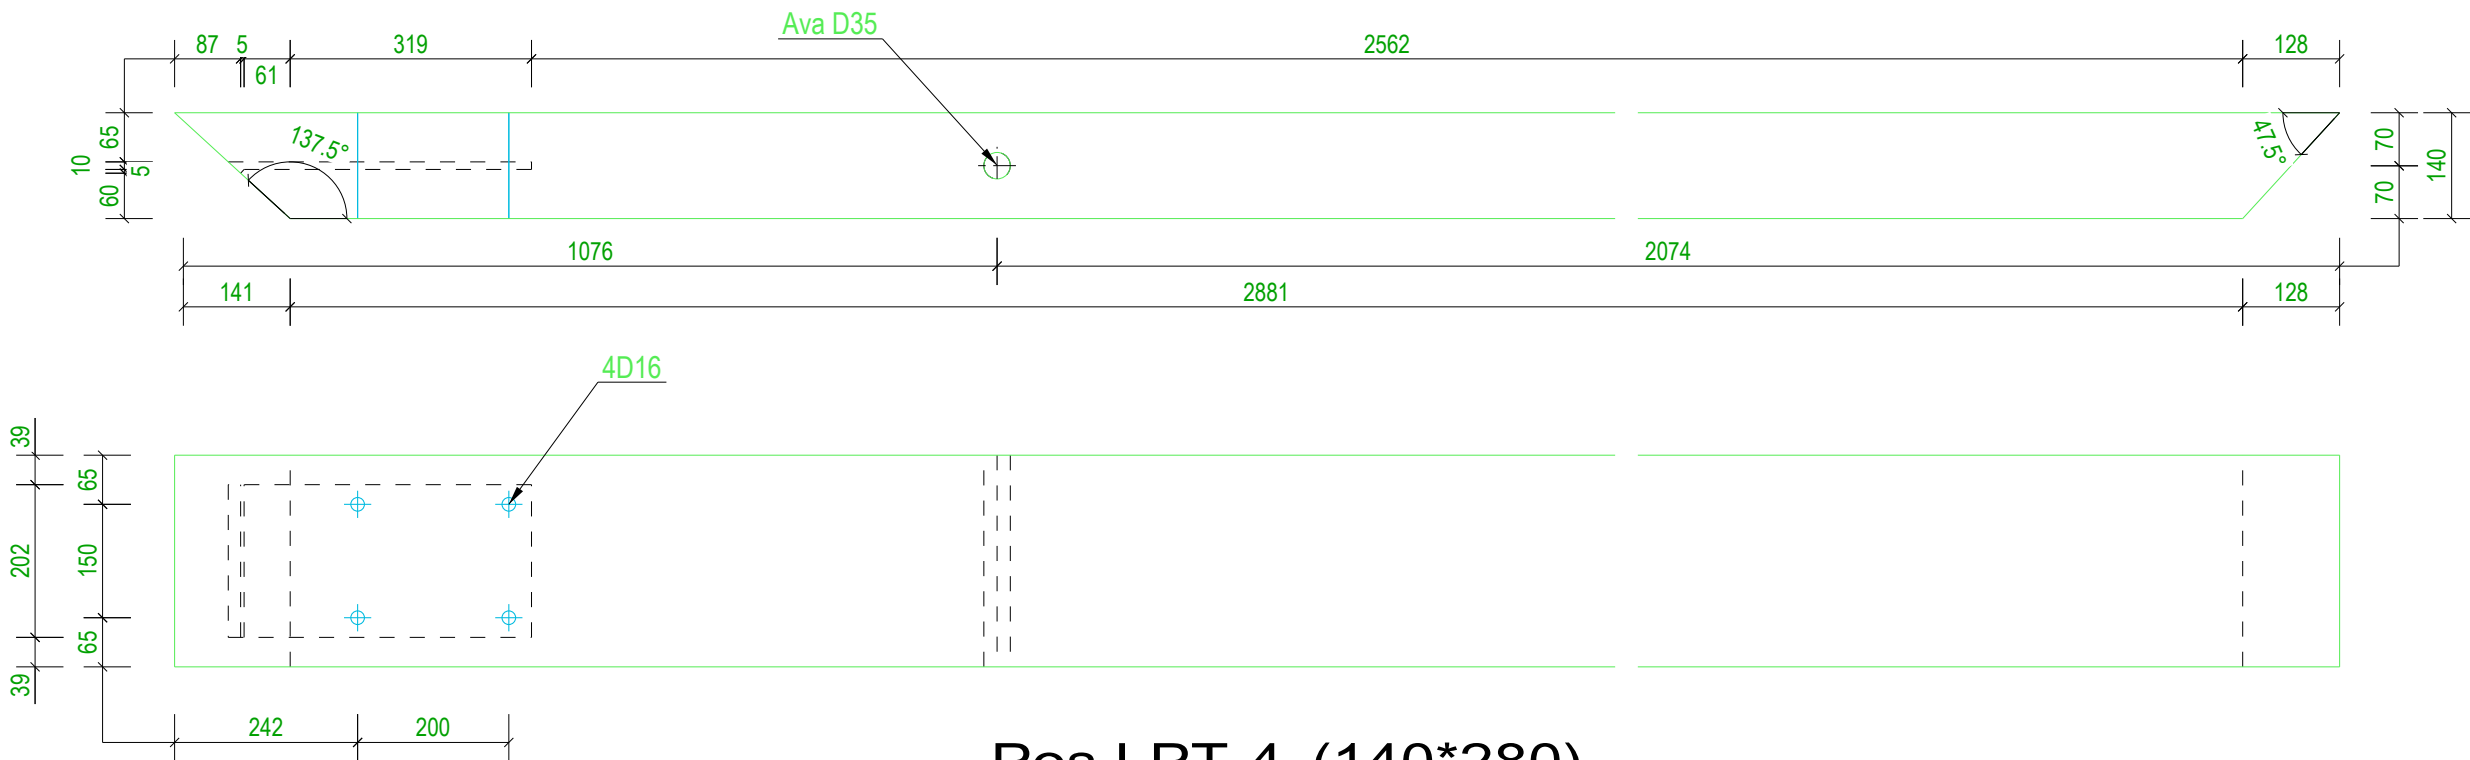

Pos.LPT-4 (140*280)

Arv:1tk

PUIDU SPETSIFIKATSIOON						
Tähis	Materjal	Kogus, tk	Gabariidid, mm			Märkus
			B	H	L	
LPT LPT-1	GL28	1	140	280	5629	
LPT LPT-2	GL28	1	140	280	3386	
LPT LPT-3	GL28	1	140	280	6595	
LPT LPT-4	GL28	1	140	280	3162	

OBJEKTI NIMI: Ridaelamud			KUUPÄEV: 16.07.2025		
AADRESS: Komeedi tn. 1, 2 ja Kuu tee 16, Saku, 75501 Harju mk					
PROJEKT: O.Paavo		JOONISE SISU: Varikatuse liimpuittalade kujudjoonised		MÕÕTKAVA: 1:10	
KONTROLLIS:		PROJ.STAADIUM: TP		TÖÖ NR. 2024.10	
J&O PROJEKT				JOON.NR. EK-7-011	