


ELEMENDI VKP-2 SPETSIFIKATSIOON, MIDA VALMISTATAKSE 2 TK						
POS.	PROFIIL	KLASS	PIKKUS [mm]	PINDALA [m2]	KAAL [kg]	ARV
1002	PL8*114	S235JR	114	0.0	0.8	1
1015	PL15*270	S355J2	270	0.2	8.6	1
KEERMEV***	D20	8.8	320	0.0	0.7	1
P-32	SHS120*4	S355J2	2607	1.3	38.0	1
			KOKKU:	1.5	48.1	

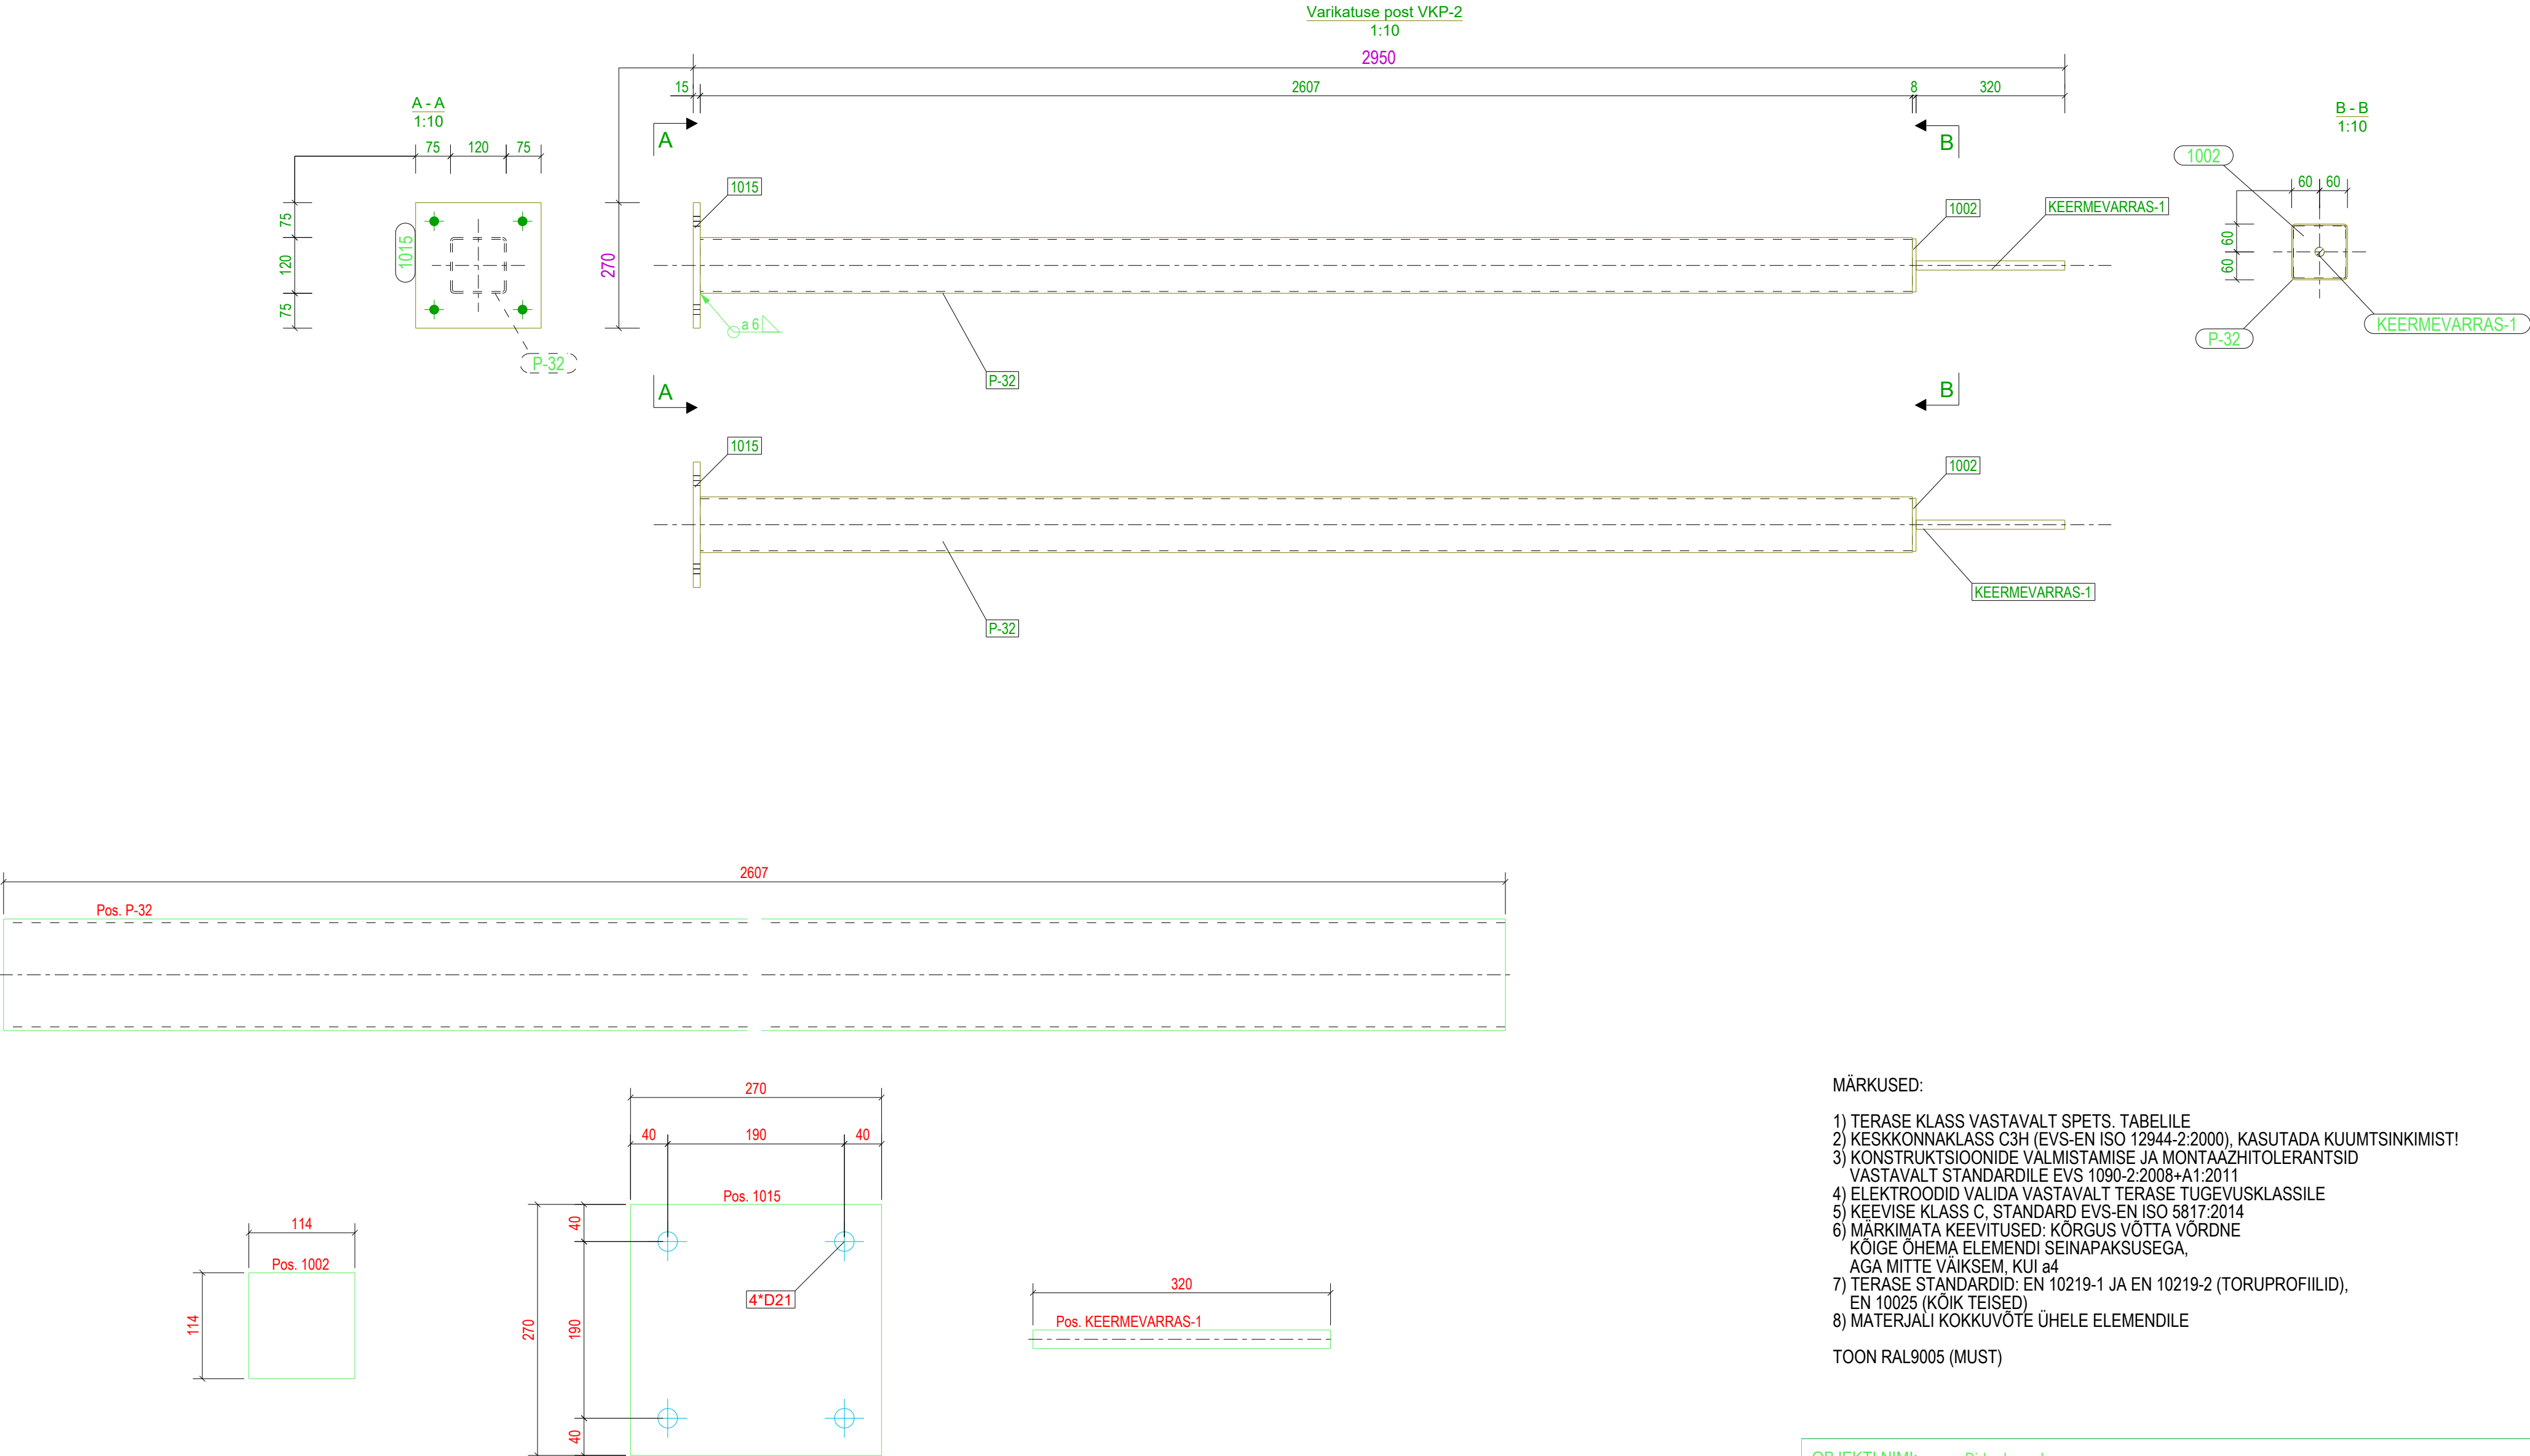

- MÄRKUSED:
- 1) TERASE KLASS VASTAVALT SPETS. TABELILE
 - 2) KESKKONNAKLASS C3H (EVS-EN ISO 12944-2:2000), KASUTADA KUUMTSINKIMIST!
 - 3) KONSTRUKTSIOONIDE VALMISTAMISE JA MONTAAZHITOLERANTSID VASTAVALT STANDARDILE EVS 1090-2:2008+A1:2011
 - 4) ELEKTROODID VALIDA VASTAVALT TERASE TUGEVUSKLASSILE
 - 5) KEEVISE KLASS C, STANDARD EVS-EN ISO 5817:2014
 - 6) MÄRKIMATA KEEVITUSED: KÕRGUS VÕTTA VÕRDNE KÕIGE ÕHEMA ELEMENDI SEINAPAKSUSEGA, AGA MITTE VÄIKSEM, KUI a4
 - 7) TERASE STANDARDID: EN 10219-1 JA EN 10219-2 (TORUPROFIILID), EN 10025 (KÕIK TEISED)
 - 8) MATERJALI KOKKUVÕTE ÜHELE ELEMENDILE
- TOON RAL9005 (MUST)

OBJEKTI NIMI: Ridaelamud			KUUPÄEV: 16.07.2025	
AADRESS: Komeedi tn. 1, 2 ja Kuu tee 16, Saku, 75501 Harju mk				
PROJEKT: O.Paavo		JOONISE SISU: Varikatuse post VKP-2		MÕÕTKAVA: 1:5, 1:10
KONTROLLIS:		PROJ.STAADIUM: TP		JOON.NR. EK-9-102
1 & O PROJEKT		TÖÖ NR. 2024.10		