



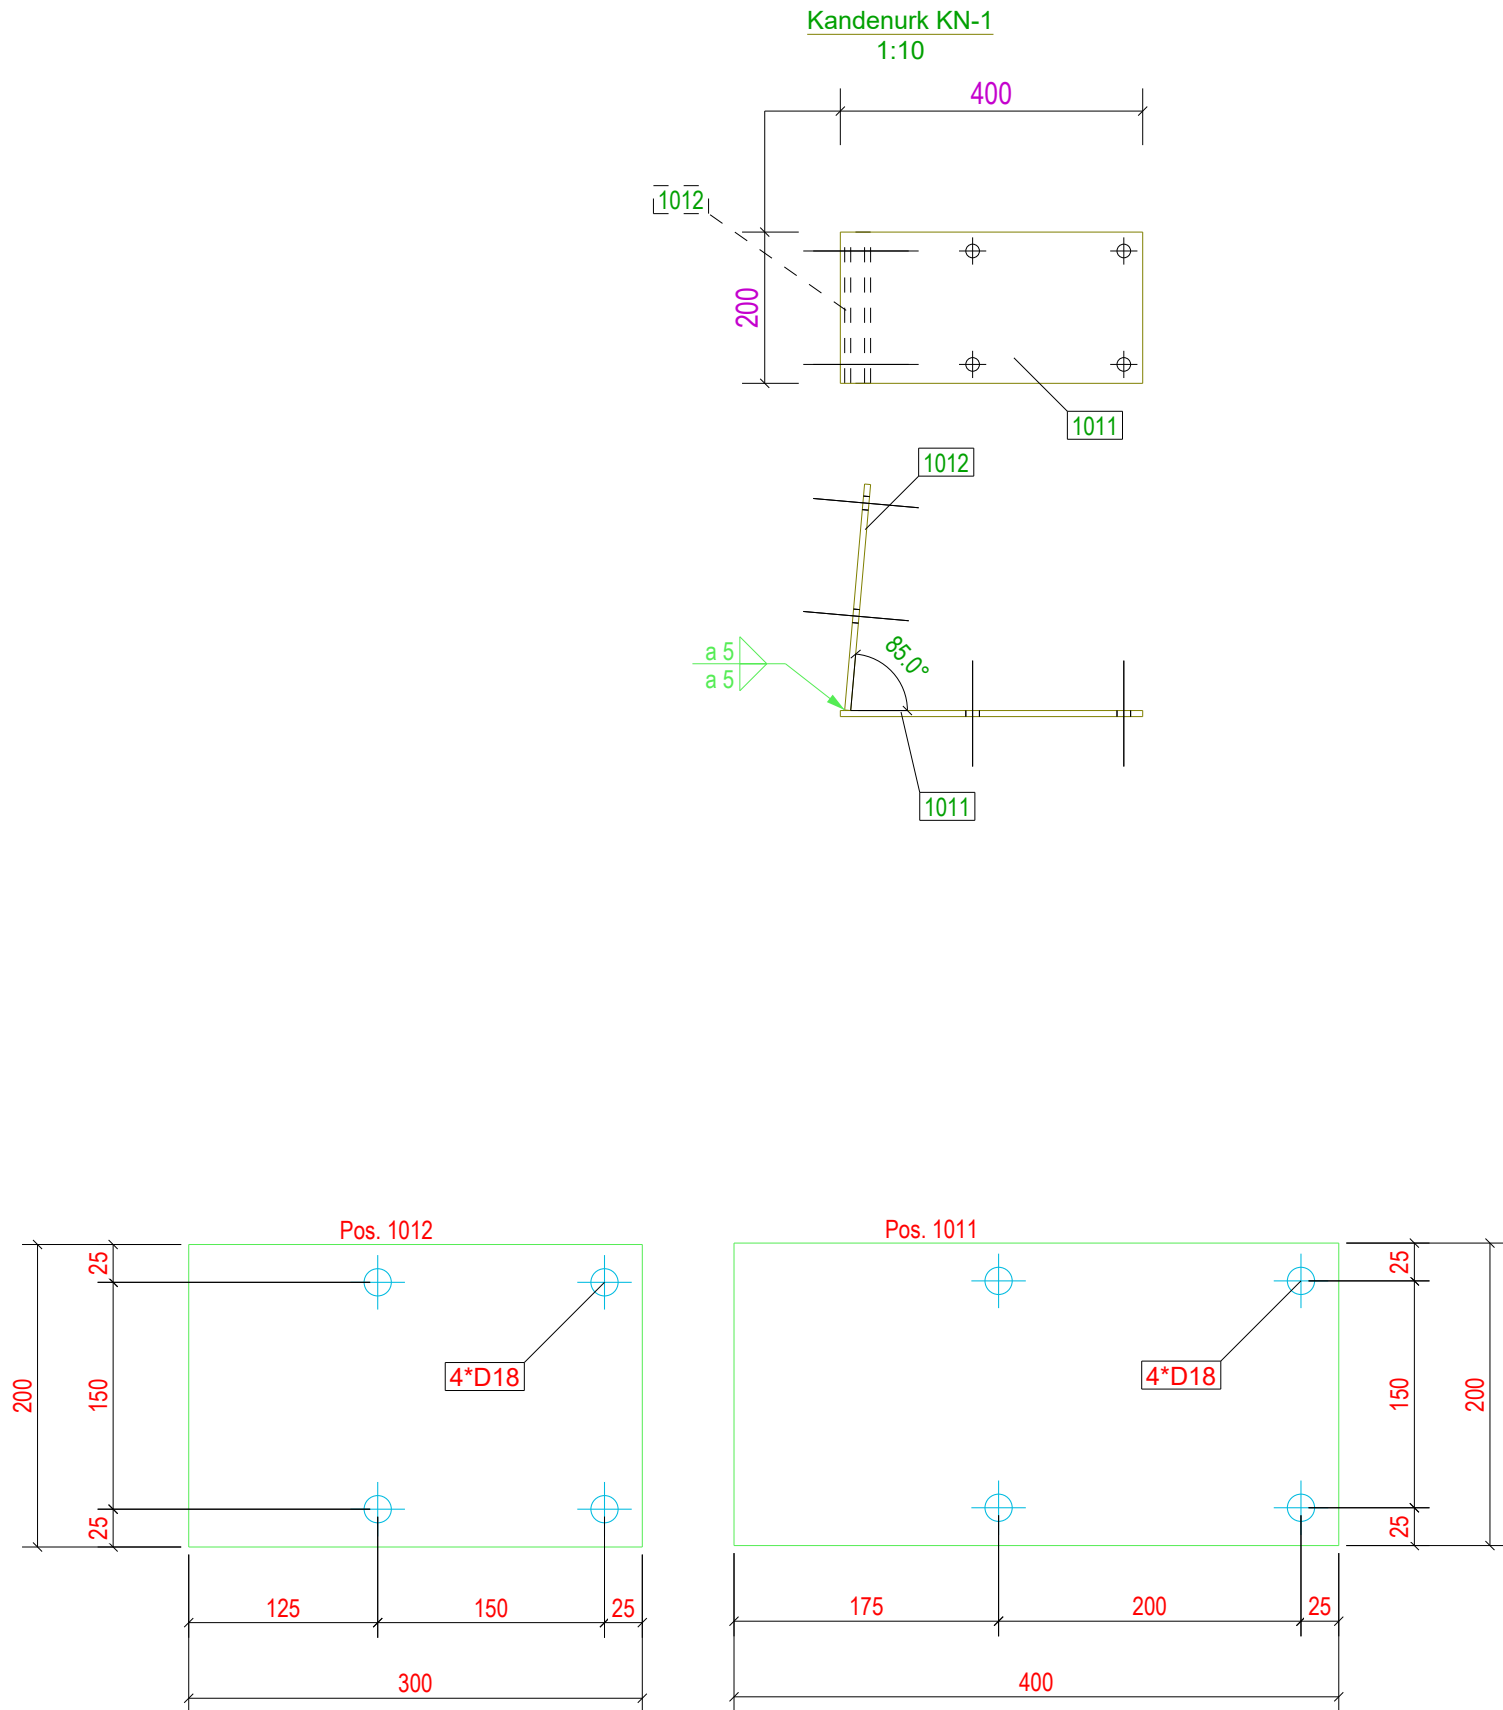

ELEMENDI KN-1 SPETSIFIKATSIOON, MIDA VALMISTATAKSE 1 TK

POS.	PROFIIL	KLASS	PIKKUS [mm]	PINDALA [m2]	KAAL [kg]	ARV
1011	PL8*200	S355J2	400	0.2	5.0	1
1012	PL8*200	S355J2	300	0.1	3.8	1
			KOKKU:	0.3	8.8	

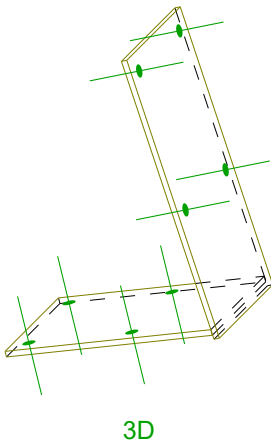

MÄRKUSED:

- 1) TERASE KLASS VASTAVALT SPETS. TABELILE
- 2) KESKKONNAKLASS C3 (EVS-EN ISO 12944-2:2000), KASUTADA KUUMTSINKIMIST!
- 3) KONSTRUKTSIOONIDE VALMISTAMISE JA MONTAAZHITOLERANTSID VASTAVALT STANDARDILE EVS 1090-2:2008+A1:2011
- 4) ELEKTROODID VALIDA VASTAVALT TERASE TUGEVUSKLASSILE
- 5) KEEVISE KLASS C, STANDARD EVS-EN ISO 5817:2014
- 6) MÄRKIMATA KEEVITUSED: KÕRGUS VÕTTA VÕRDNE KÕIGE ÕHEMA ELEMENDI SEINAPAKSUSEGA, AGA MITTE VÄIKSEM, KUI a4
- 7) TERASE STANDARDID: EN 10219-1 JA EN 10219-2 (TORUPROFIILID), EN 10025 (KÕIK TEISED)
- 8) MATERJALI KOKKUVÕTE ÜHELE ELEMENDILE

OBJEKTI NIMI: Ridaelamud		KUUPÄEV: 16.07.2025	
ADDRESS: Komeedi tn. 1, 2 ja Kuu tee 16, Saku, 75501 Harju mk			
PROJEKT: O.Paavo	JOONISE SISU: Kandenurk KN-1		MÕÕTKAVA: 1:5 1:10
KONTROLLIS:	PROJ.STAADIUM: TP	TÖÖ NR. 2024.10	JOON.NR. EK-9-111