


Sokli plaan
1:75

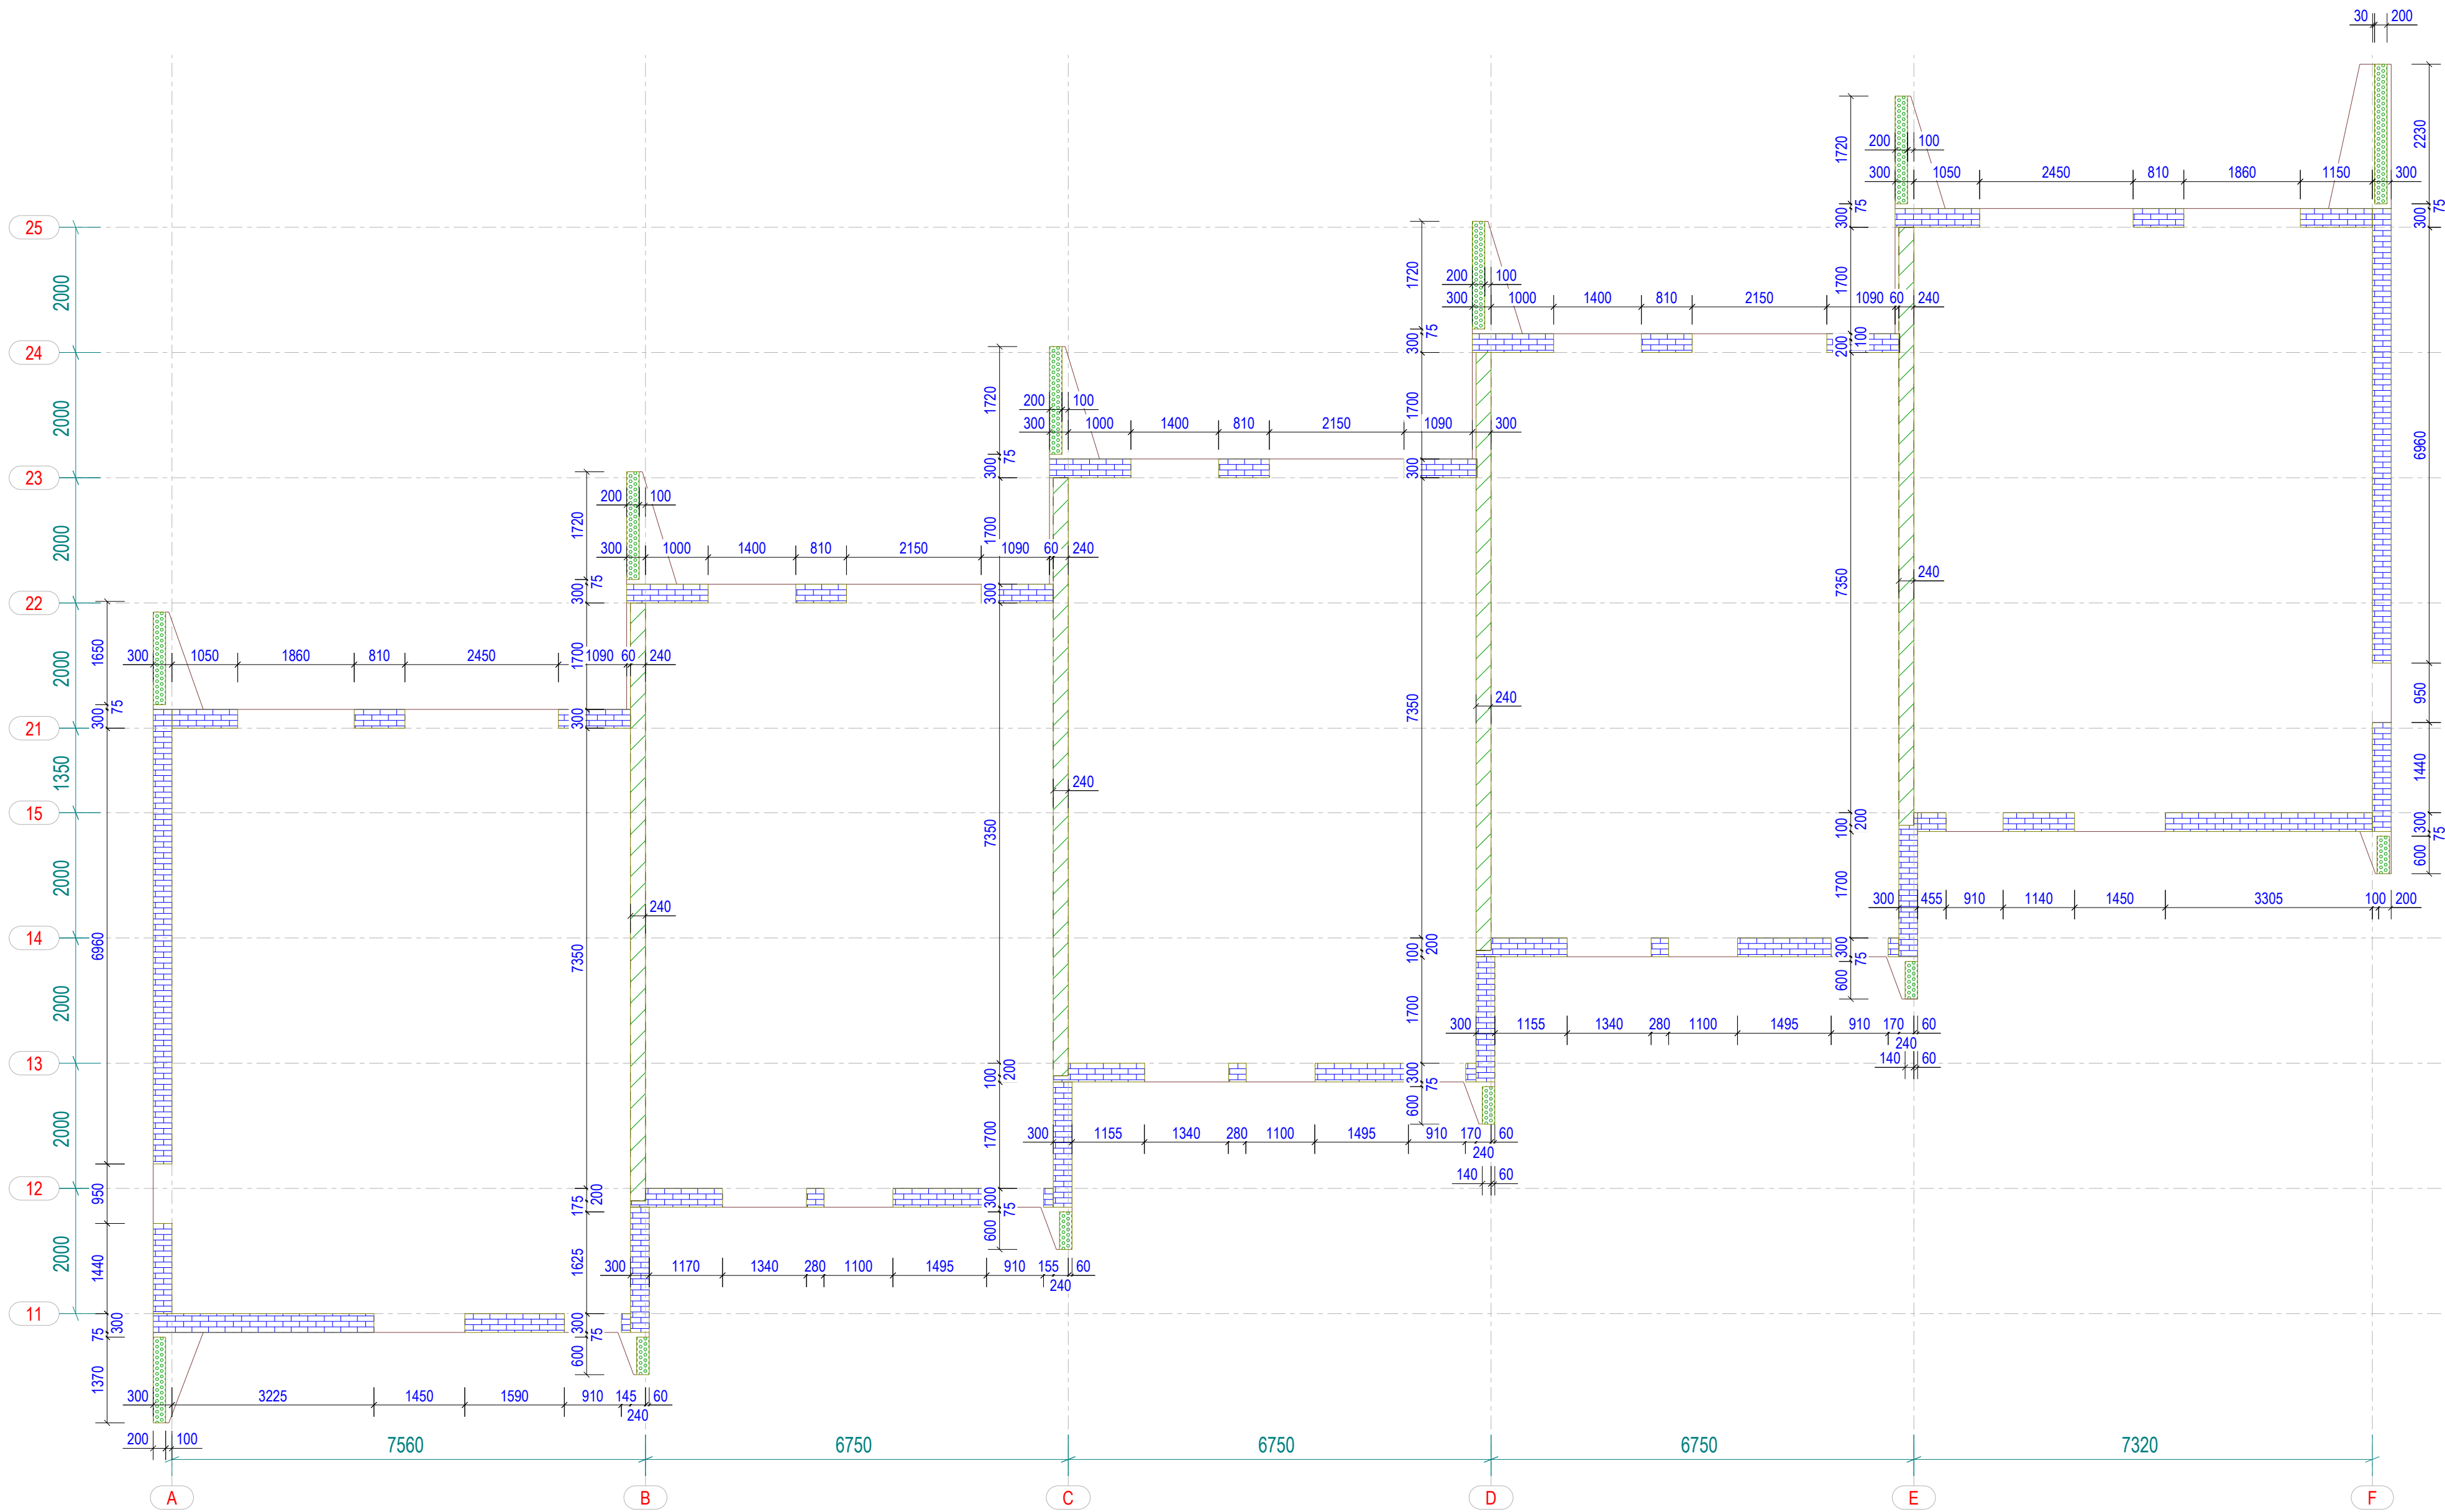

TINGMÄRGID:

- FIBO 5 200mm
- FIBO 5 300mm
- "COLUMBIA"-KIVI 240mm

OBJEKTI NIMI: Ridaelamud		KUUPÄEV: 26.03.2025	
AADRESS: Komeedi tn. 1, 2 ja Kuu tee 16, Saku, 75501 Harju mk		MÕÕTKAVA: 1:75	
PROJEKT: O.Paavo	JOONISE SISU: Sokli plaan		JOON.NR.: EK-2-101
KONTROLLIS:	PROJ.STAADIUM: TP	TÖÖ NR.: 202410	

