


BETOONKONSTRUKTSIOONIDE SPETSIFIKATSIOON						
TÄHIS	ARV	BETOON	KOGUS [m³]	KAAL [t]	KOKKU [m³]	JOONIS
BAUROC 1600x375x200	7					
BAUROC 2000x375x200	5					
BAUROC 2400x375x200	5					
BAUROC 3000x375x200	5					
KOKKU	22				0.0	

1.Korruse kandeseinte plaan
1:50

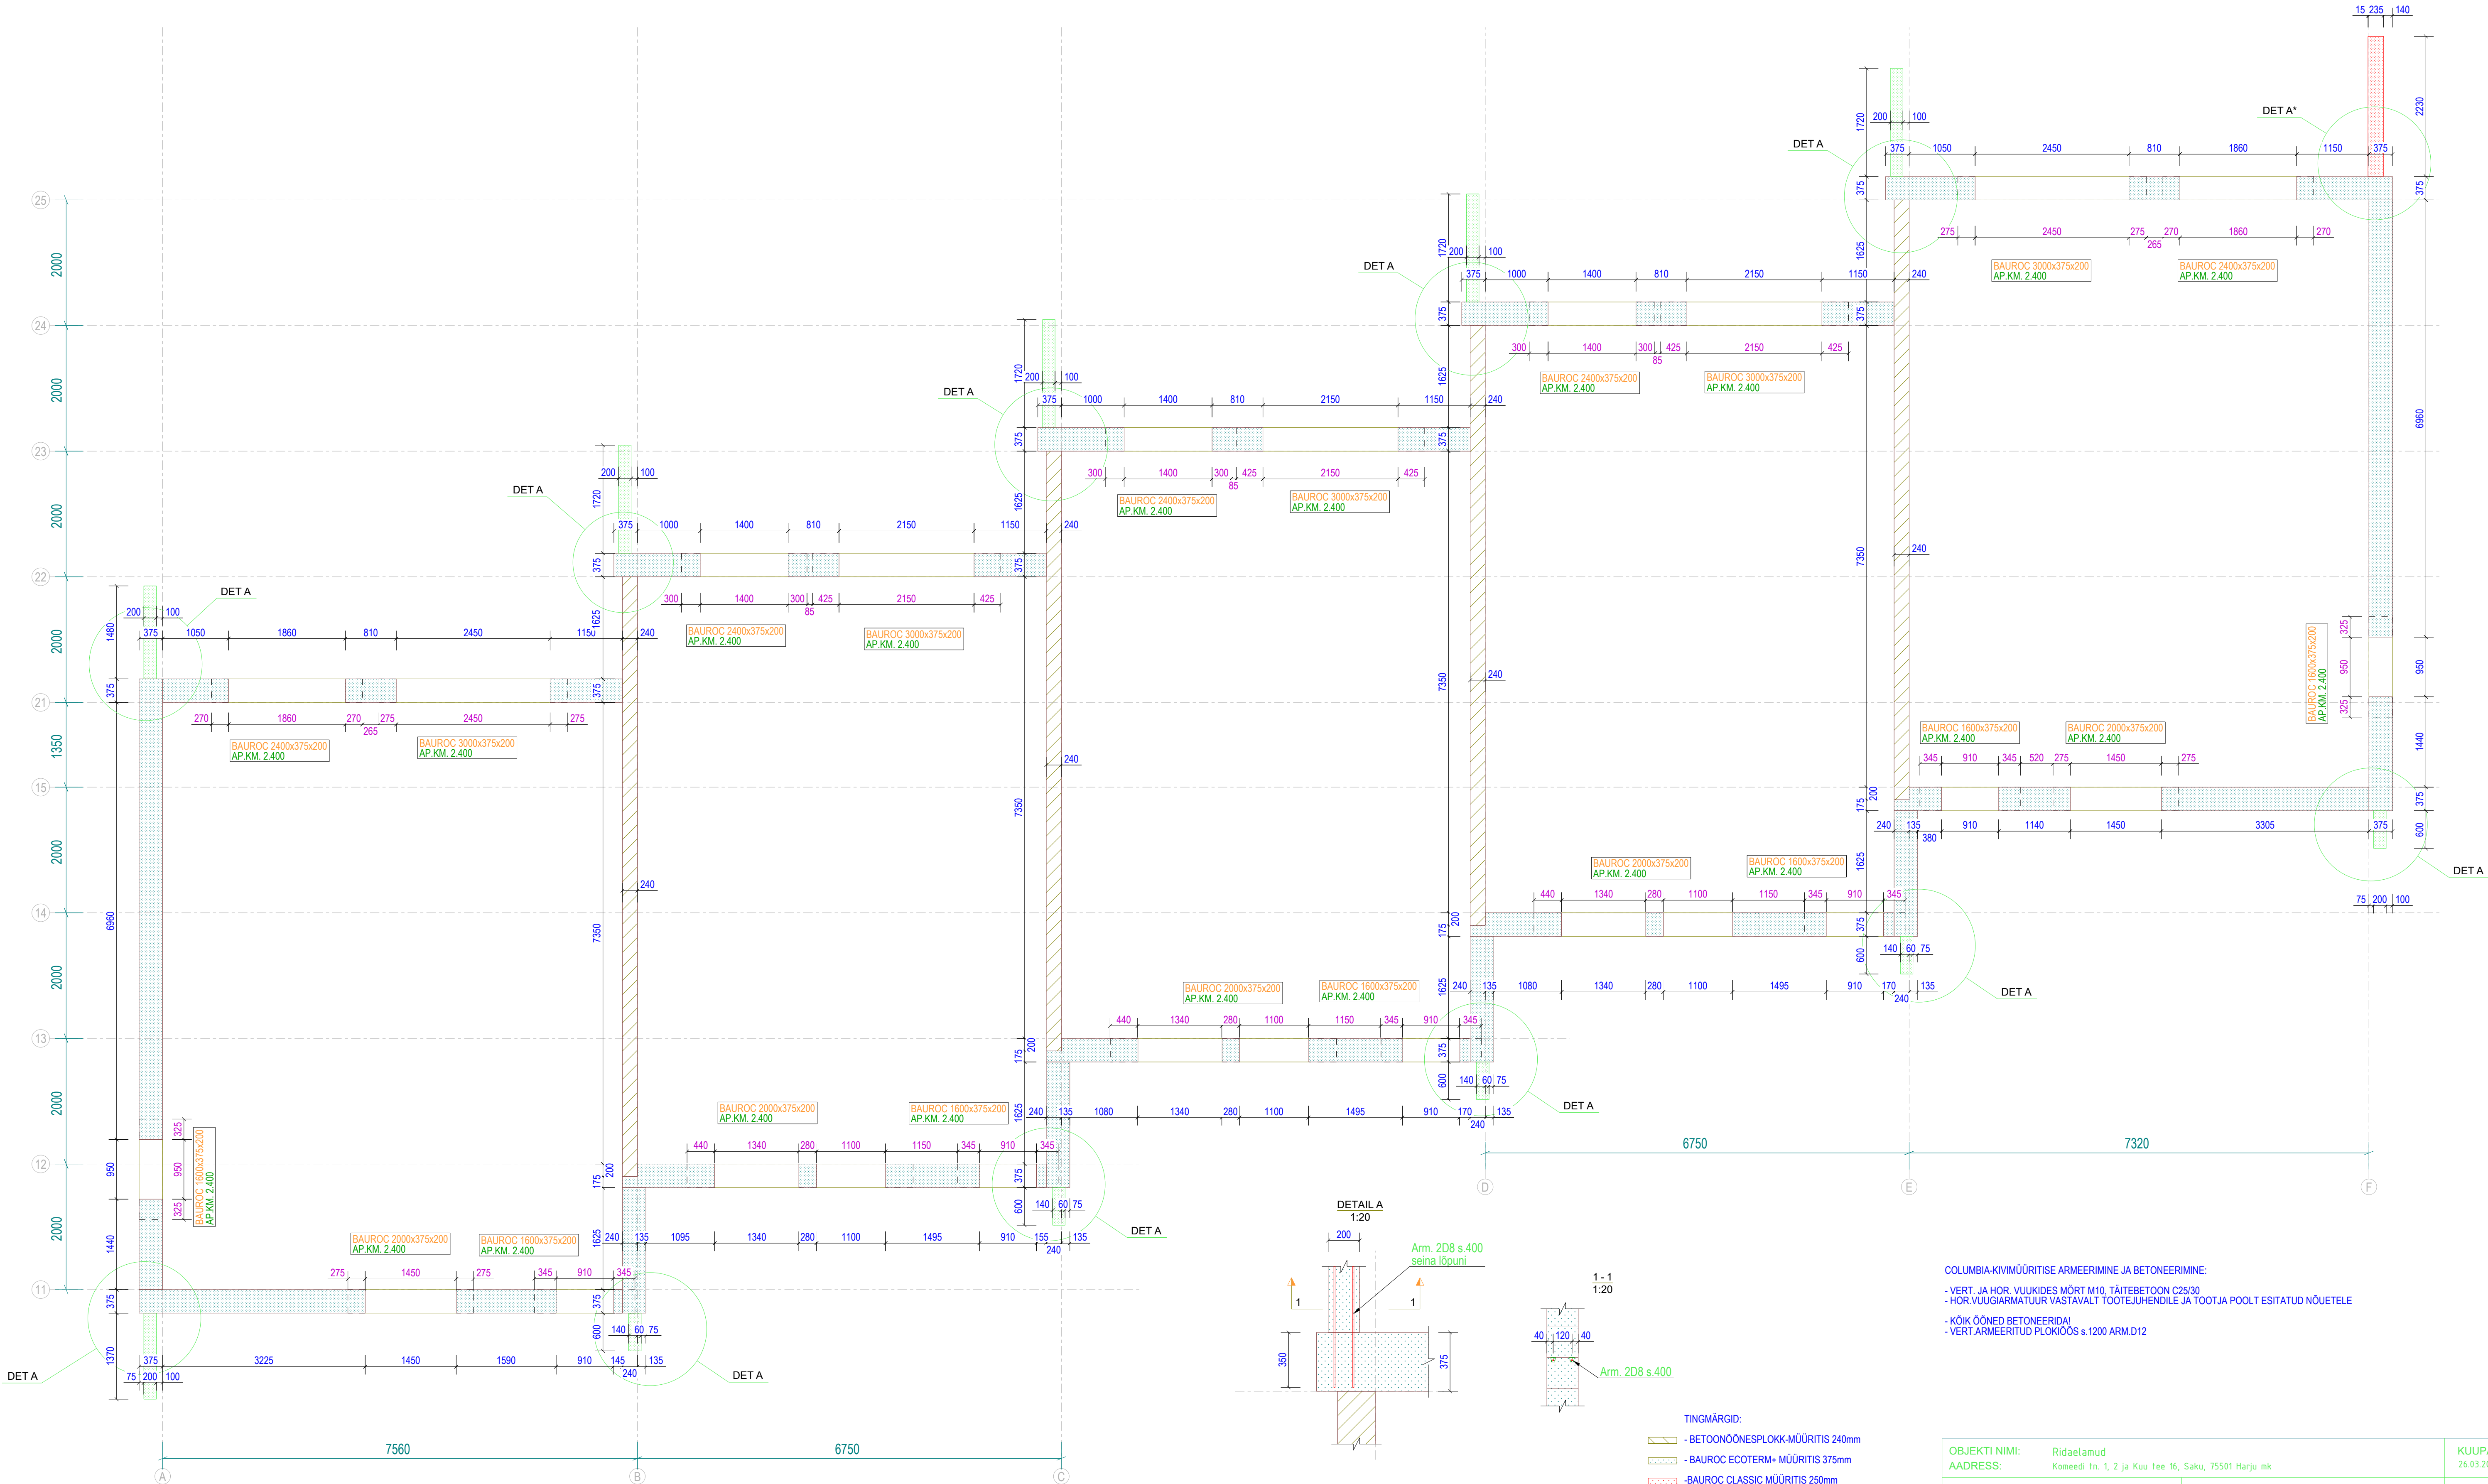

COLUMBIA-KIVIMÜÜRITISE ARMEERIMINE JA BETONEERIMINE:
- VERT. JA HOR. VUUKIDES MÕRT M10, TÄITEBETOON C25/30
- HOR. VUUGIARMATUUR VASTAVALT TOOTEJUHENDILE JA TOOTJA POOLT ESITATUD NÕUETELE
- KÕIK ÕNDED BETONEERIDA!
- VERT.ARMEERITUD FLOKIOOS s.1200 ARM.D12

OBJEKTI NIMI:	Ridaelamud	KUUPÄEV:	26.03.2025
AADRESS:	Komeedi tn. 1, 2 ja Kuu tee 16, Saku, 75501 Harju mk		
PROJEKT:	O.Paavo	JOONISE SISU:	1.Korruse kandeseinte plaan
KONTROLLIS:		PROJ.STAADIUM:	1P
		TÖÖ NR.	2024.10
		JOON.NR.	EK-3-001