BETOONKONSTRUKTSIOONIDE SPETSIFIKATSIOON

TÄHIS	ARV	BETOON	KOGUS [m3]	KAAL [t]	KOKKU [m3]	JOONIS
BAUROC 1600x200x200	1					
BAUROC 2000x200x200	9					
BAUROC 2400x200x200	5					
BAUROC 3000x200x200	5					
KOKKU	20				0.0	

2.Korruse kandeseinte plaan
1:50

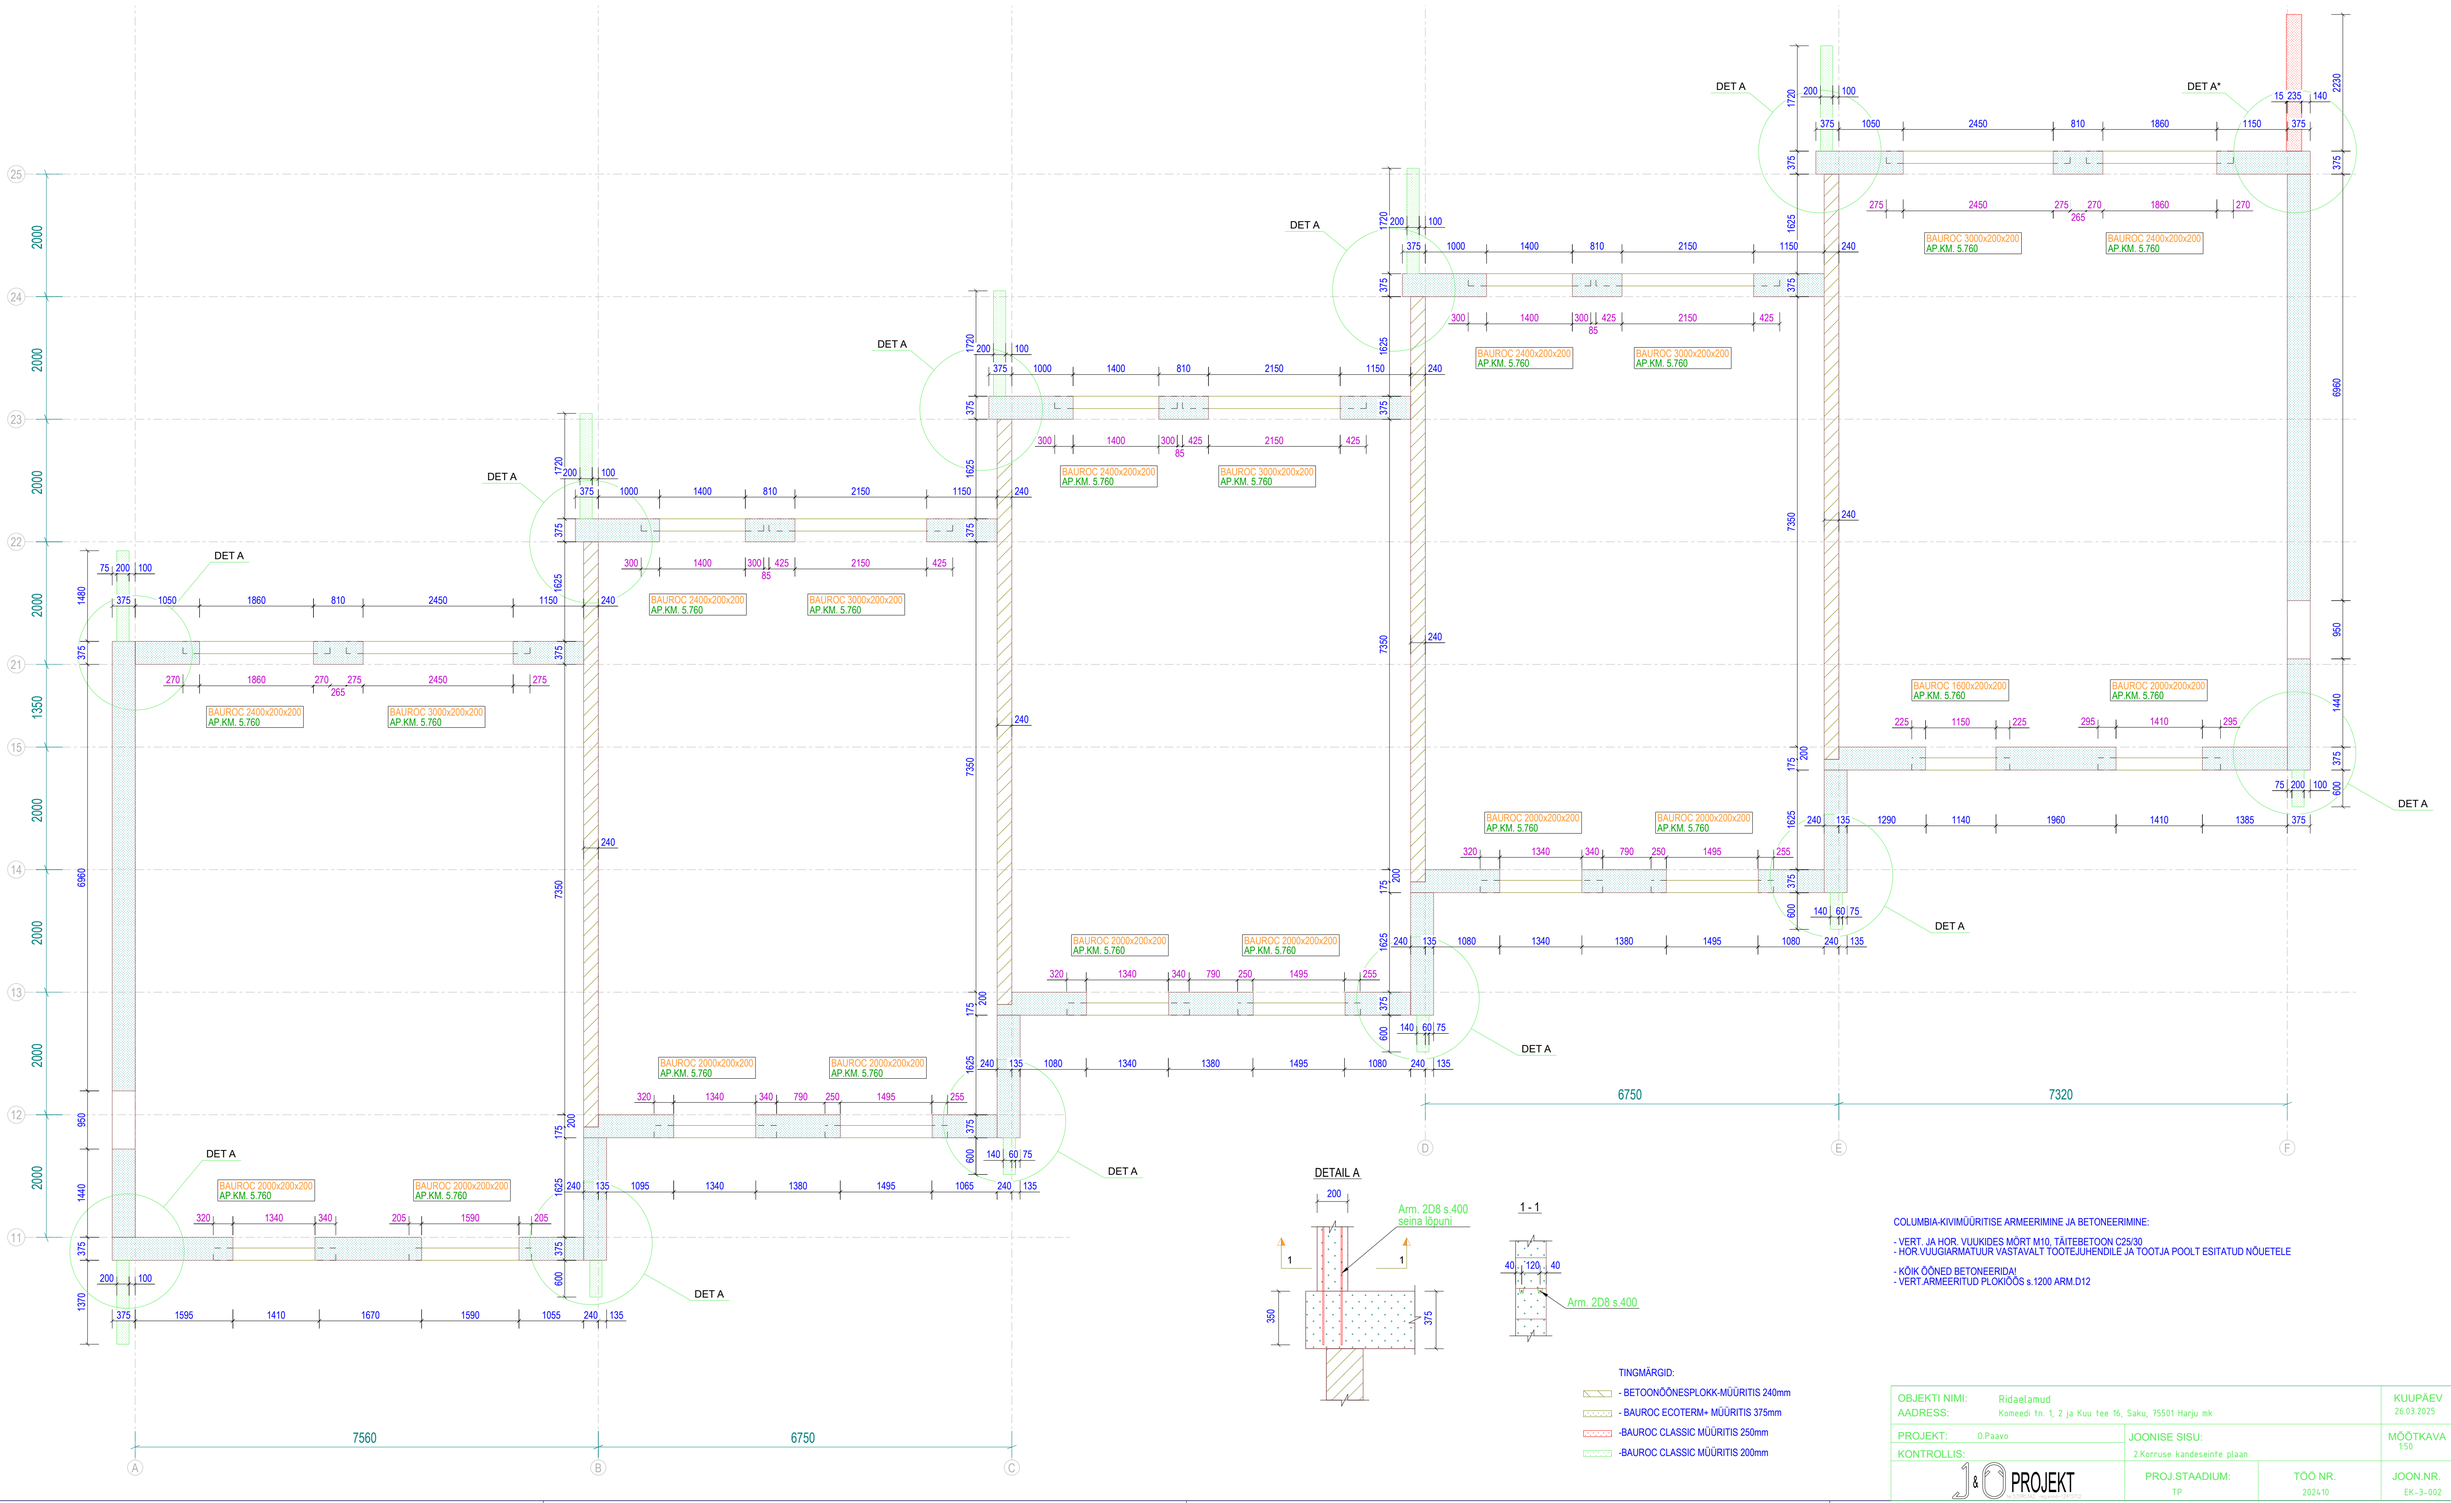

TINGMÄRGID:

- BETOONÕÕNESPLOKK-MÜÜRITIS 240mm
- BAUROC ECOTERM+ MÜÜRITIS 375mm
- BAUROC CLASSIC MÜÜRITIS 250mm
- BAUROC CLASSIC MÜÜRITIS 200mm

COLUMBIA-KIVIMÜÜRITISE ARMEERIMINE JA BETONEERIMINE:

- VERT. JA HOR. VUUKIDES MÖRT M10, TÄITEBETOON C25/30
- HOR.VUUGIARMATUUR VASTAVALT TOOTEJUHENDILE JA TOOTJA POOLT ESITATUD NÕUETELE

- KÕIK ÕÕNED BETONEERIDA!
- VERT.ARMEERITUD PLOKIÕÕS s.1200 ARM.D12

OBJEKTI NIMI: Ridaelamud			KUUPÄEV 26.03.2025
AADRESS: Komeedi tn. 1, 2 ja Kuu tee 16, Saku, 75501 Harju mk			
PROJEKT: 0.Paavo	JOONISE SISU: 2.Korruse kandeseinte plaan		MÕÕTKAVA 1:50
KONTROLLIS:			
J & O PROJEKT	PROJ.STAADIUM: TP	TÖÖ NR. 202410	JOON.NR. EK-3-002

Tekla Structures