MATERJALI SPETSIFIKATSIOON

MATERJAL	MAHT [m3]	
C30/37	9.4	

KOGUS		TÄHIS	
15	tk	WELDA150x150-110 Tarilapp	
34.6	kg	B500B	D6
710.1	kg	B500B	D12
KOKKU:	745	kg	

TERASELEMENTIDE SPETSIFIKATSIOON

Tähis	Kogus, tk	Mass, kg		Pikkus, mm	Märkus/Profiil
		ühele	kokku		
VARIKATUS VK-1	1	82.0	82.0	3935	Vt.Joon. EK-9-021
VARIKATUS VK-2	4	75.7	302.6	3500	Vt.Joon. EK-9-022
	KOKKU:	385	kg		

ÕÕNESPANEELIDE SPETSIFIKATSIOON

POS.NR.	ARV	MÕÕDUD (HxBxL)	PINDALA (m2)	KAAL (kg)	MÄRKUSED
ÕP-I-1	1	220x880x7535	9.04	1906	
ÕP-I-2	5	220x1200x7535	9.04	2625	
ÕP-I-3	1	220x1200x7535	9.04	2600	
ÕP-I-4	2	220x860x4190	5.03	1060	
ÕP-I-5	2	220x1200x4190	5.03	1459	
ÕP-I-6	1	220x1200x7570	9.08	2602	
ÕP-I-7	1	220x1200x7570	9.08	2637	
ÕP-I-8	1	220x380x7570	4.54	760	
ÕP-I-9	3	220x915x6690	8.03	1726	
ÕP-I-10	6	220x1200x6690	8.03	2330	
ÕP-I-11	3	220x1200x6690	8.03	2306	
ÕP-I-12	3	220x860x3380	4.06	855	
ÕP-I-13	3	220x1200x3380	4.06	1177	
ÕP-I-14	3	220x1200x6725	8.07	2308	
ÕP-I-15	3	220x1200x6725	8.07	2342	
ÕP-I-16	3	220x375x6725	4.03	662	
ÕP-I-17	1	220x880x7535	9.04	1906	
ÕP-I-18	1	220x1200x7535	9.04	2600	
ÕP-I-19	1	220x1200x7535	9.04	2600	
ÕP-I-20	1	220x380x7535	4.52	756	
KOKKU:	45		319 m2	84.6 T	

1.korruse vahelae plaan
1:50

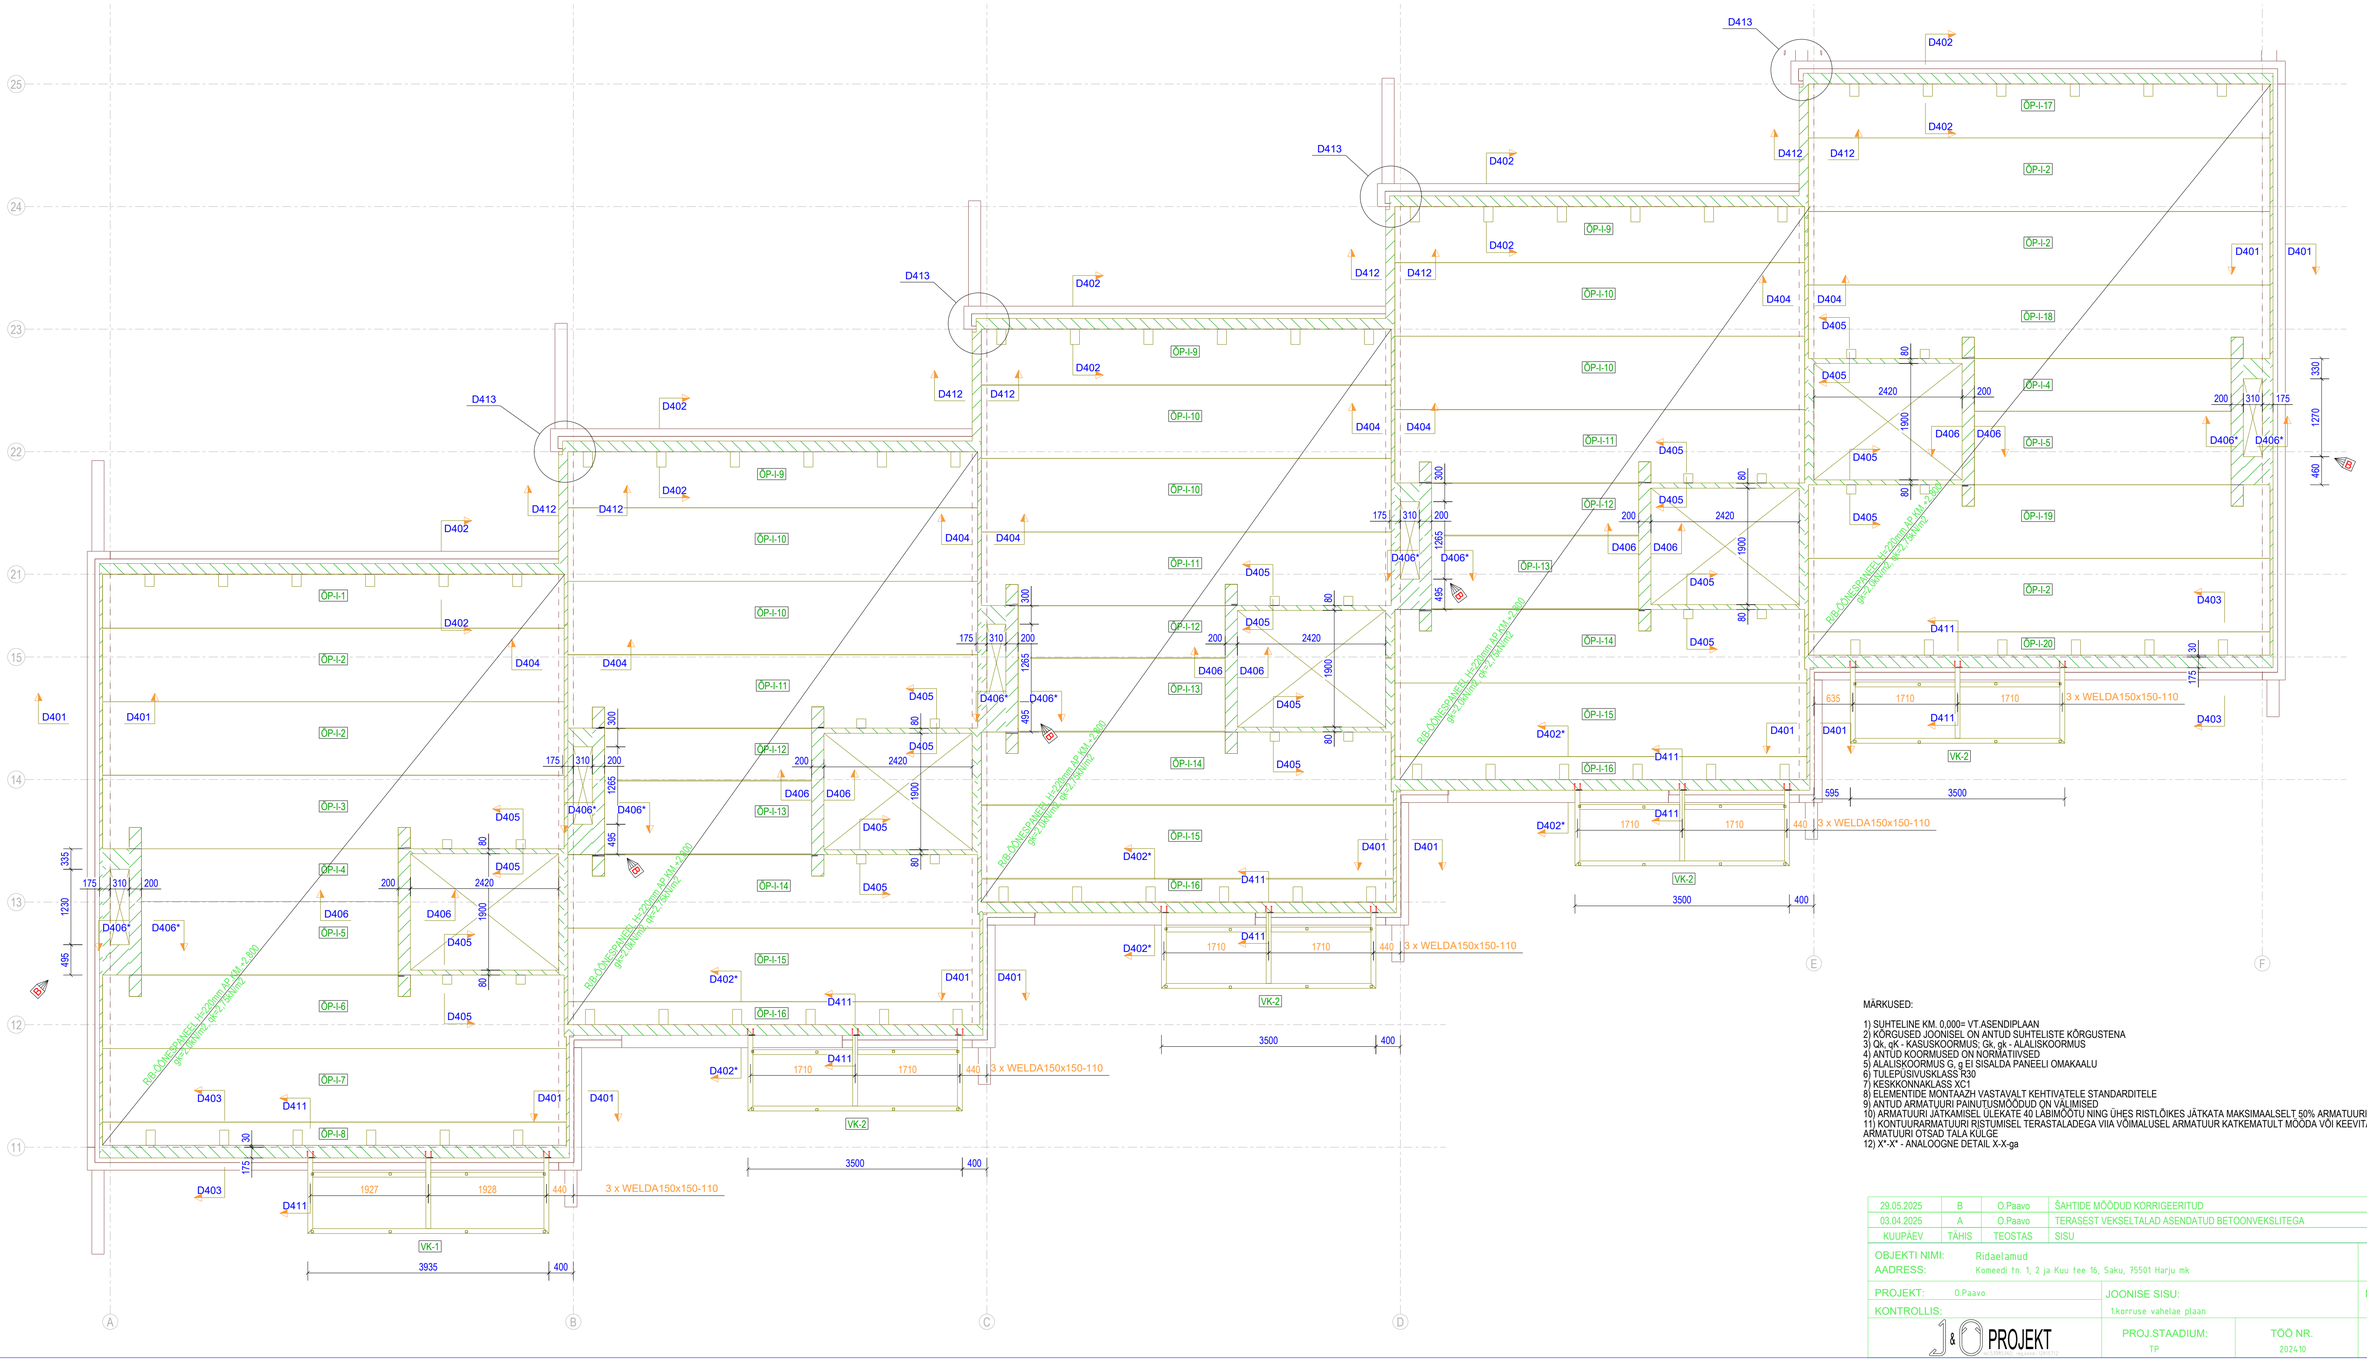

MÄRKUSED:

1) SUHTELINE KM. 0,000= VT.ASENDIPLAAN
2) KÕRGUSED JOONISEL ON ANTUD SUHTELISTE KÕRGUSTENA
3) Qk, qK - KASUSKOORMUS; Gk, gk - ALALISKOORMUS
4) ANTUD KOORMUSED ON NORMATIIVSED
5) ALALISKOORMUS G, g EI SISALDA PANEELI OMAKAALU
6) TULEPÜSIVUSKLASS R30
7) KESKKONNAKLASS XC1
8) ELEMENTIDE MONTAAZH VASTAVALT KEHTIVATELE STANDARDITELE
9) ANTUD ARMATUURI PAINUTUSMÕÕDUD ON VÄLMISED
10) ARMATUURI JÄTKAMISEL ÜLEKATE 40 LÄBIMÕÕTU NING ÜHES RISTLÕIKES JÄTKATA MAKSIMAALSELT 50% ARMATUURIST
11) KONTUURARMATUURI RISTUMISEL TERASTALADEGA VIIA VÕIMALUSEL ARMATUUR KATKEMATULT MÖÖDA VÕI KEEVITADA ARMATUURI OTSAD TALA KÜLGE
12) X*-X* - ANALOOGNE DETAIL X-X-ga

29.05.2025	B	O.Paavo	ŠAHTIDE MÕÕDUD KORRIGEERITUD
03.04.2025	A	O.Paavo	TERASEST VEKSELTALAD ASENDATUD BETOONVEKSLITEGA
KUUPÄEV	TÄHIS	TEOSTAS	SISU

OBJEKTI NIMI: Ridaelamud			KUUPÄEV 26.03.2025
AADRESS: Komeedi tn. 1, 2 ja Kuu tee 16, Saku, 75501 Harju mk			
PROJEKT: O.Paavo	JOONISE SISU: 1.korruse vahelae plaan		MÕÕTKAVA 1:50
KONTROLLIS:	J&O PROJEKT	PROJ.STAADIUM: TP	TÖÖ NR. 202410	JOON.NR. EK-4-001

Tekla Structures