


MATERJALI SPETSIFIKATSIOON		
MATERJAL	MAHT [m3]	
C30/37	5.9	
KOGUS	TÄHIS	
389.9 kg	B500B D12	
KOKKU:	390 kg	

PUIT-METALLALADE SPETSIFIKATSIOON			
POS	PROFIIL	ARV	PIKKUS [mm]
PMT-1	PS 370/145	1	7735
PMT-2	PS 370/145	6	6925
PMT-3	PS 370/145	1	7825
PMT-4	PS 370/145	1	7920
PMT-5	PS 370/145	1	7710
	KOKKU	10	

ÕONESPANEELIDE SPETSIFIKATSIOON					
POS.NR	ARV	MÕÕDUD (HxBxL)	PINDALA (m2)	KAAL (kg)	MÄRKUSED
ÕP-II-1	1	220x920x7535	9.04	1955	
ÕP-II-2	6	220x1200x7535	9.04	2625	
ÕP-II-3	2	220x1200x7535	9.04	2586	
ÕP-II-4	1	220x1200x7570	9.08	2633	
ÕP-II-5	1	220x1200x7570	9.08	2620	
ÕP-II-6	3	220x920x6690	8.03	1732	
ÕP-II-7	8	220x1200x6690	8.03	2330	
ÕP-II-8	2	220x1200x6690	8.03	2301	
ÕP-II-9	3	220x1200x6690	8.03	2303	
ÕP-II-10	3	220x1200x6690	8.03	2295	
ÕP-II-11	2	220x1200x6725	8.07	2338	
ÕP-II-12	3	220x1200x6725	8.07	2326	
ÕP-II-13	1	220x920x7535	9.04	1955	
ÕP-II-14	1	220x1200x7535	9.04	2583	
ÕP-II-15	1	220x1200x7535	9.04	2586	
ÕP-II-16	1	220x1200x7535	9.04	2588	
ÕP-II-17	1	220x1200x7535	9.04	2608	
KOKKU:	40		338 m2	94.3 T	

2.korruse katuslae plaan
1:50

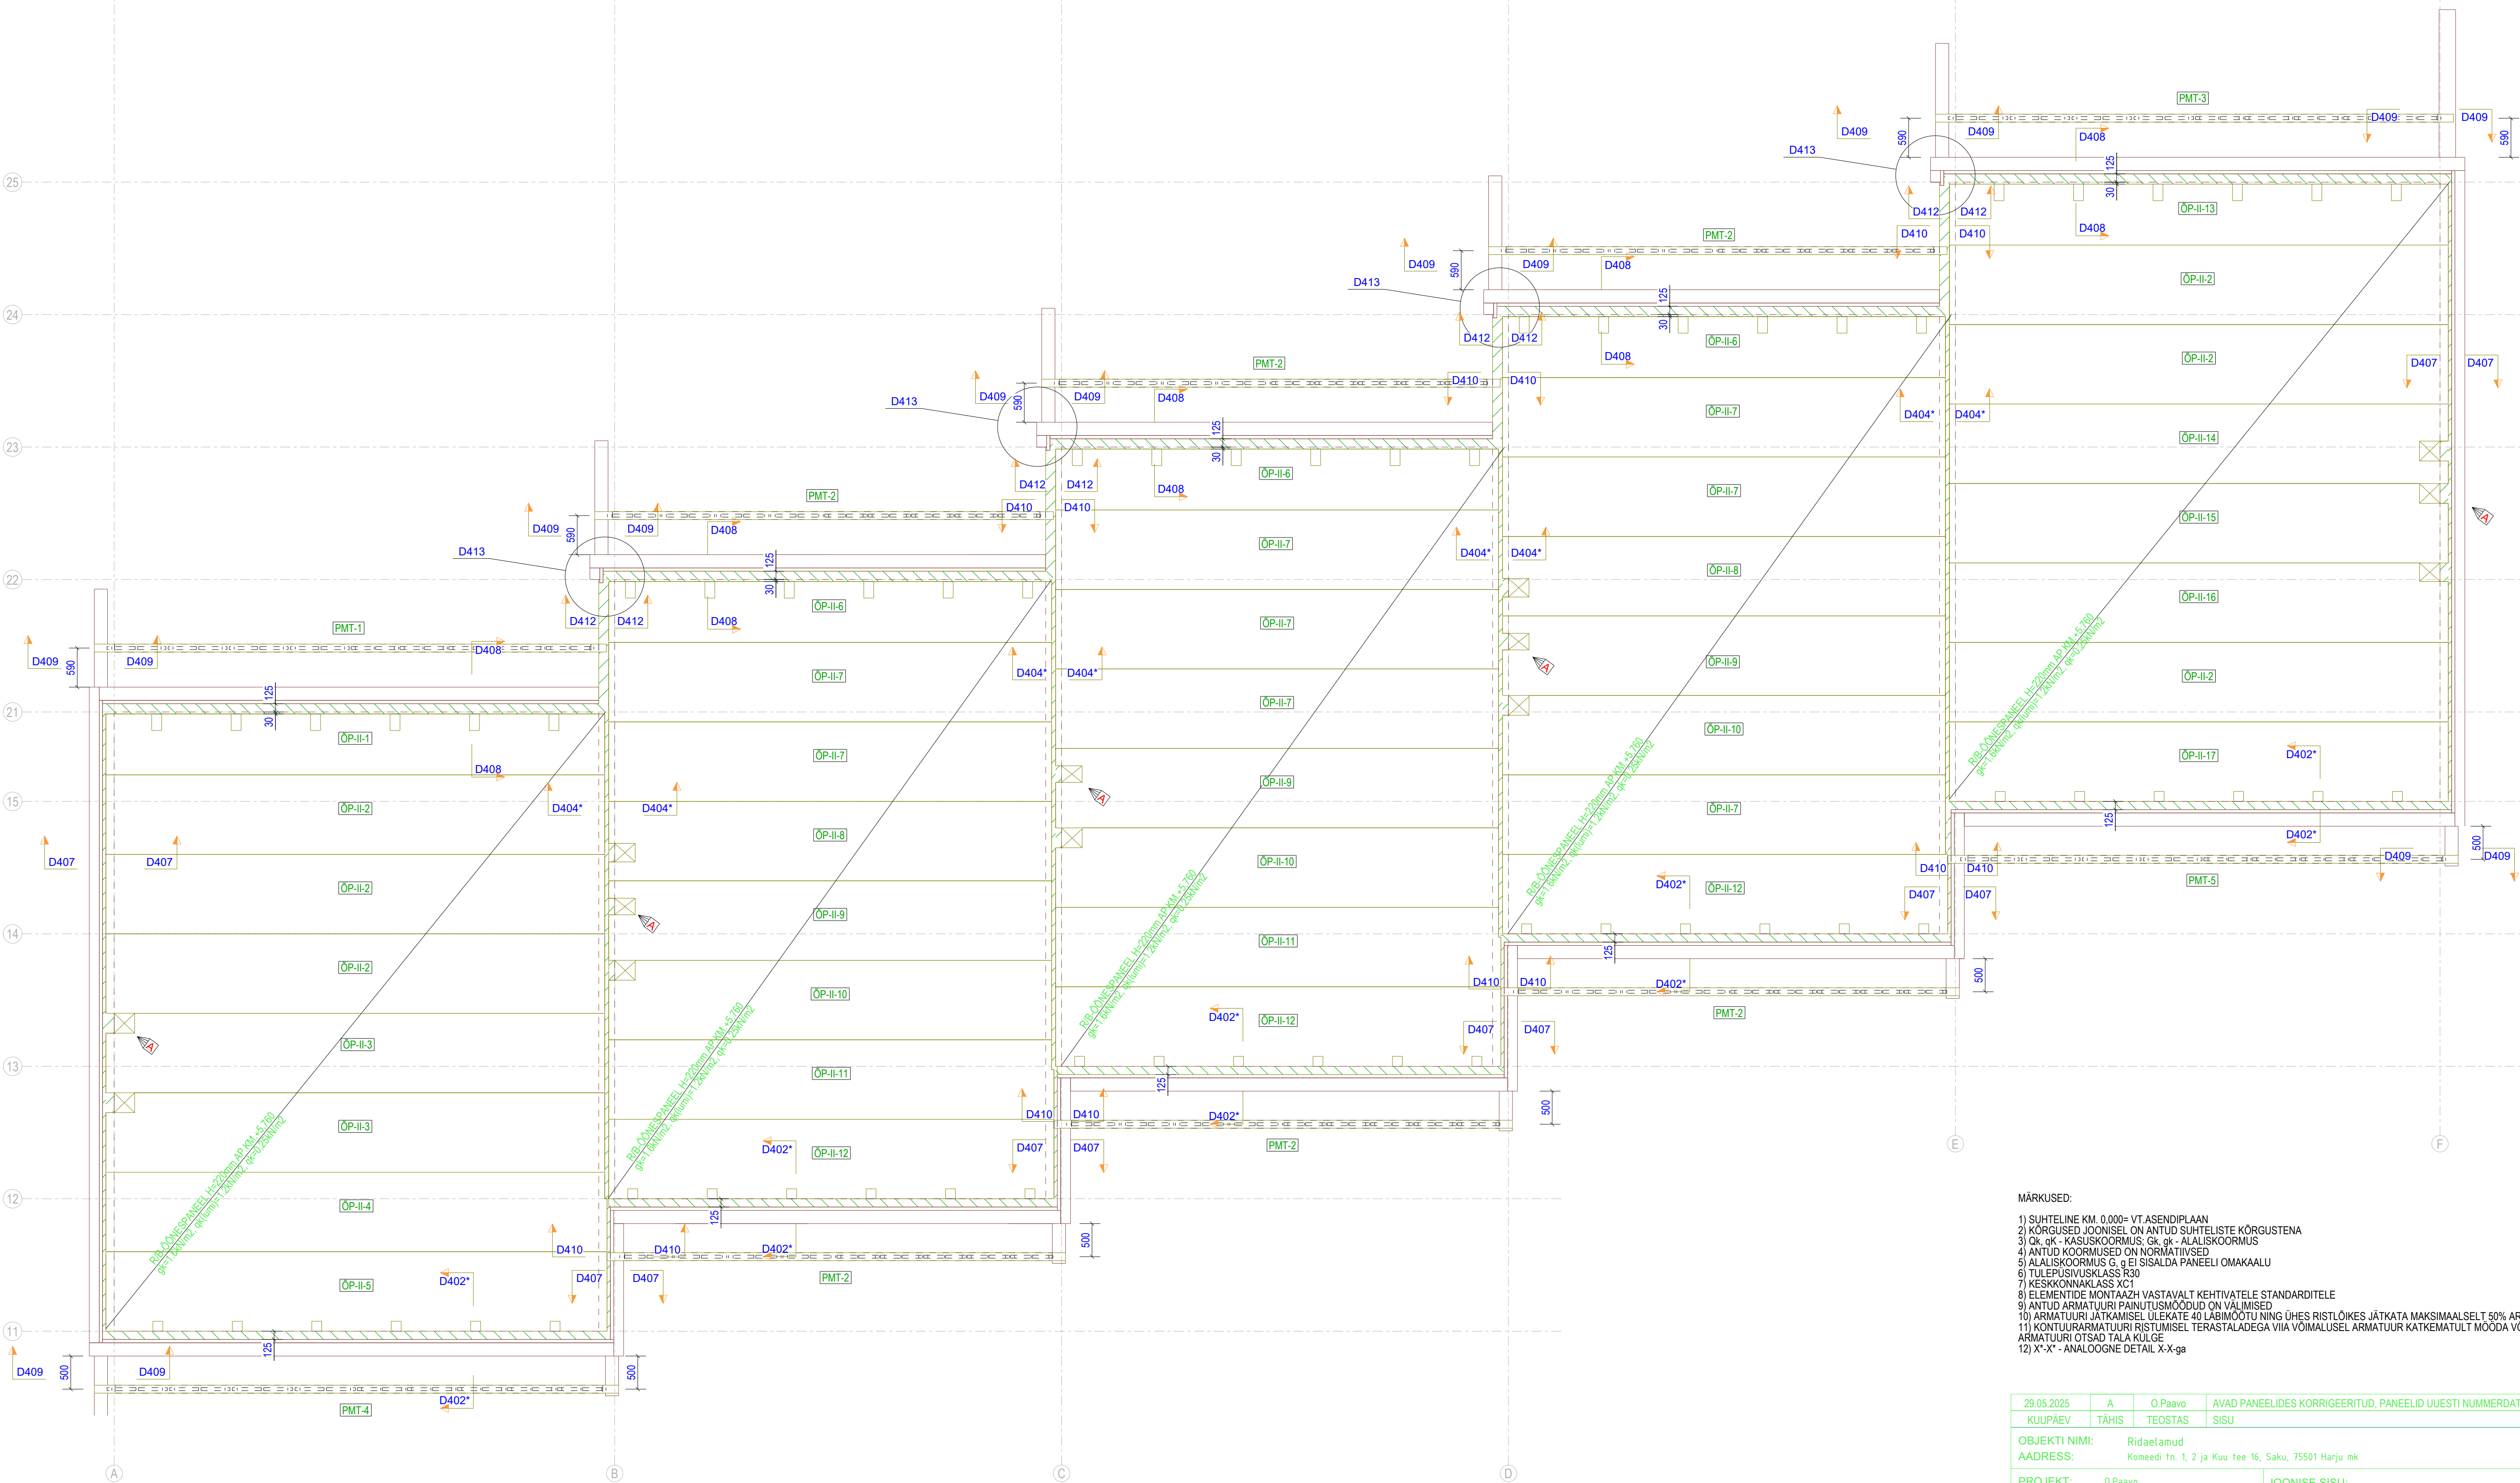

- MÄRKUSED:
- SUHTELINE KM. 0.000=VT.ASENDIPLAAN
 - KÕRGUSED JOONISEL ON ANTUD SUHTELISTE KÕRGUSTENA
 - OK, OK - KASUKOORMUS, GK, GK - ALALISKOORMUS
 - ANTUD KOORMUSED ON NORMATIIVSED
 - ALALISKOORMUS G, g EI SISALDA PANEELI OMAKAALU
 - TULEPÜSIVUSKLASS R30
 - KESKKONNAKLASS XC1
 - ELEMENTIDE MONTAAZH VASTAVALT KEHTIVATELE STANDARDITELE
 - ANTUD ARMATUURI PAINUTUSMÕDUD ON VALMISED
 - ARMATUURI JÄTKAMISEL ÜLEKATE 40 LÄBIMÕDUT NING ÜHES RISTLÕIKES JÄTKATA MAKSIMAALSELT 50% ARMATUURIST
 - KONTUURARMATUURI RISTUMISEL TERASTALADEGA VIA VOIMALUSEL ARMATUUR KATKEMATULT MÕDDA VÕI KEEVITADA
 - ARMATUURI OTSAD TALA KÜLGEL
 - X-X' - ANALOOGNE DETAIL X-X-ga

29.05.2025	A	O.Paavo	AVAD PANEELIDES KORRIGEERITUD, PANEELID UUESTI NUMMERDATUD
KUUPÄEV	TÄHIS	TEOSTAS	SISU
OBJEKTI NIMI:	Ridaelamud		
Aadress:	Komeedi tn. 1, 2 ja Kuu tee 16, Saku, 75501 Harju mk		
PROJEKT:	O.Paavo	JOONISE SISU:	
KONTROLLIS:		2.korruse katuslae plaan	
		PROJ.STAADIUM:	TP
		TÖÖ NR.	2024.10
		JOON.NR.	EK-4-002