


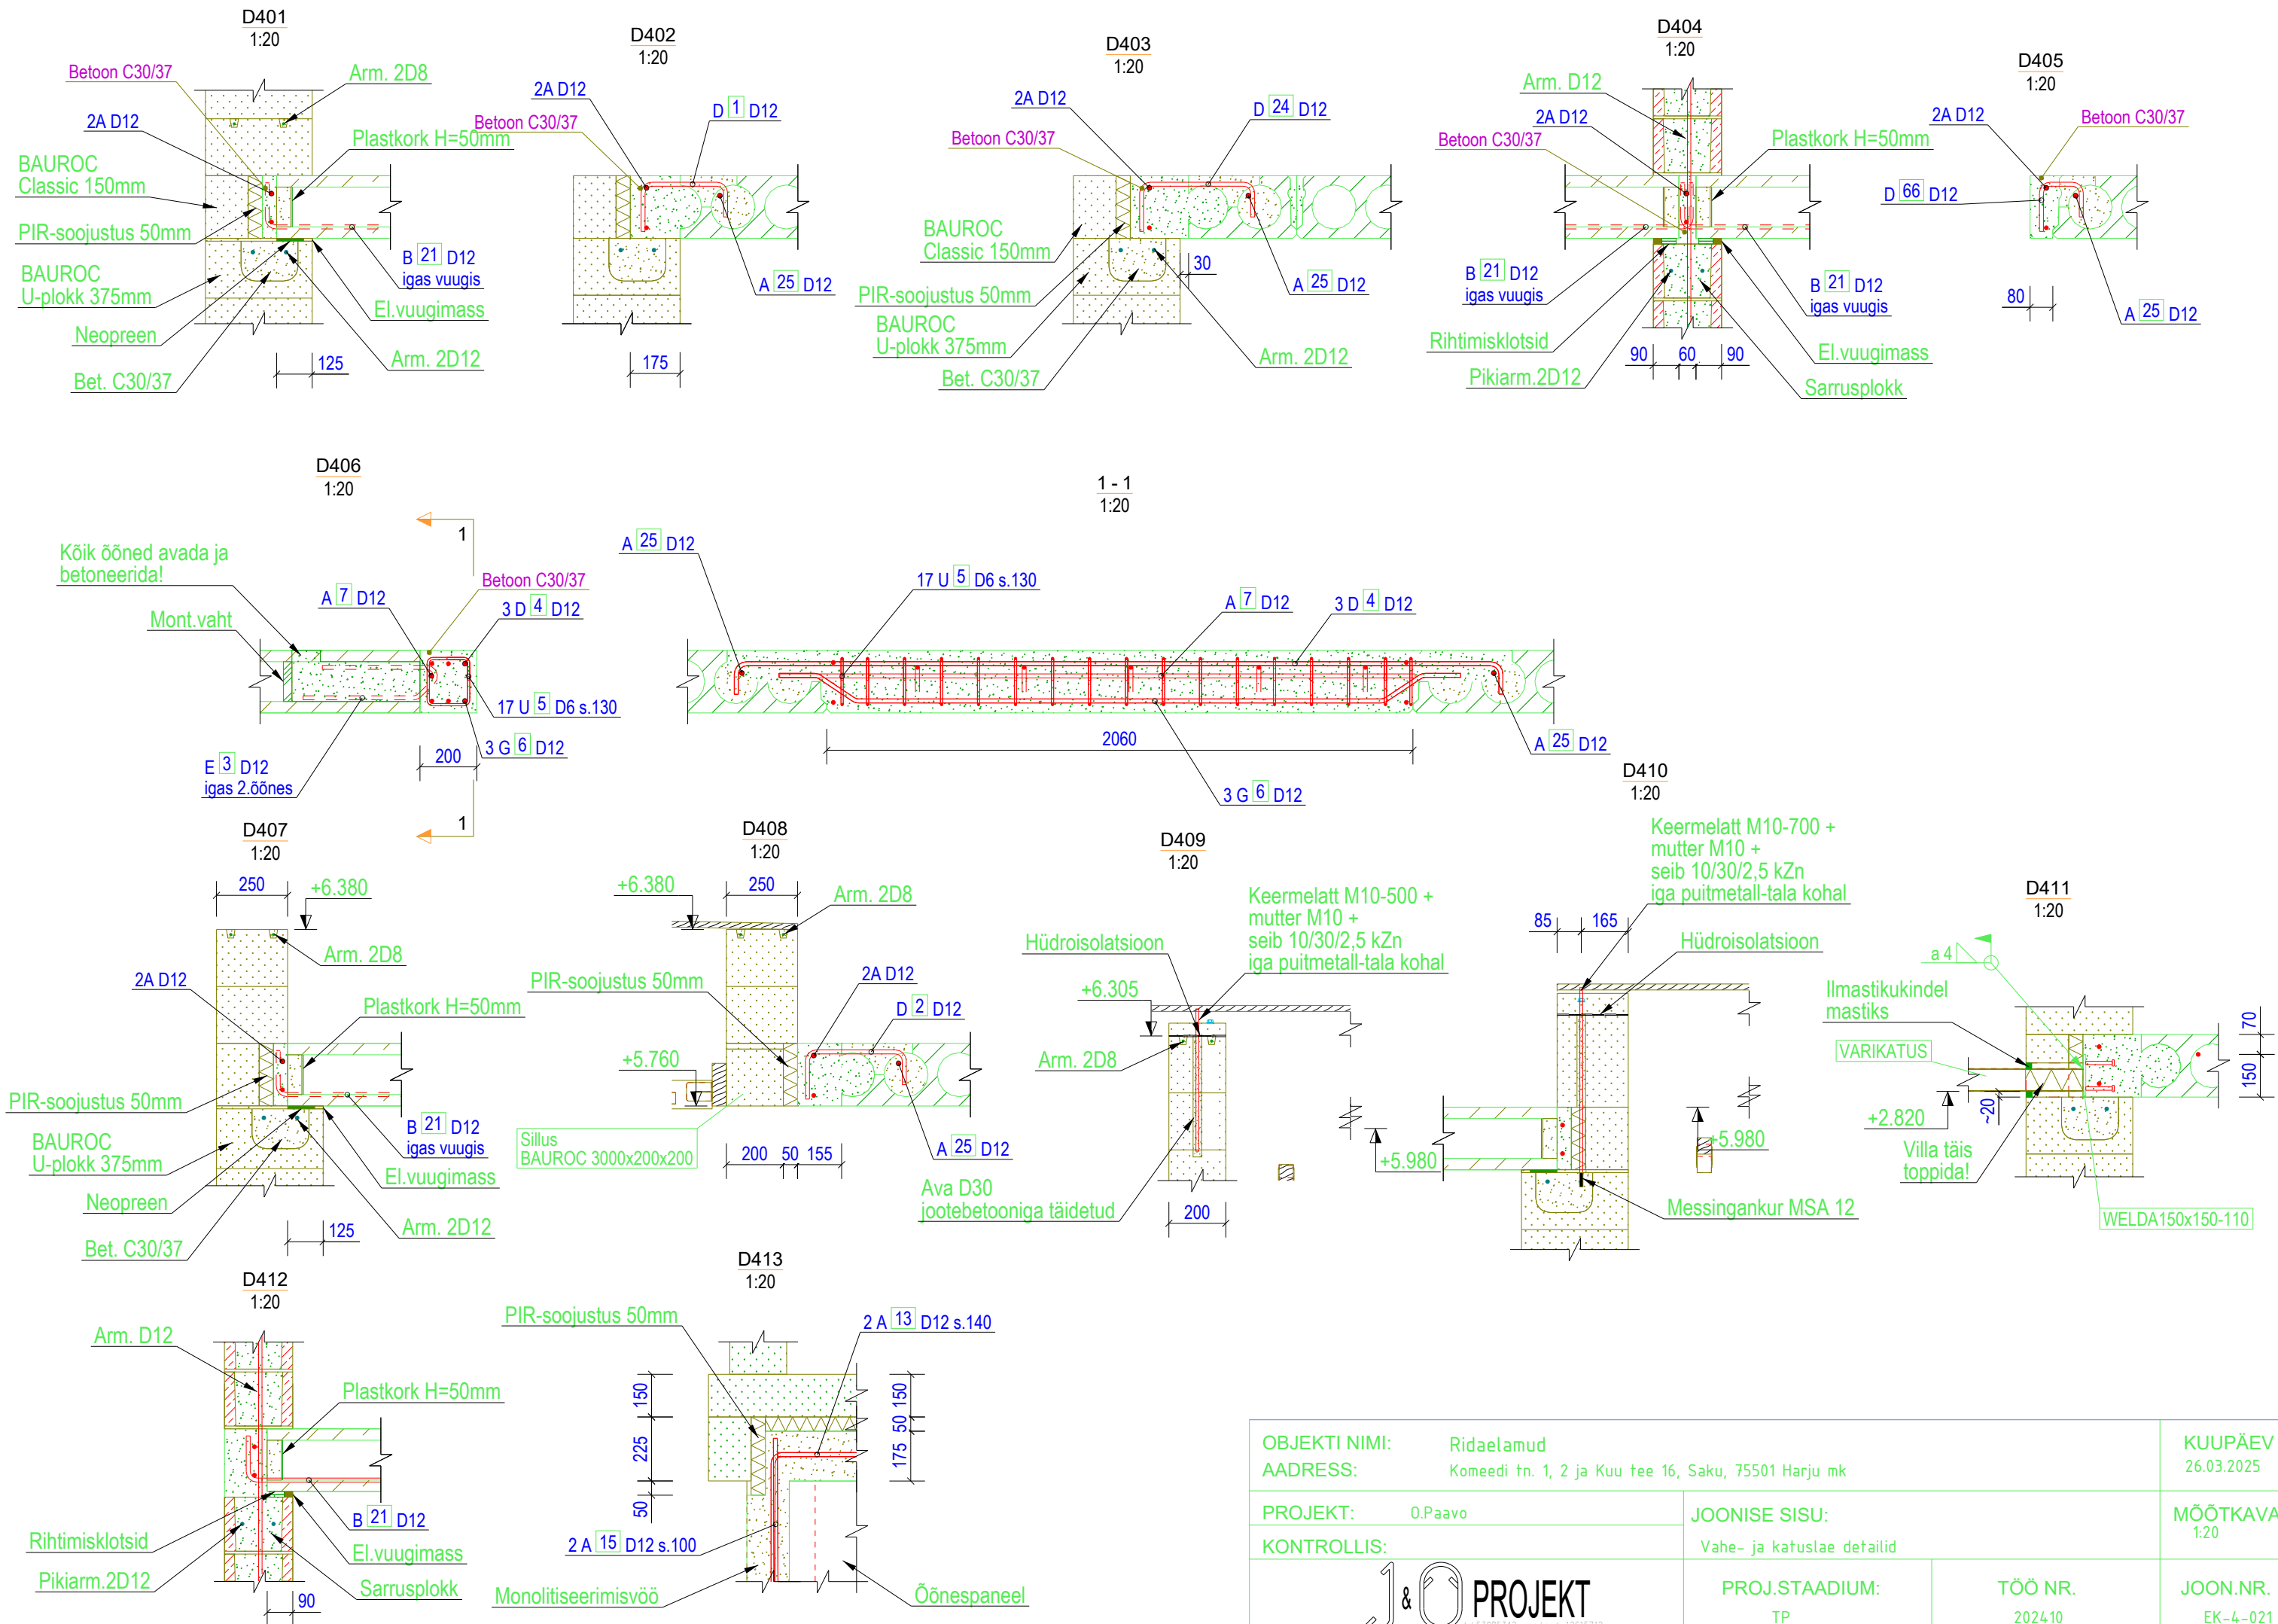

OBJEKTI NIMI:	Ridaelamud	KUUPÄEV:	26.03.2025
ADDRESS:	Komeedi tn. 1, 2 ja Kuu tee 16, Saku, 75501 Harju mk		
PROJEKT:	O.Paavo	JOONISE SISU:	MÕÕTKAVA 1:20
KONTROLLIS:		Vahe- ja katustlae detailid	
		PROJ.STAADIUM:	TP
		TÖÖ NR.	2024-10
		JOON.NR.	EK-4-021