



Plaan
1:100

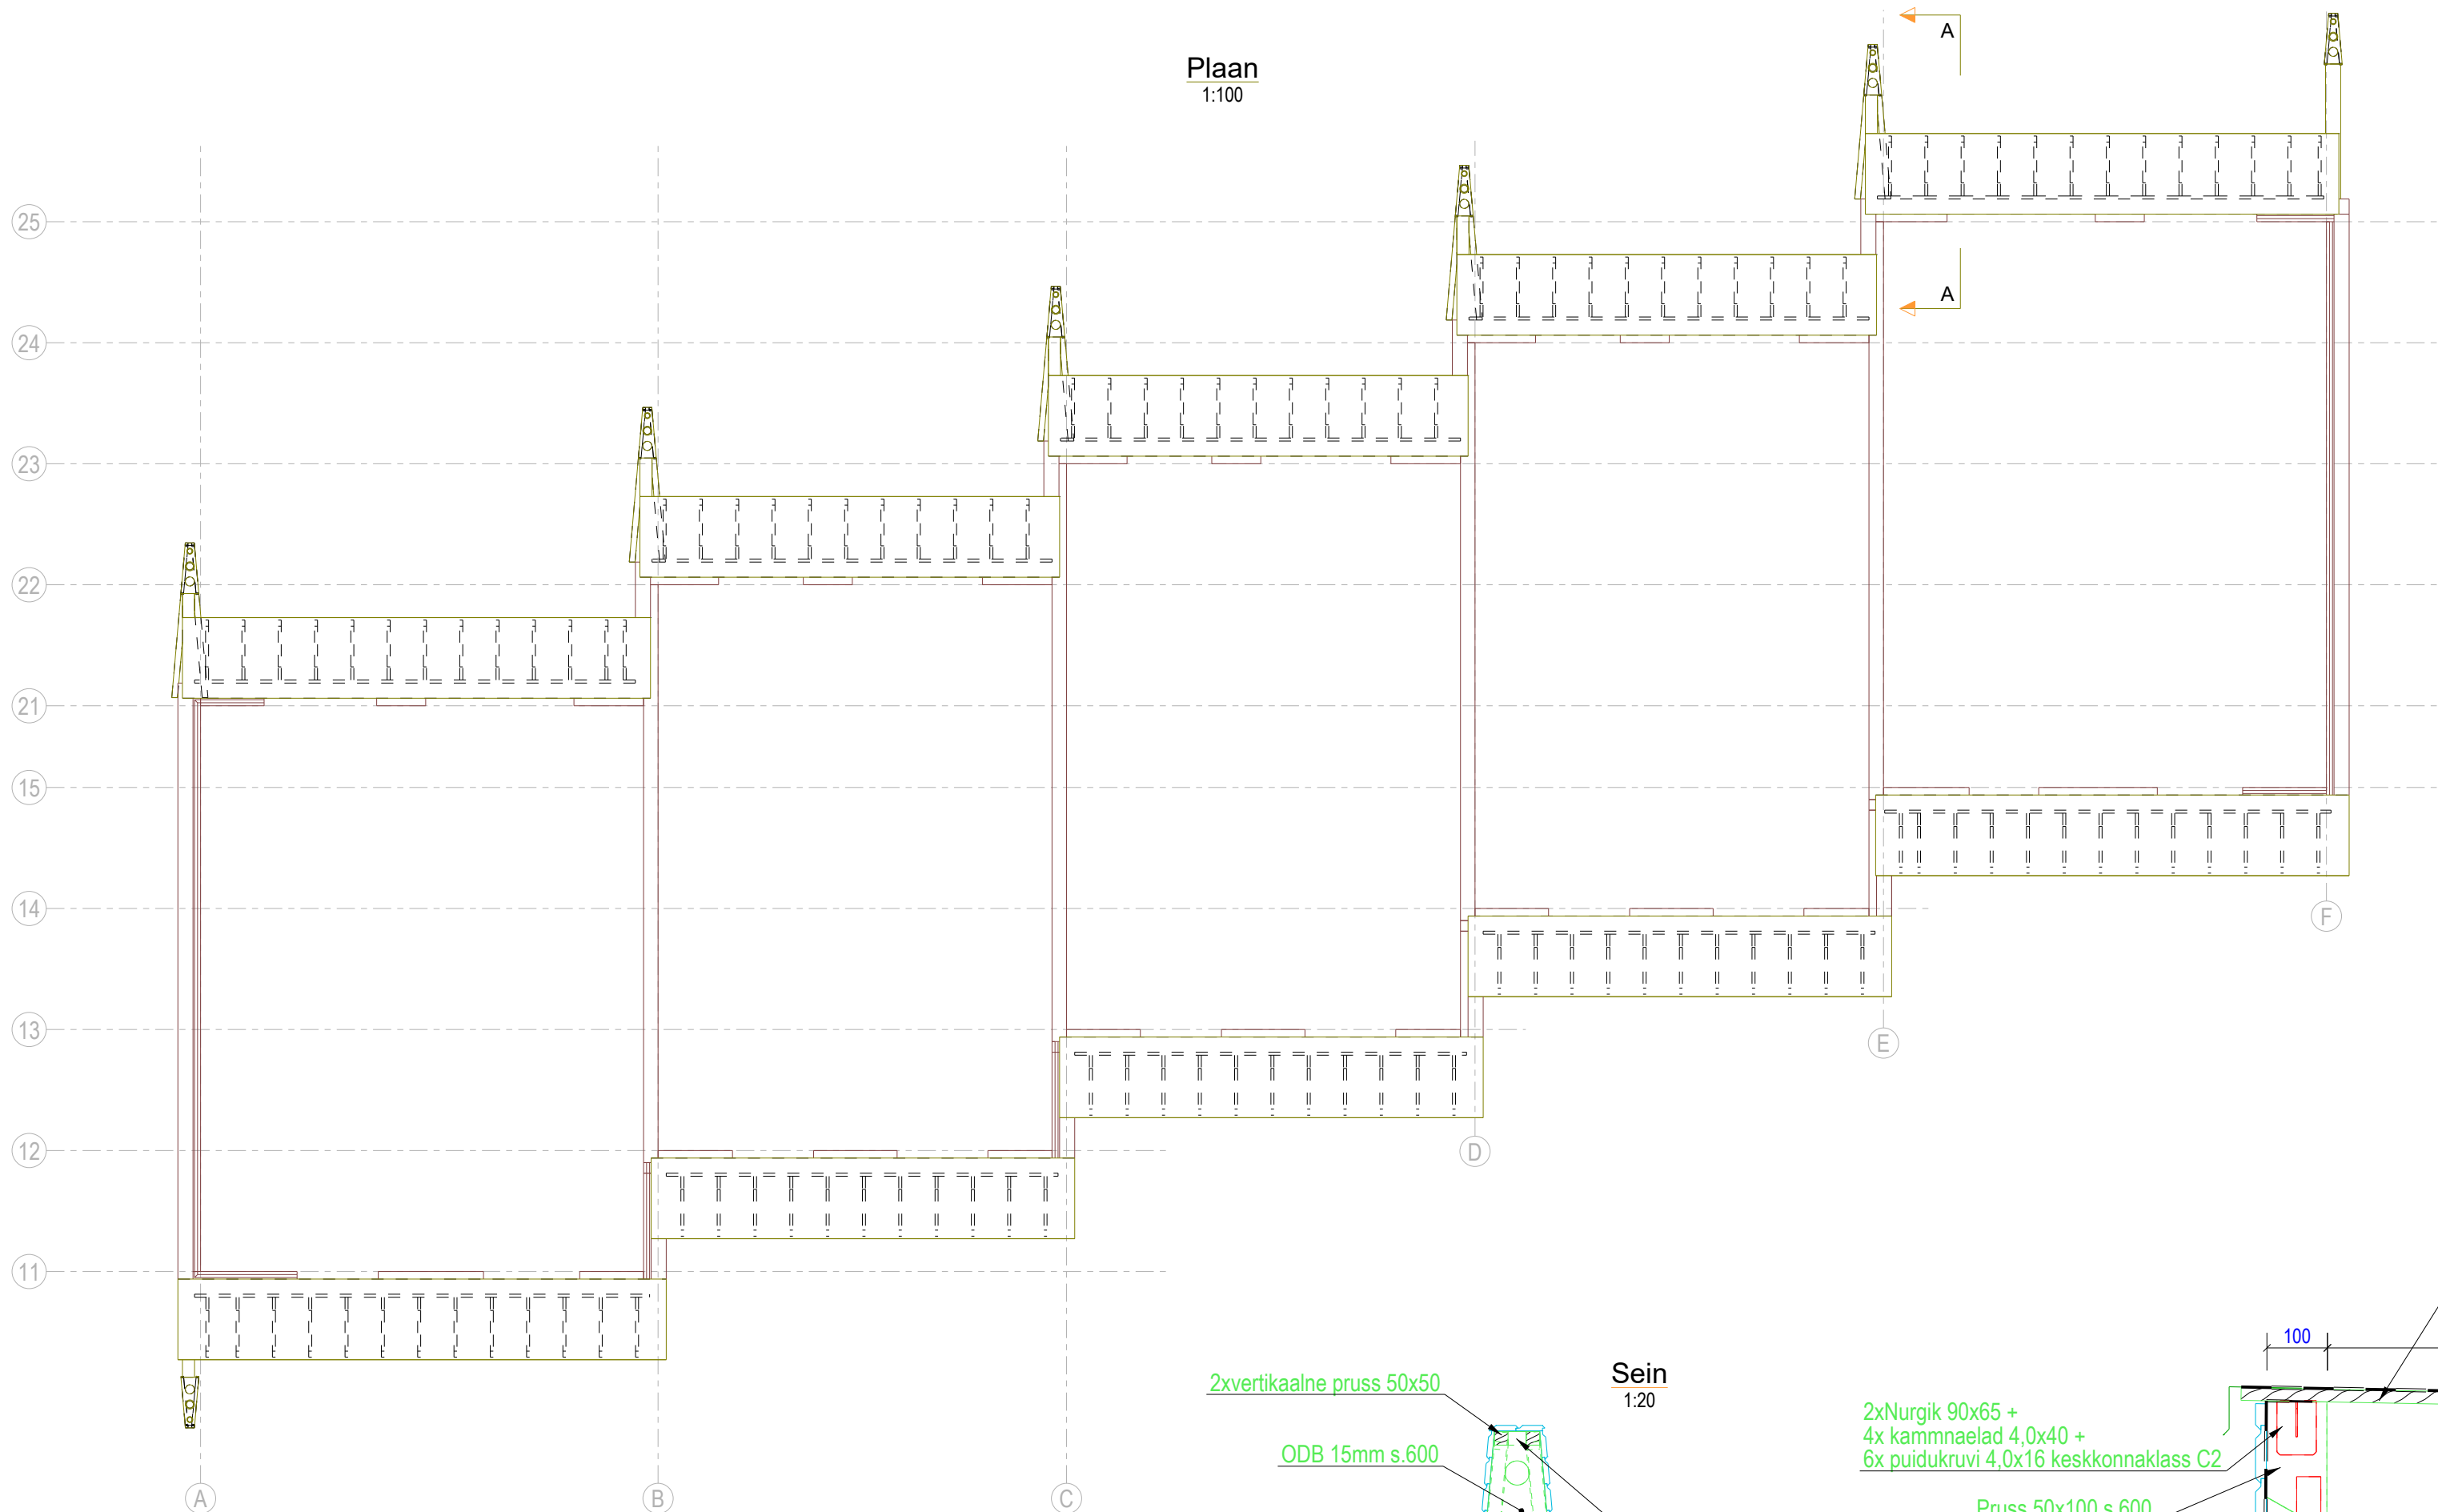


OSB-plaadi kuju
1:10


ARV: 77TK

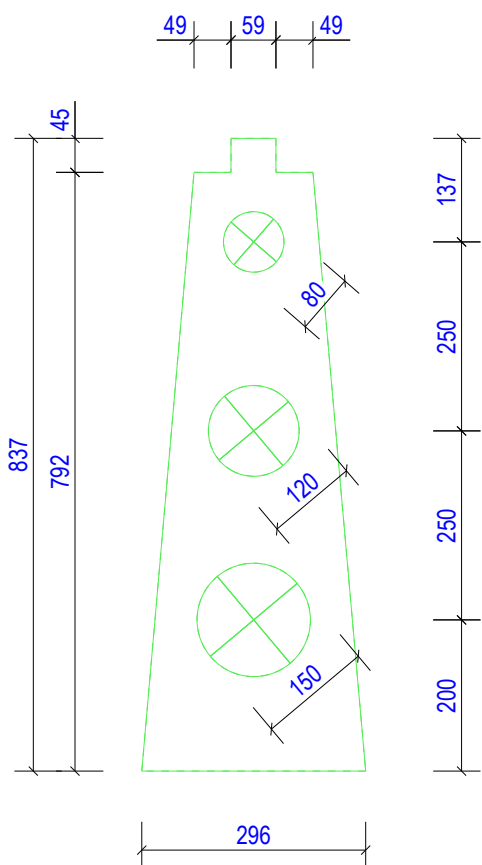


Sein
1:20

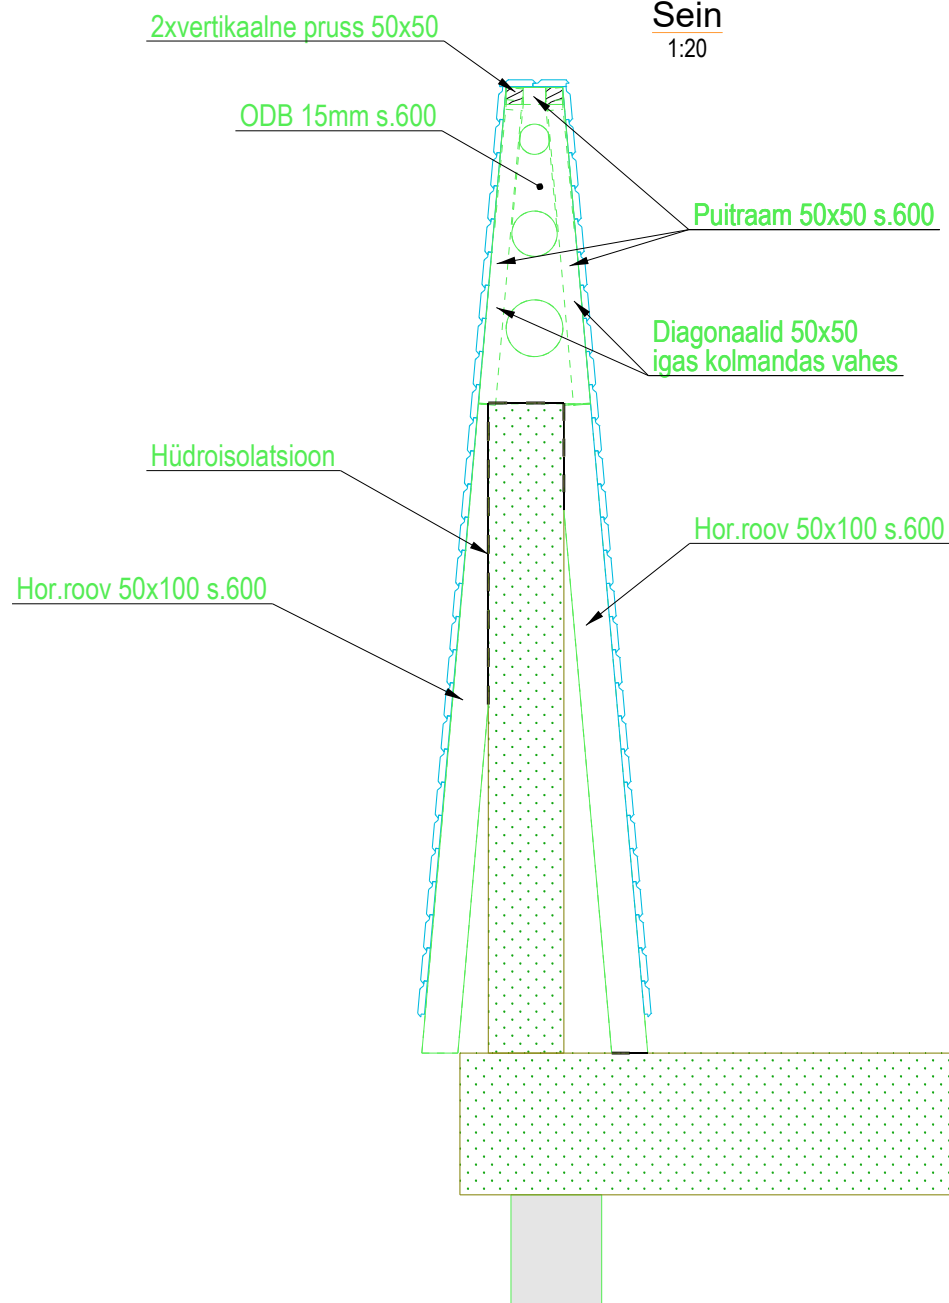

A-A
1:50

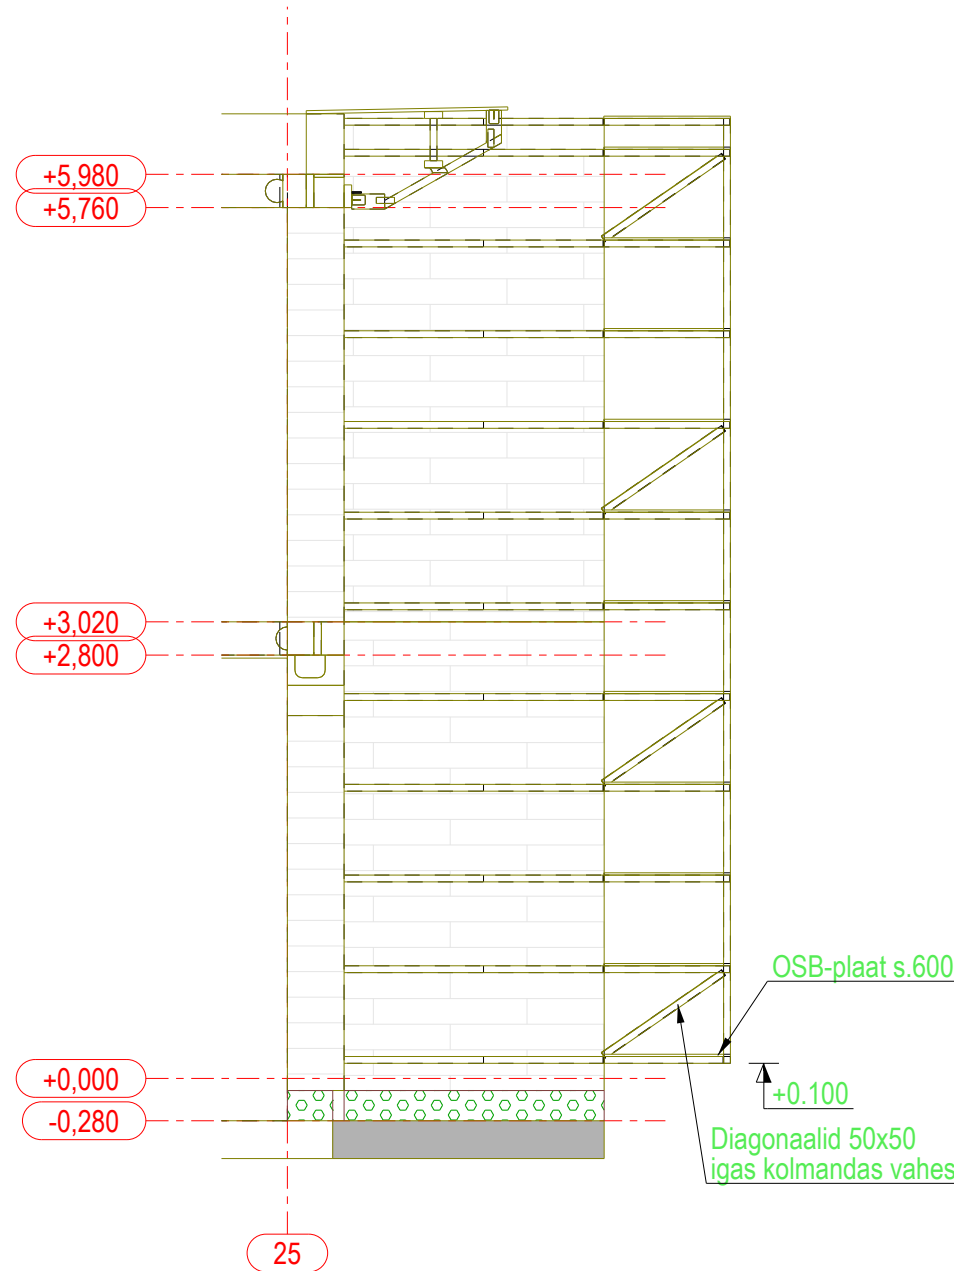

Varikatus
1:10

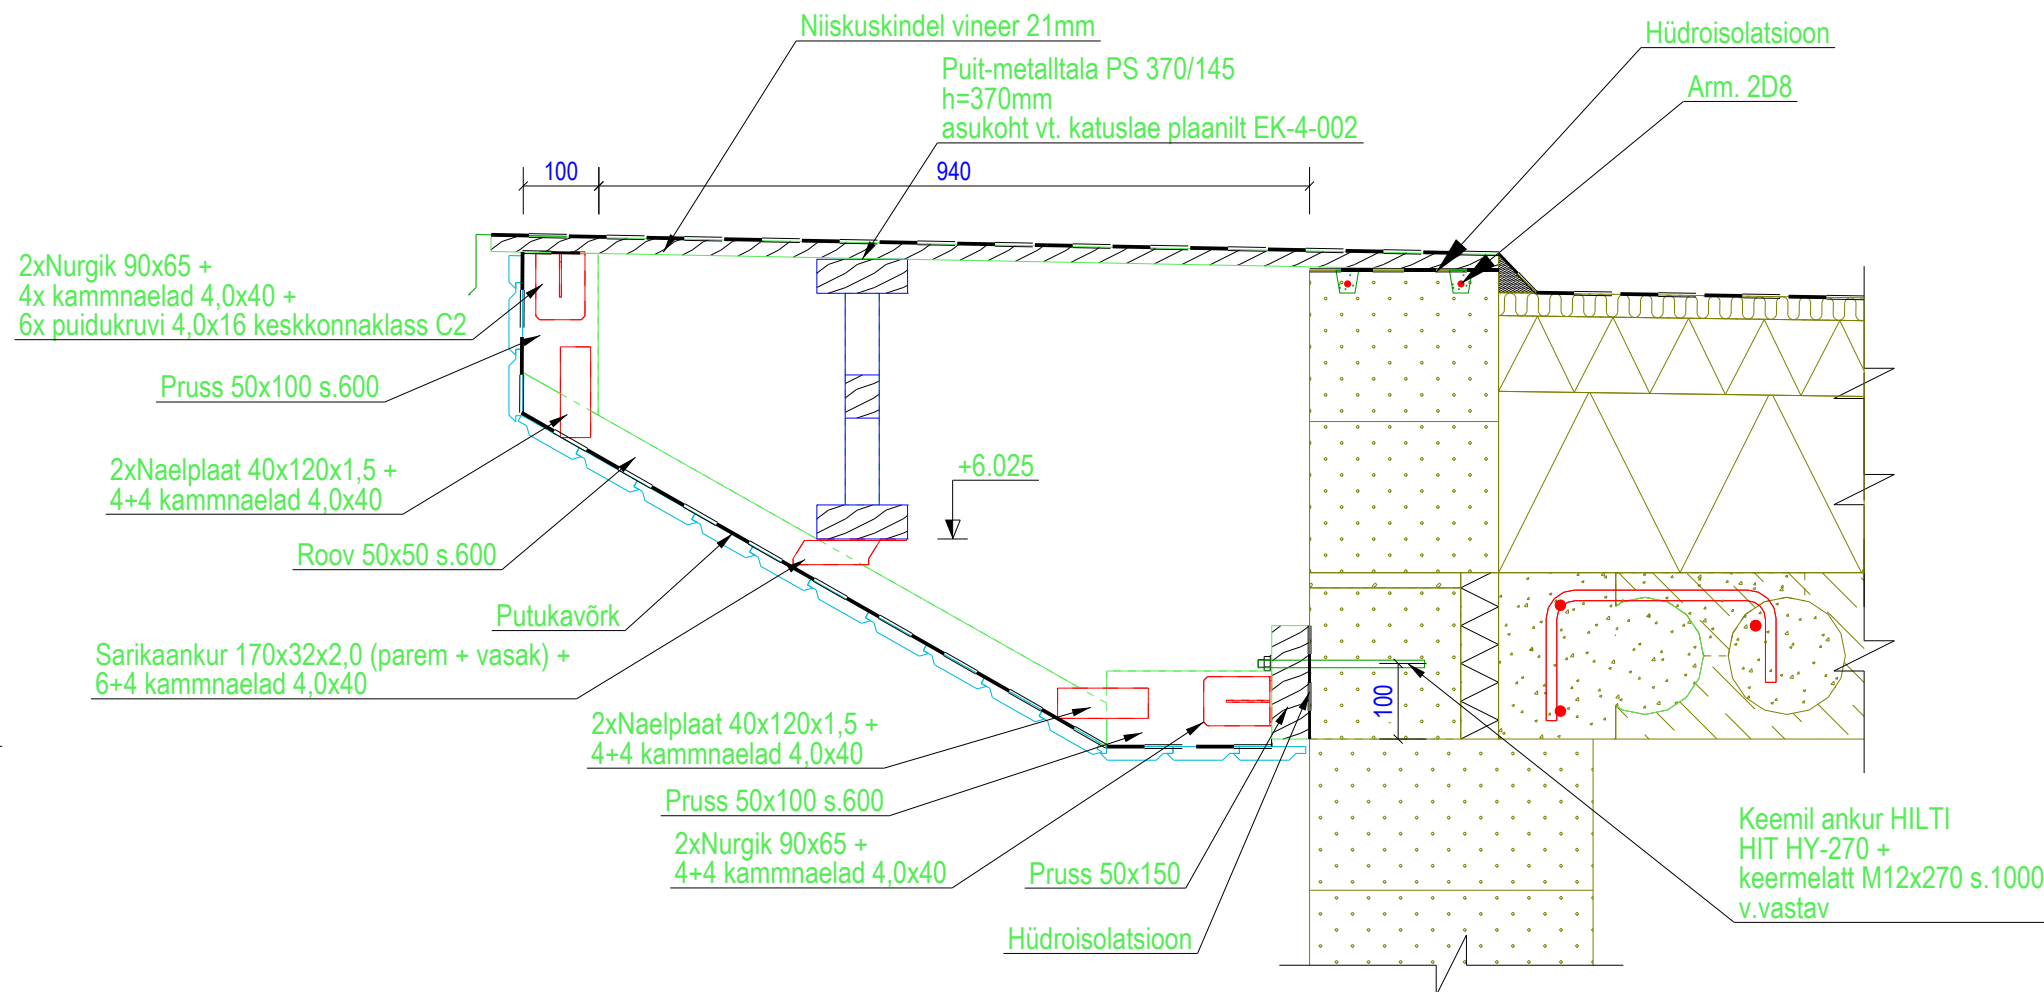

MÄRKUSED:

- KÕIK KÕRGUSMÄRGID ON SUHTELISED
- KÕIK VÄLISED KINNITUSVAHENDID TSINGITUD
- PUITKONSTRUKTSIOONID IGAL POOL ERALDADA KIVIKONSTRUKTSIOONIDEST HÜDROISOLATSIOONIGA!

OBJEKTI NIMI:	Ridaelamud	KUUPÄEV:	26.03.2025
ADDRESS:	Komeedi tn. 1, 2 ja Kuu tee 16, Saku, 75501 Harju mk		
PROJEKT:	O.Paavo	JOONISE SISU:	MÕÕTKAVA 1:10 1:20 1:50
KONTROLLIS:		Puidust välised seinad ja varikatused	
		PROJ.STAADIUM:	TP
		TÖÖ NR.	2024.10
		JOON.NR.	EK-5-001