


ELEMENDI VK-2 SPETSIFIKATSIOON, MIDA VALMISTATAKSE 4 TK

POS.	PROFIIL	KLASS	PIKKUS [mm]	PINDALA [m2]	KAAL [kg]	ARV
1005	PL3*34	S235J2	34	0.0	0.0	8
P-12	SHS80*3	S355J2H	1233	0.8	8.7	2
P-14	SHS80*3	S355J2H	1153	0.4	8.4	1
P-16	SHS40*3	S235J2	47	0.1	0.2	8
P-17	SHS80*3	S355J2H	3500	1.1	24.8	1
P-18	SHS80*3	S355J2H	1630	1.0	11.8	2
			KOKKU:	3.4	75.7	

Varikatus VK-2
1:20

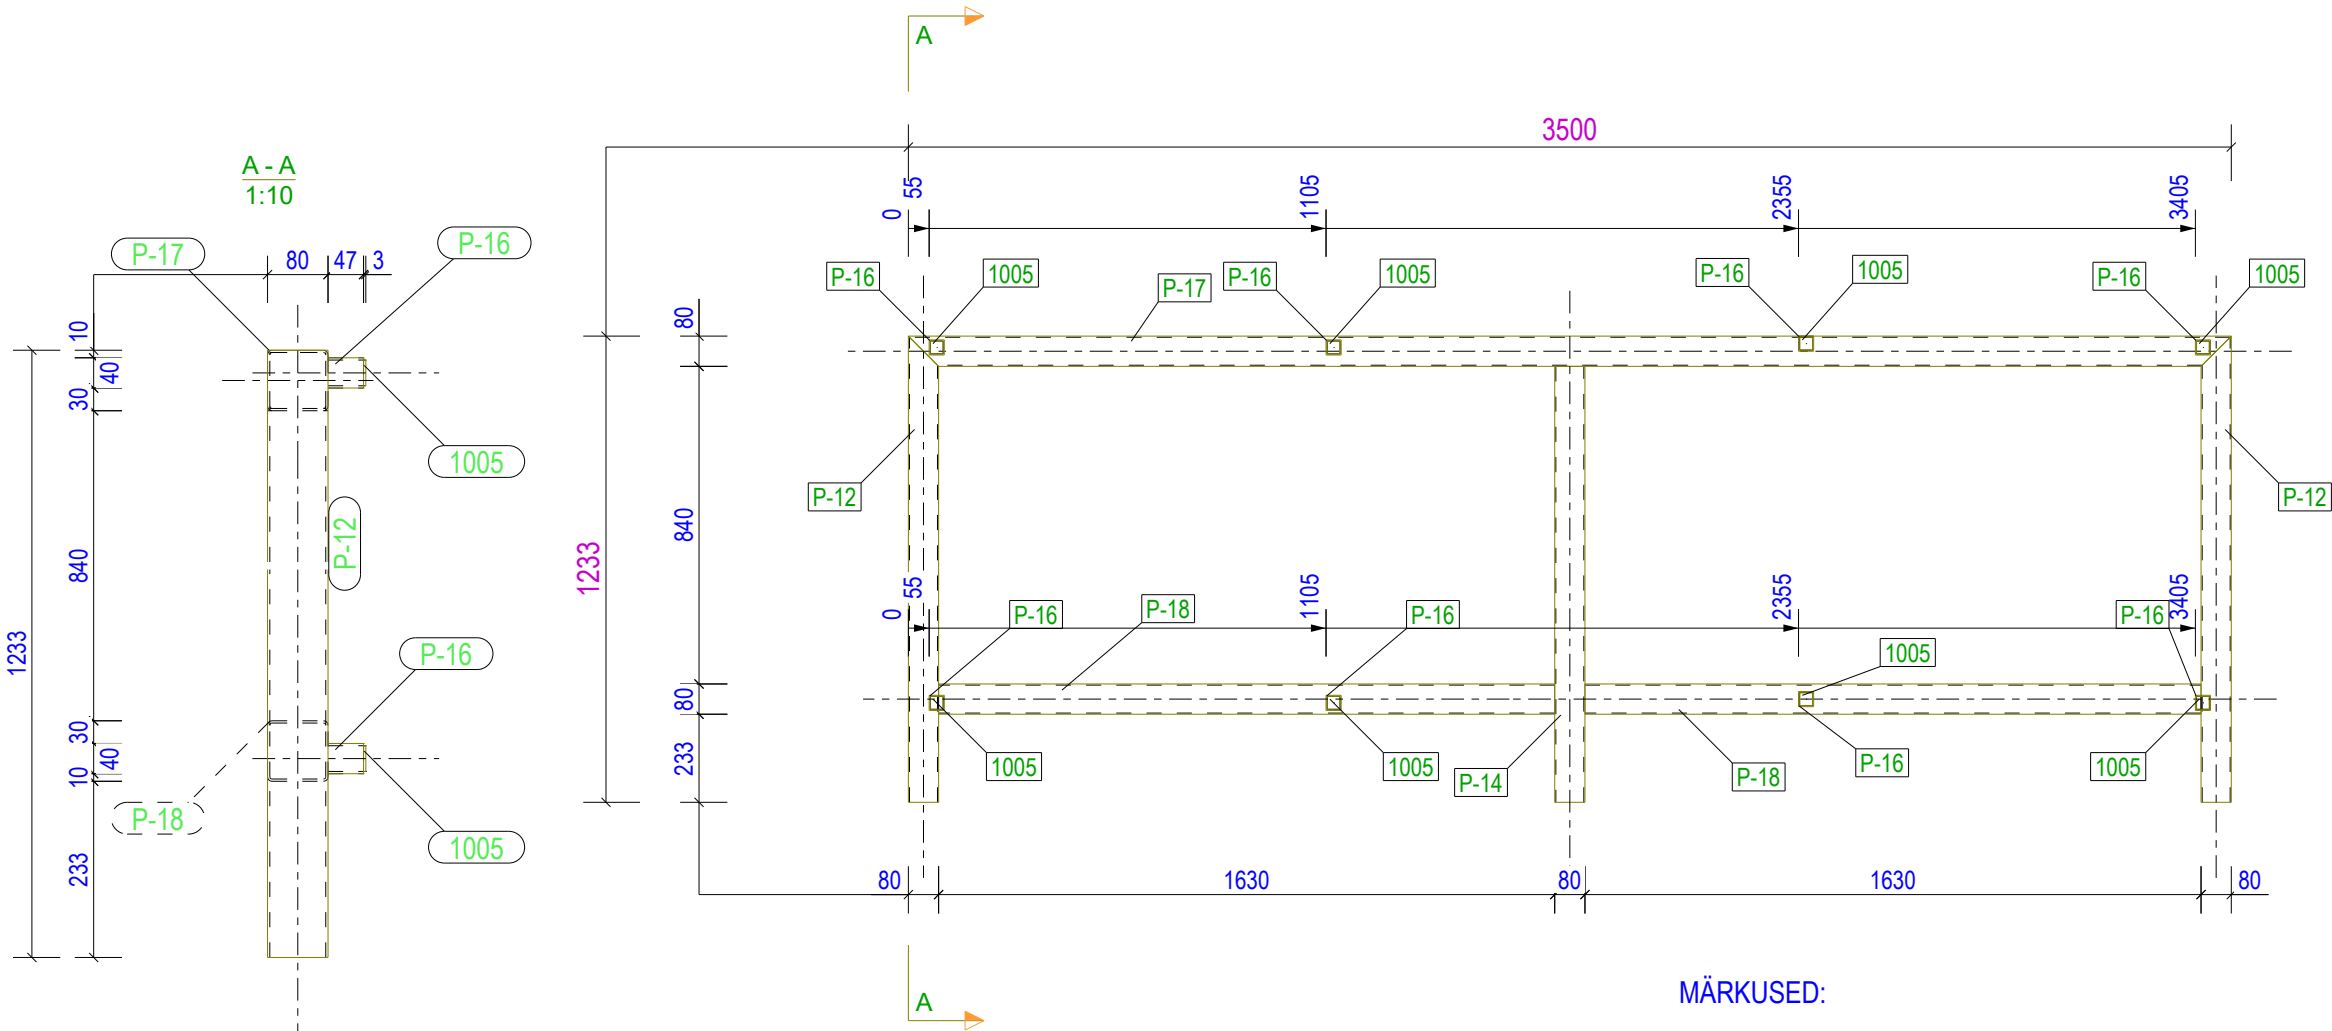

MÄRKUSED:

- 1) TERASE KLASS VASTAVALT SPETS. TABELILE
- 2) KESKKONNAKLASS C3H (EVS-EN ISO 12944-2:2000)
- 3) KONSTRUKTSIOONIDE VALMISTAMISE JA MONTAAZHITOLERANTSID VASTAVALT STANDARDILE EVS 1090-2:2008+A1:2011
- 4) ELEKTROODID VALIDA VASTAVALT TERASE TUGEVUSKLASSILE
- 5) KEEVISE KLASS C, STANDARD EVS-EN ISO 5817:2014
- 6) MÄRKIMATA KEEVITUSED: KÕRGUS VÕTTA VÕRDNE KÕIGE ÕHEMA ELEMENDI SEINAPAKSUSEGA, AGA MITTE VÄIKSEM, KUI a4
- 7) TERASE STANDARDID: EN 10219-1 JA EN 10219-2 (TORUPROFIILID), EN 10025 (KÕIK TEISED)
- 8) MATERJALI KOKKUVÕTE ÜHELE ELEMENDILE

OBJEKTI NIMI: Ridaelamud		KUUPÄEV 10.03.2025	
AADRESS: Komeedi tn. 1, 2 ja Kuu tee 16, Saku, 75501 Harju mk			
PROJEKT: O.Paavo	JOONISE SISU:		MÕÕTKAVA 1:10 1:20
KONTROLLIS:	Varikatus VK-2		
		PROJ.STAADIUM: TP	TÖÖ NR. 2024.10
			JOON.NR. EK-9-022