


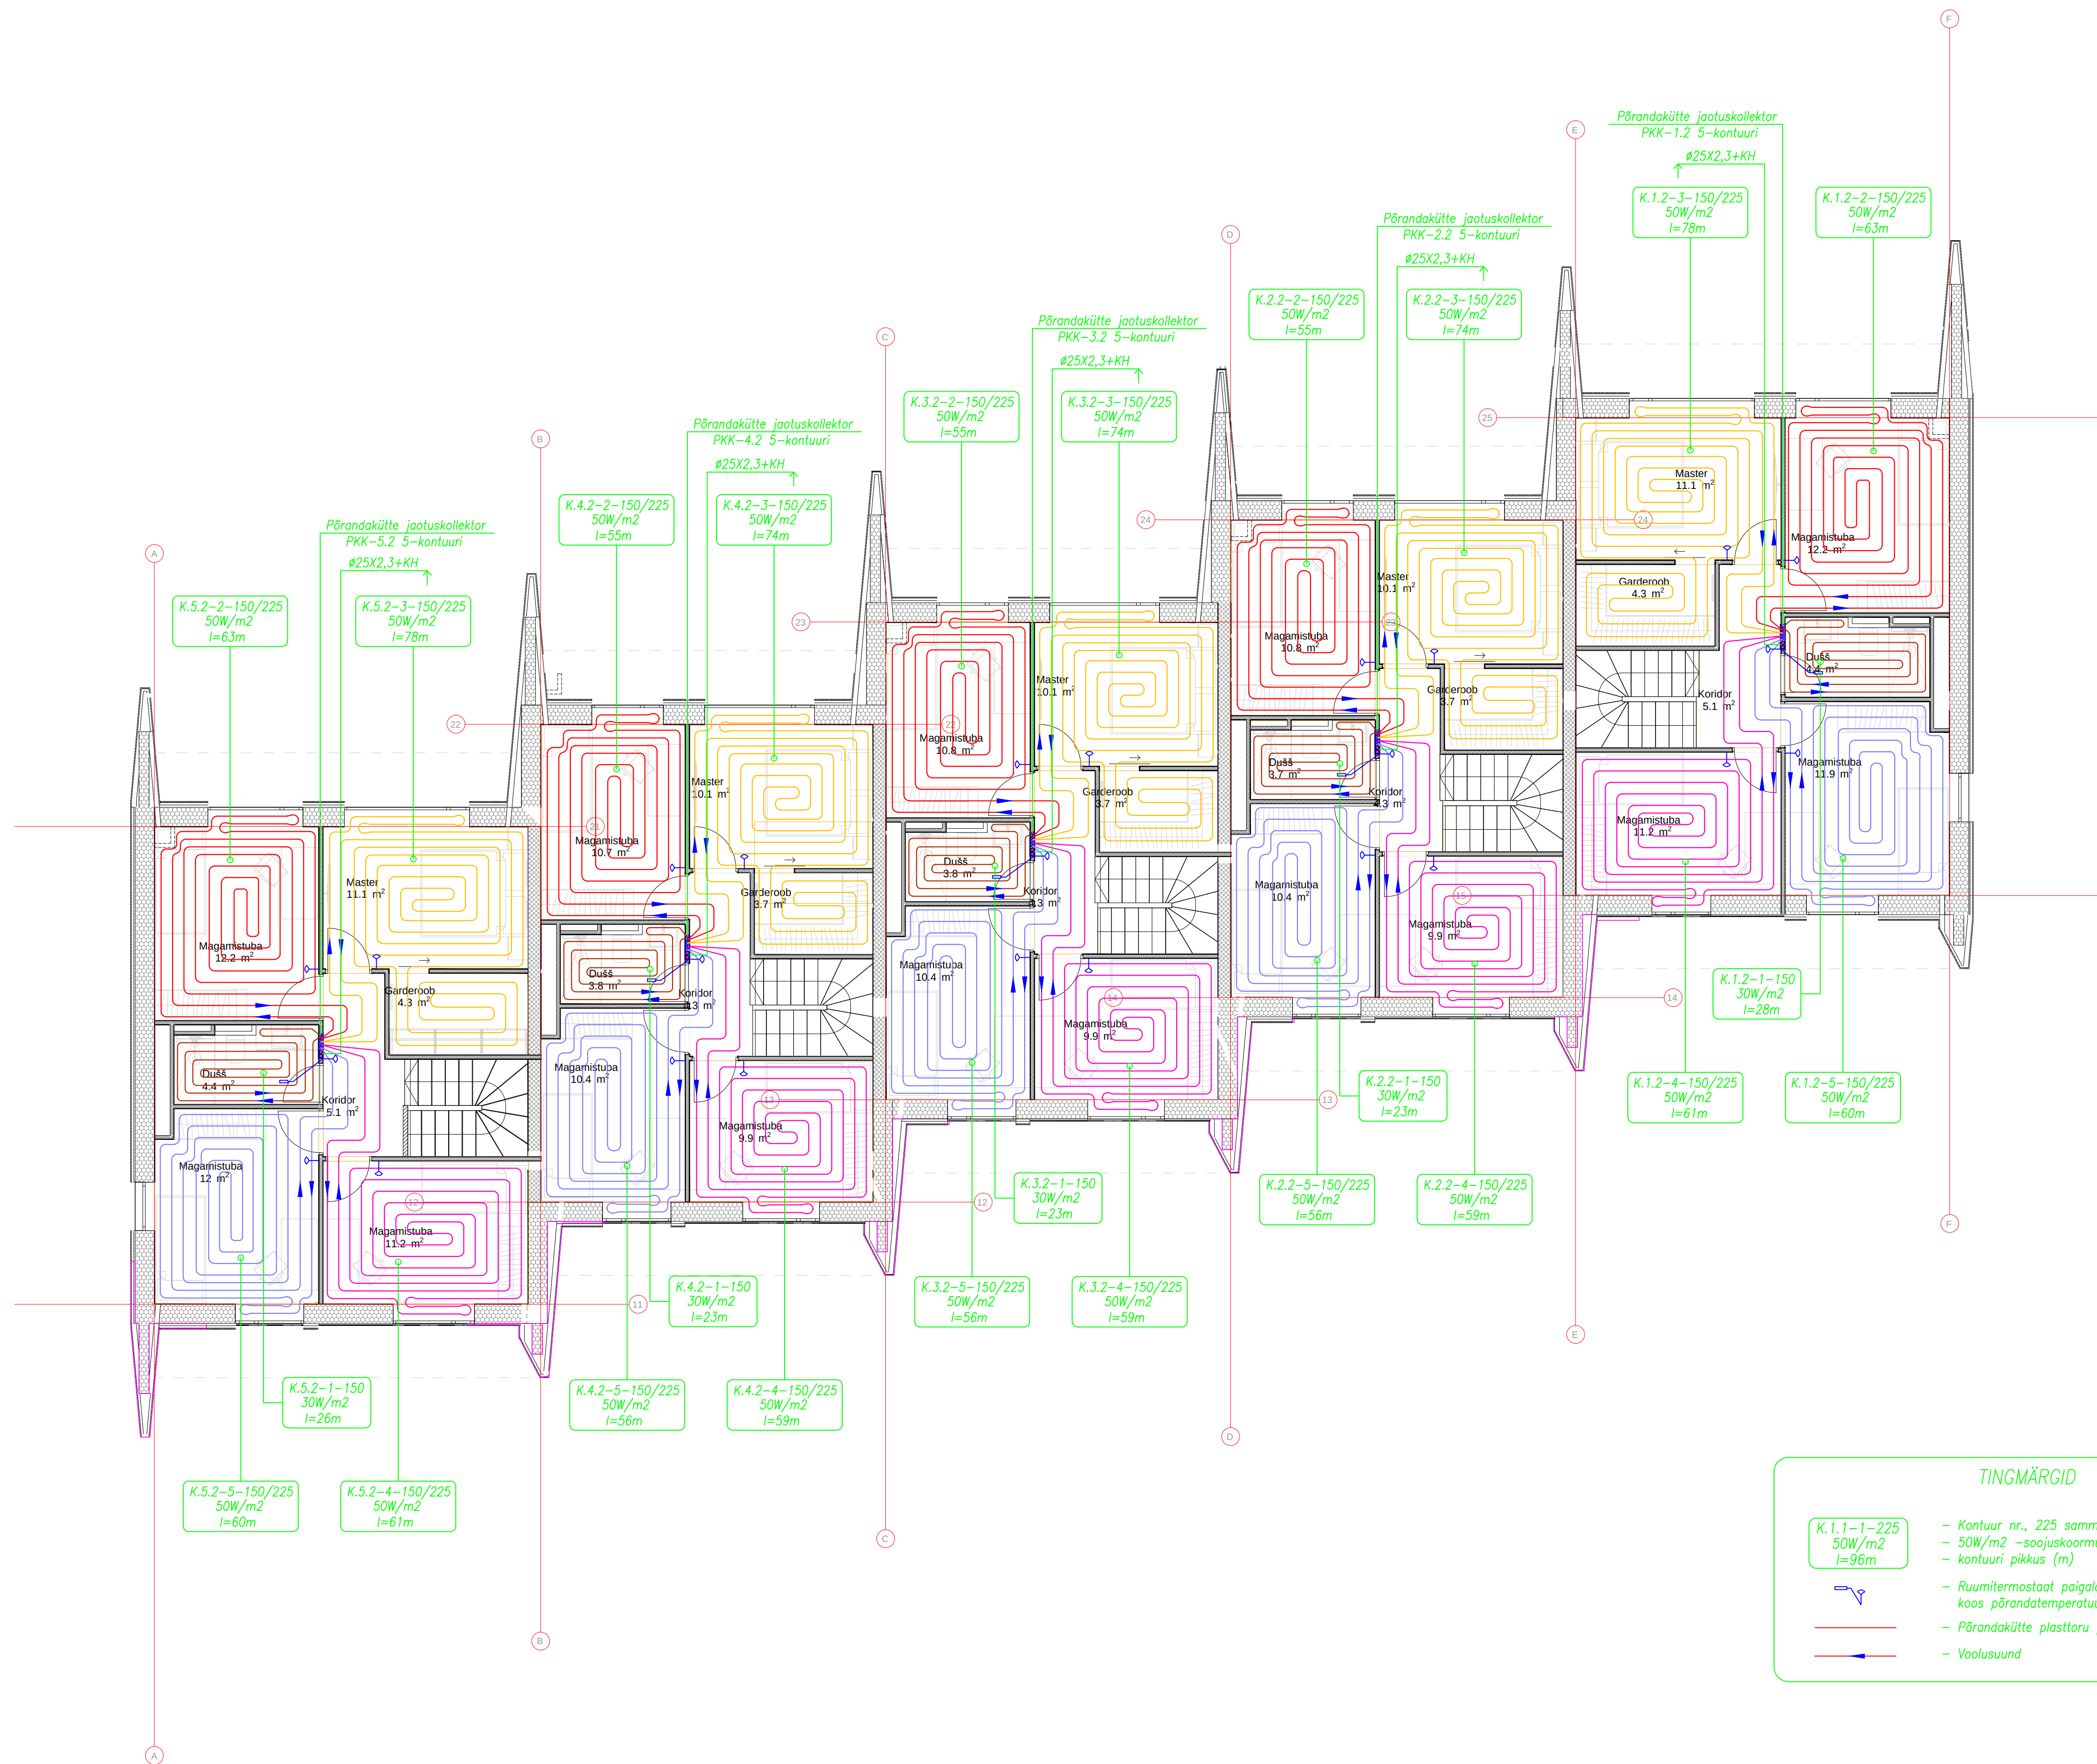

 KVVK PROJEKT OÜ EEP 002365 tel. 5149080 kvvkprojekt@gmail.com		Tellija NOBE OÜ		Töö nr. KV-205-24	
		Objekt Saku Ridaelamu		Joonise nr. KVK-5-02	
Projekteerija	Vladimir Krehov	Aadress Kuu tee 16, Saku		Staadium	PP
Vastutav spets.	Vladimir Krehov			Möötkava	M 1:100
		Joonis 2. korruse plaan. Küte			
		Fail 09.04.25 KV20524_PP_KVK-5-02_2K-küte.dwg		Kuupäev	09.04.2025