



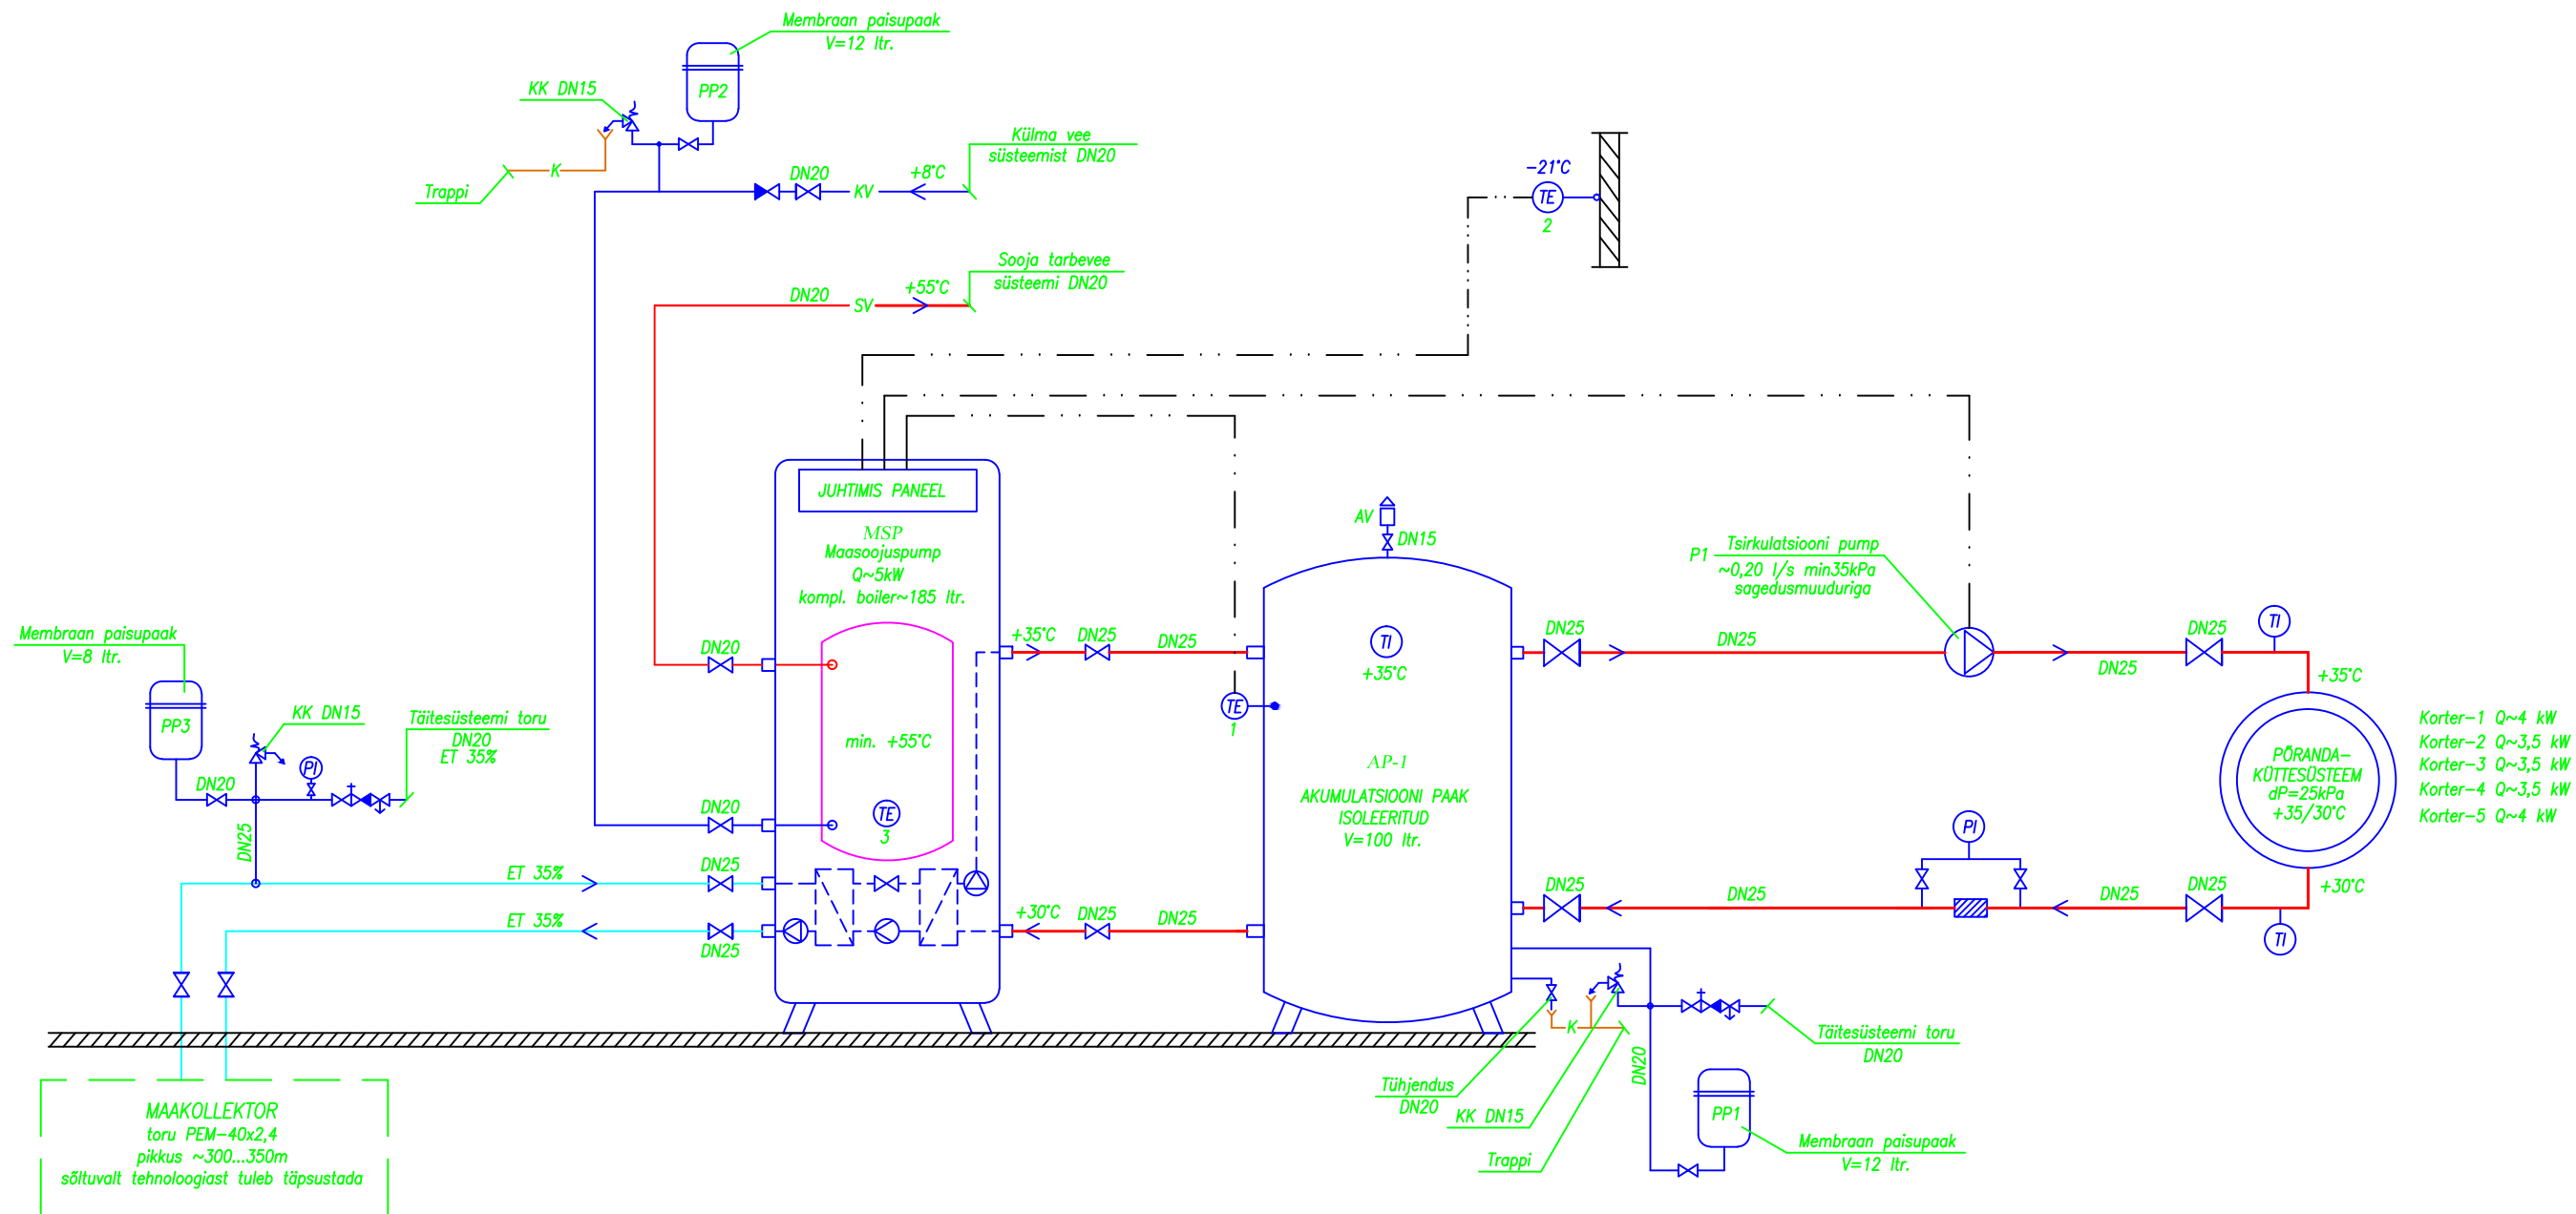

TINGMÄRGID

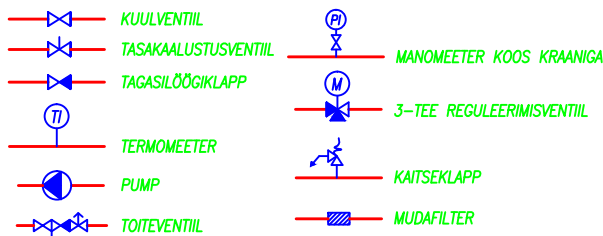

TÖÖPÕHIMÖTE

Küttesüsteemi sekundaarpool
Reguleerimiskeskus juhib soojuspumba tööd nii, et kütteveetemperatuur mõõdetuna temperatuuranduriga TE-1 püsib etteantud suuruses. Välisõhu temperatuuri muutudes anduril TE-2 muudab reguleerimiskeskus kütteveetemperatuuri vastavalt etteantud küttegaafikule.

Sooja tarbevee soojendamine
Reguleerimiskeskus juhib soojuspumba MSP tööd nii, et sooja tarbevee temperatuur mõõdetuna anduriga TE-3 vastaks ettenähtule (näiteks 55 °C). Sooja vee tootmine on primaarne võrreldes kütteveetootmisega.

 KVVK PROJEKT OÜ EEP 002365 tel. 5149080 kvvkprojekt@gmail.com			Tellija NOBE OÜ		Töö nr. KV-205-24	
			Objekt Saku Ridaelamu		Joonise nr. KVK-5-03	
Projekteerija	Vladimir Krehov		Aadress Kuu tee 16, Saku		Staadium	PP
Vastutav spets.	Vladimir Krehov					
			Joonis SOOJUSVARUSTUSE PÕHIMÕTTELINE SKEEM		Mõõtkava	
			Fail 09.04.25 KV20524_PP_KVK-5-03_SV-skeem.dwg		Kuupäev	09.04.2025