


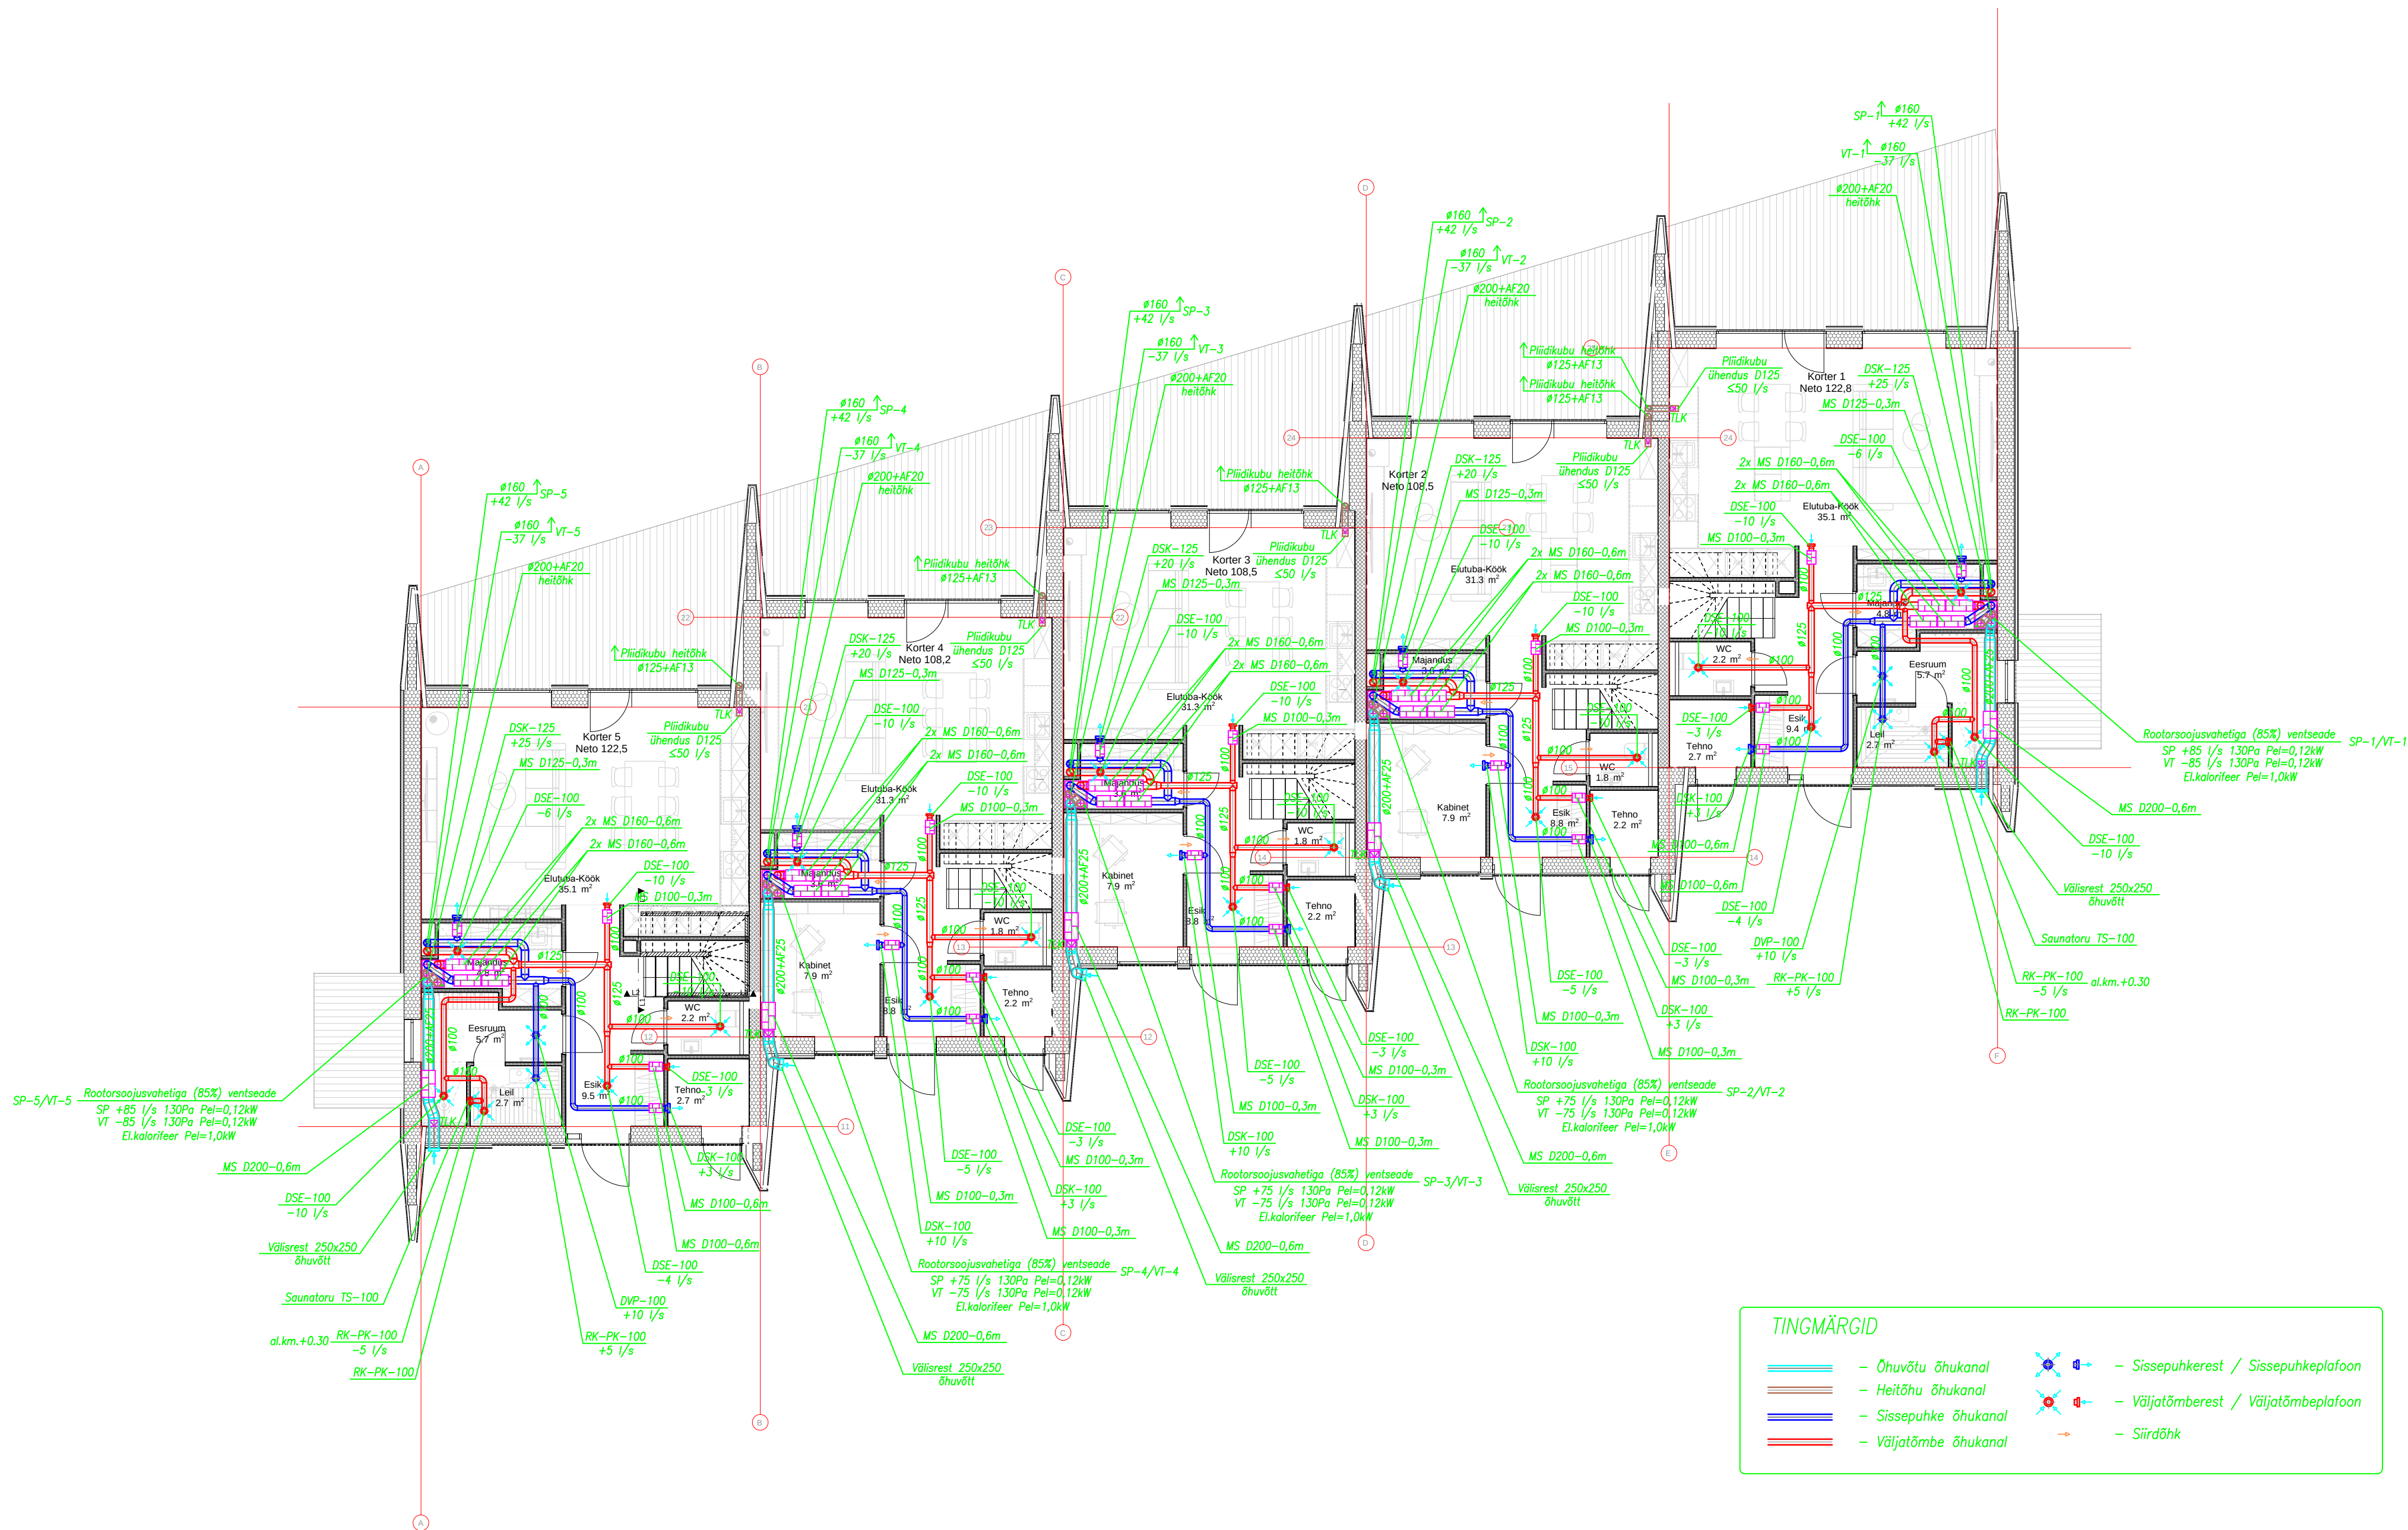

 KVVK PROJEKT OÜ EEP 002365 tel. 5149080 kvvprojekt@gmail.com		Tellija NOBE OÜ		Töö nr. KV-205-24	
		Objekt Saku Ridaelamu		Joonise nr. KVV-5-01	
Projekteerija	Vladimir Krehov	Address Kuu tee 16, Saku		Staadium	PP
Vastutav spets.	Vladimir Krehov	Joonis 1. korruse plaan. Ventilatsioon		Mõõtkava	M 1:100
Fail 11.05.25 KV20524_PP_KVV-5-01_1K-ventilatsioon.dwg		Kuupäev		09.05.2025	