


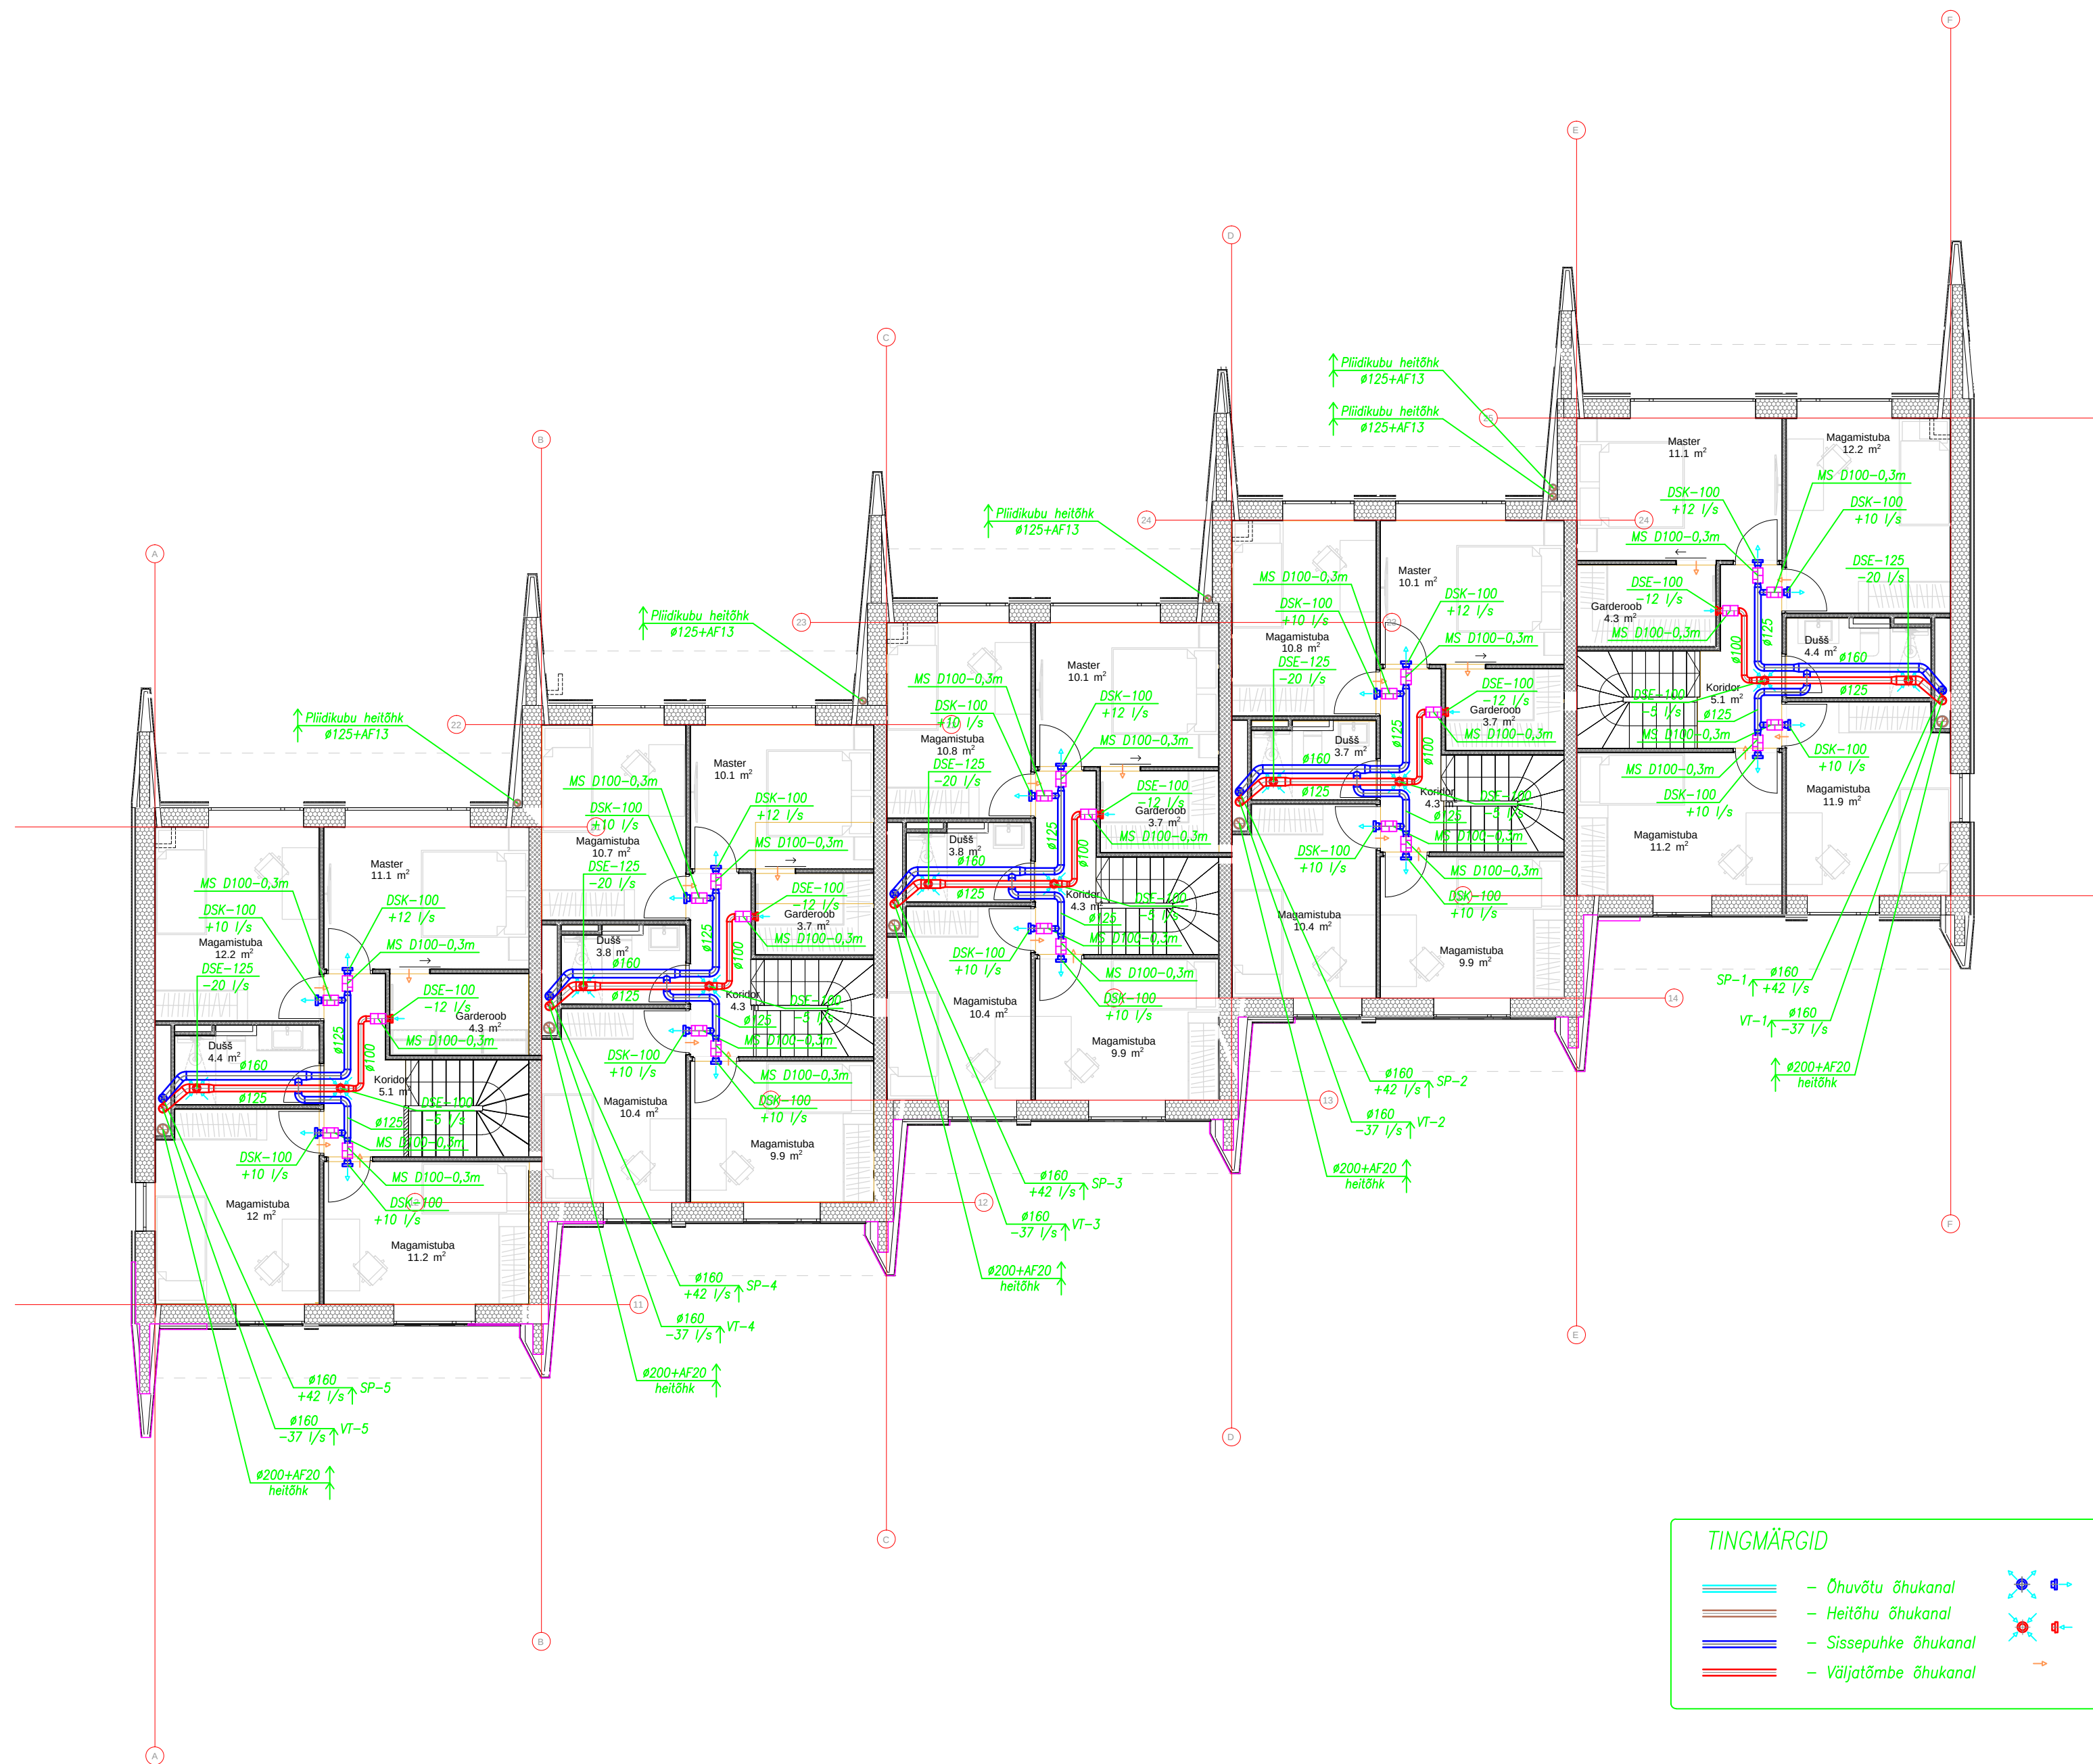

 KVVK PROJEKT OÜ EEP 002365 tel. 5149080 kvvkprojekt@gmail.com			Tellija NOBE OÜ		Töö nr. KV-205-24		
			Objekt Saku Ridaelamu		Joonise nr. KVV-5-02		
Projekteerija	Vladimir Krehov		Address Kuu tee 16, Saku			Staadium	PP
Vastutav spets.	Vladimir Krehov		Joonis 2. korruse plaan. Ventilatsioon				
			Fail 11.05.25 KV20524_PP_KVV-5-02_2K-ventilatsioon.dwg			Kuupäev	09.05.2025