


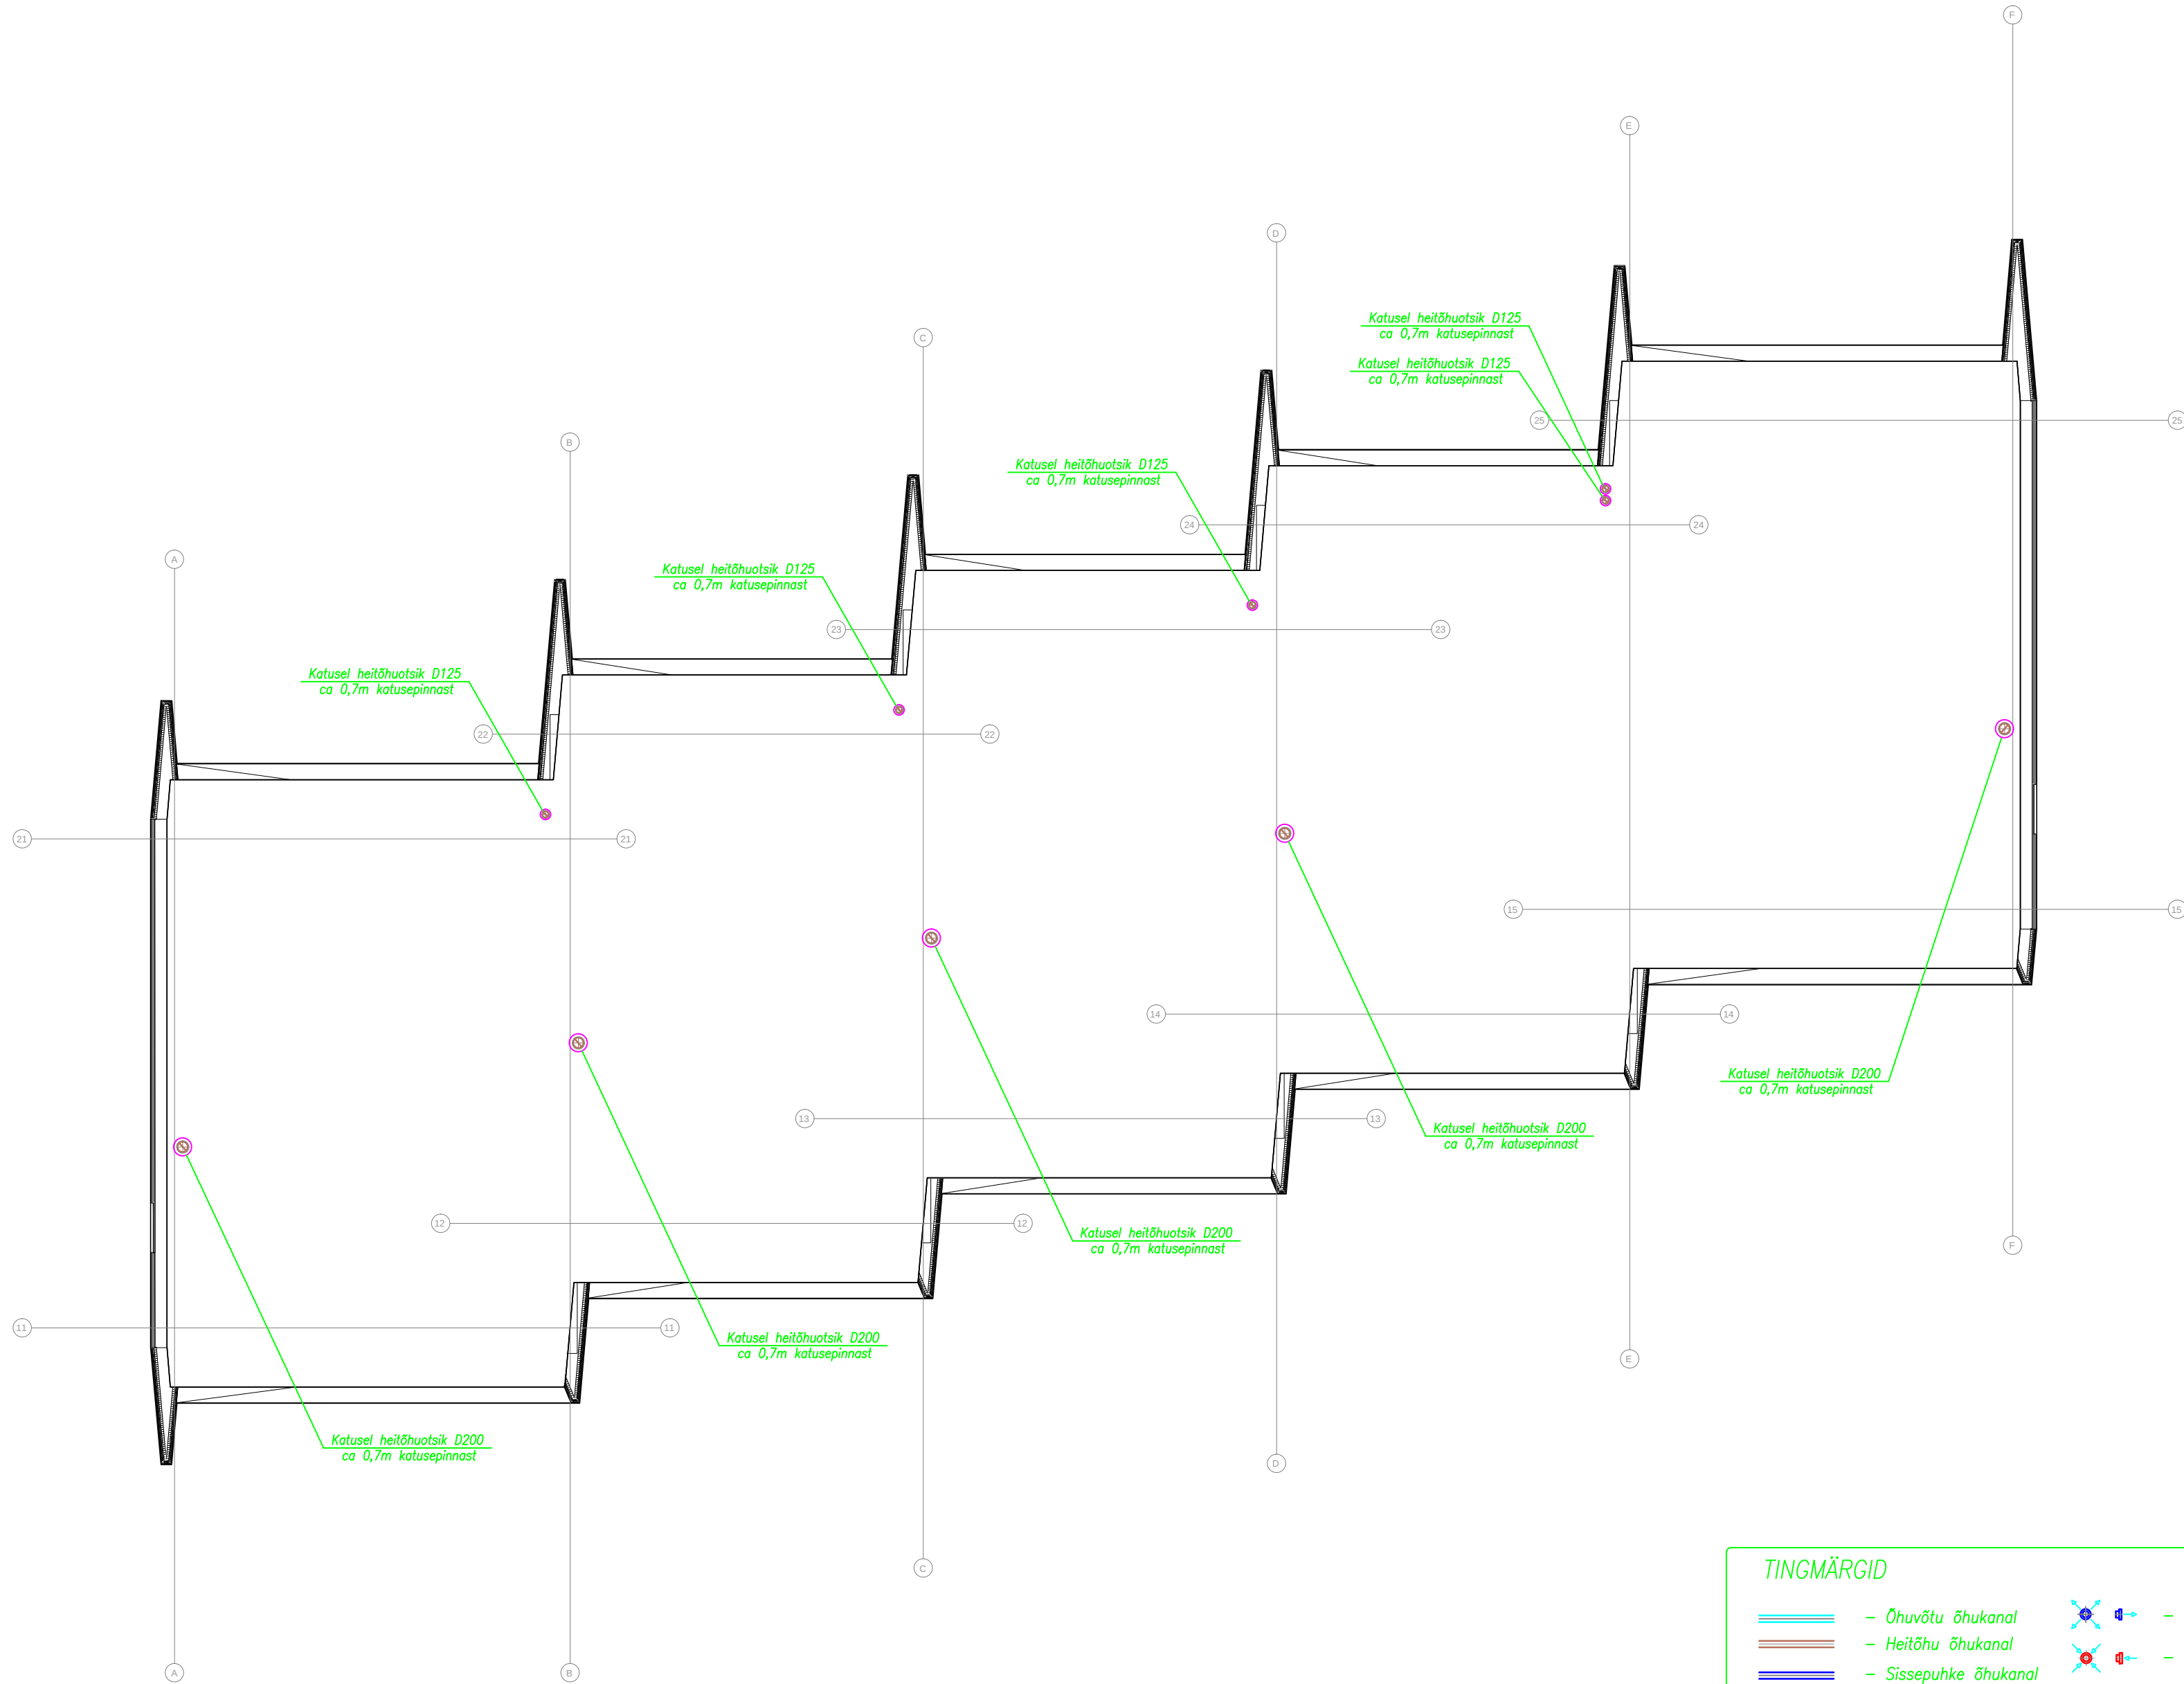

TINGMÄRGID

	- Õhuvõtu õhukanal		- Sisepuhkerest / Sisepuhkeplafoon
	- Heitõhu õhukanal		- Väljatõmberest / Väljatõmbeplafoon
	- Sisepuhke õhukanal		- Siirdõhk
	- Väljatõmbe õhukanal		

 KVVK PROJEKT OÜ EEP 002365 tel. 5149080 kvvkprojekt@gmail.com			Tellija NOBE OÜ		Töö nr. KV-205-24	
			Objekt Saku Ridaelamu		Joonise nr. KVV-5-03	
Projekteerija	Vladimir Krehov		Aadress Kuu tee 16, Saku		Staadium	PP
Vastutav spets.	Vladimir Krehov		Joonis Katuse plaan. Ventilatsioon		Mõõtkava	M 1:100
					Mõõtkava	M 1:100
			Fail 11.05.25 KV20524_PP_KVV-5-03_Katus-ventilatsioon.dwg		Kuupäev	09.05.2025